

FÖRKLARINGAR

SYSTEM + LÖPNUMMER
MATERIAL + VARIANTNR
DIMENSION
ISOLERINGSTYP

SYSTEM VÄRME
FJV1 FJÄRRVÄRME

SYSTEM TAPPVATTEN

KV1 KALLVATTEN, OAVHÄRDAT, 5 °C
KV2 KALLVATTEN, AVHÄRDAT, 5 °C
VV1 VARMVATTEN, 55°C
VV2 VARMVATTENCIRKULATION, 50°C

SYSTEM SPILLVATTEN

D1 DAGVATTEN, ALLMÄNT I MARK
S1 SPILLVATTEN, ALLMÄNT I MARK
S2 SPILLVATTEN, ALLMÄNT INOMHUS
S3 SPILLVATTEN FRÅN STORKÖK

MATERIAL RÖR

E13 PEM, TRYCKRÖR
S6 STÅLRÖR, TUBRÖR TRYCKKÄRLSKVALITET, SVETSFÖG
X31 LEDNINGAR AV PEX (PE-XA) MED RIR

MATERIAL SPILLVATTEN

E4 PE-RÖR, TRYCKRÖR, PN16
P2 LEDNINGAR AV PP-RÖR, SLÄTA
MARKAVLOPPSRÖR I BYGGNAD
R8 LEDNINGAR AV ROSTFRIA RÖR

ISOLERING

W MINERALULL FABRIKSMONTERAD ALU-PLÅT
V CELLGUMMISLANG
YTBEKLÄDNAD
B PLASTPLÅT
C MÖNSTERPRÄGLAD ALU-PLÅT

KOMPONENTER

ALxxx AVLUFTARE
Bxxx GOLVBRUNN
BLxxx BLÅNDARE
DBxxx DISKBÄNKAR
DM DISKMASKIN
IL INSPEKTIONSLUCKA (UTFÖRS AV BE)
KM KÖMBÄSKIN
RLx RENSÖR, MED LOCK
SL1 SERVICELUCKA, 150x150, INGÅR I BE
TM TVÄTTMASKIN
TSxxx TVÄTTSTALL
VL0xxx VÄTTENLÄS
VKxxx VATTENKLOSETT

ÖVRIGT

ANSL ANSLUTNING
CL CENTRUMLINJE
FG FÄRDIGT GOLV
ÖFG ÖVER (FÄRDIGT) GOLV
INK INKÖPLING
UK UNDERKANT
VG VATTENGÅNG
(L) AVLOPPSFLUTARE

KOPPLINGSLEDNINGAR

FÖLJANDE GÄLLER OM EJ ANNAT ANGES:

DÖLDA KV/VV/IL-ZI-X31

ANSL	KV	VV	S
B	-	-	75
BL	16(15)	16(15)	-
TS	16(12)	16(12)	75
UB	16(12)	16(12)	75
VK	16(12)	-	110

B	ENL. PM-2	2024-05-07	A.B.
A	ENL. PM-1	2024-04-19	A.B.
REV	ÄNDRINGEN AVSER	DATUM	SIGN

BYGGHANDLING

FASTIGHETSBETECKNING
OSTRA KASERN 3



Kristianstads
kommun

Västra Storgatan 12
291 80 KRISTIANSTAD

Telefon: 044-13 50 00



A			
K			
V			
E			
X	L VINNERSI AB	+46 101 02 44 00	
B			
SK			
ANSVARIG L.F.	RITAD/KONSTR AV A.B.	HANDLGGARE L.F.	
PROJEKT NR 2029304	DATUM 2024-03-01	REV.DATUM 2024-05-07	
OBJEKTID 268140	HUS AA	VÄRNING 01	DISCIPLIN W

ALLÖSKOLAN - HUS AA

VS-INSTALLATIONER
RÖR UNDER BOTTENPLATTA- DEL 1



FORMAT

SKALA A1 (A3) 1:50 (1:100)	RITINGSNUMMER W-50-1-A-0011	BET B
-------------------------------	--------------------------------	----------

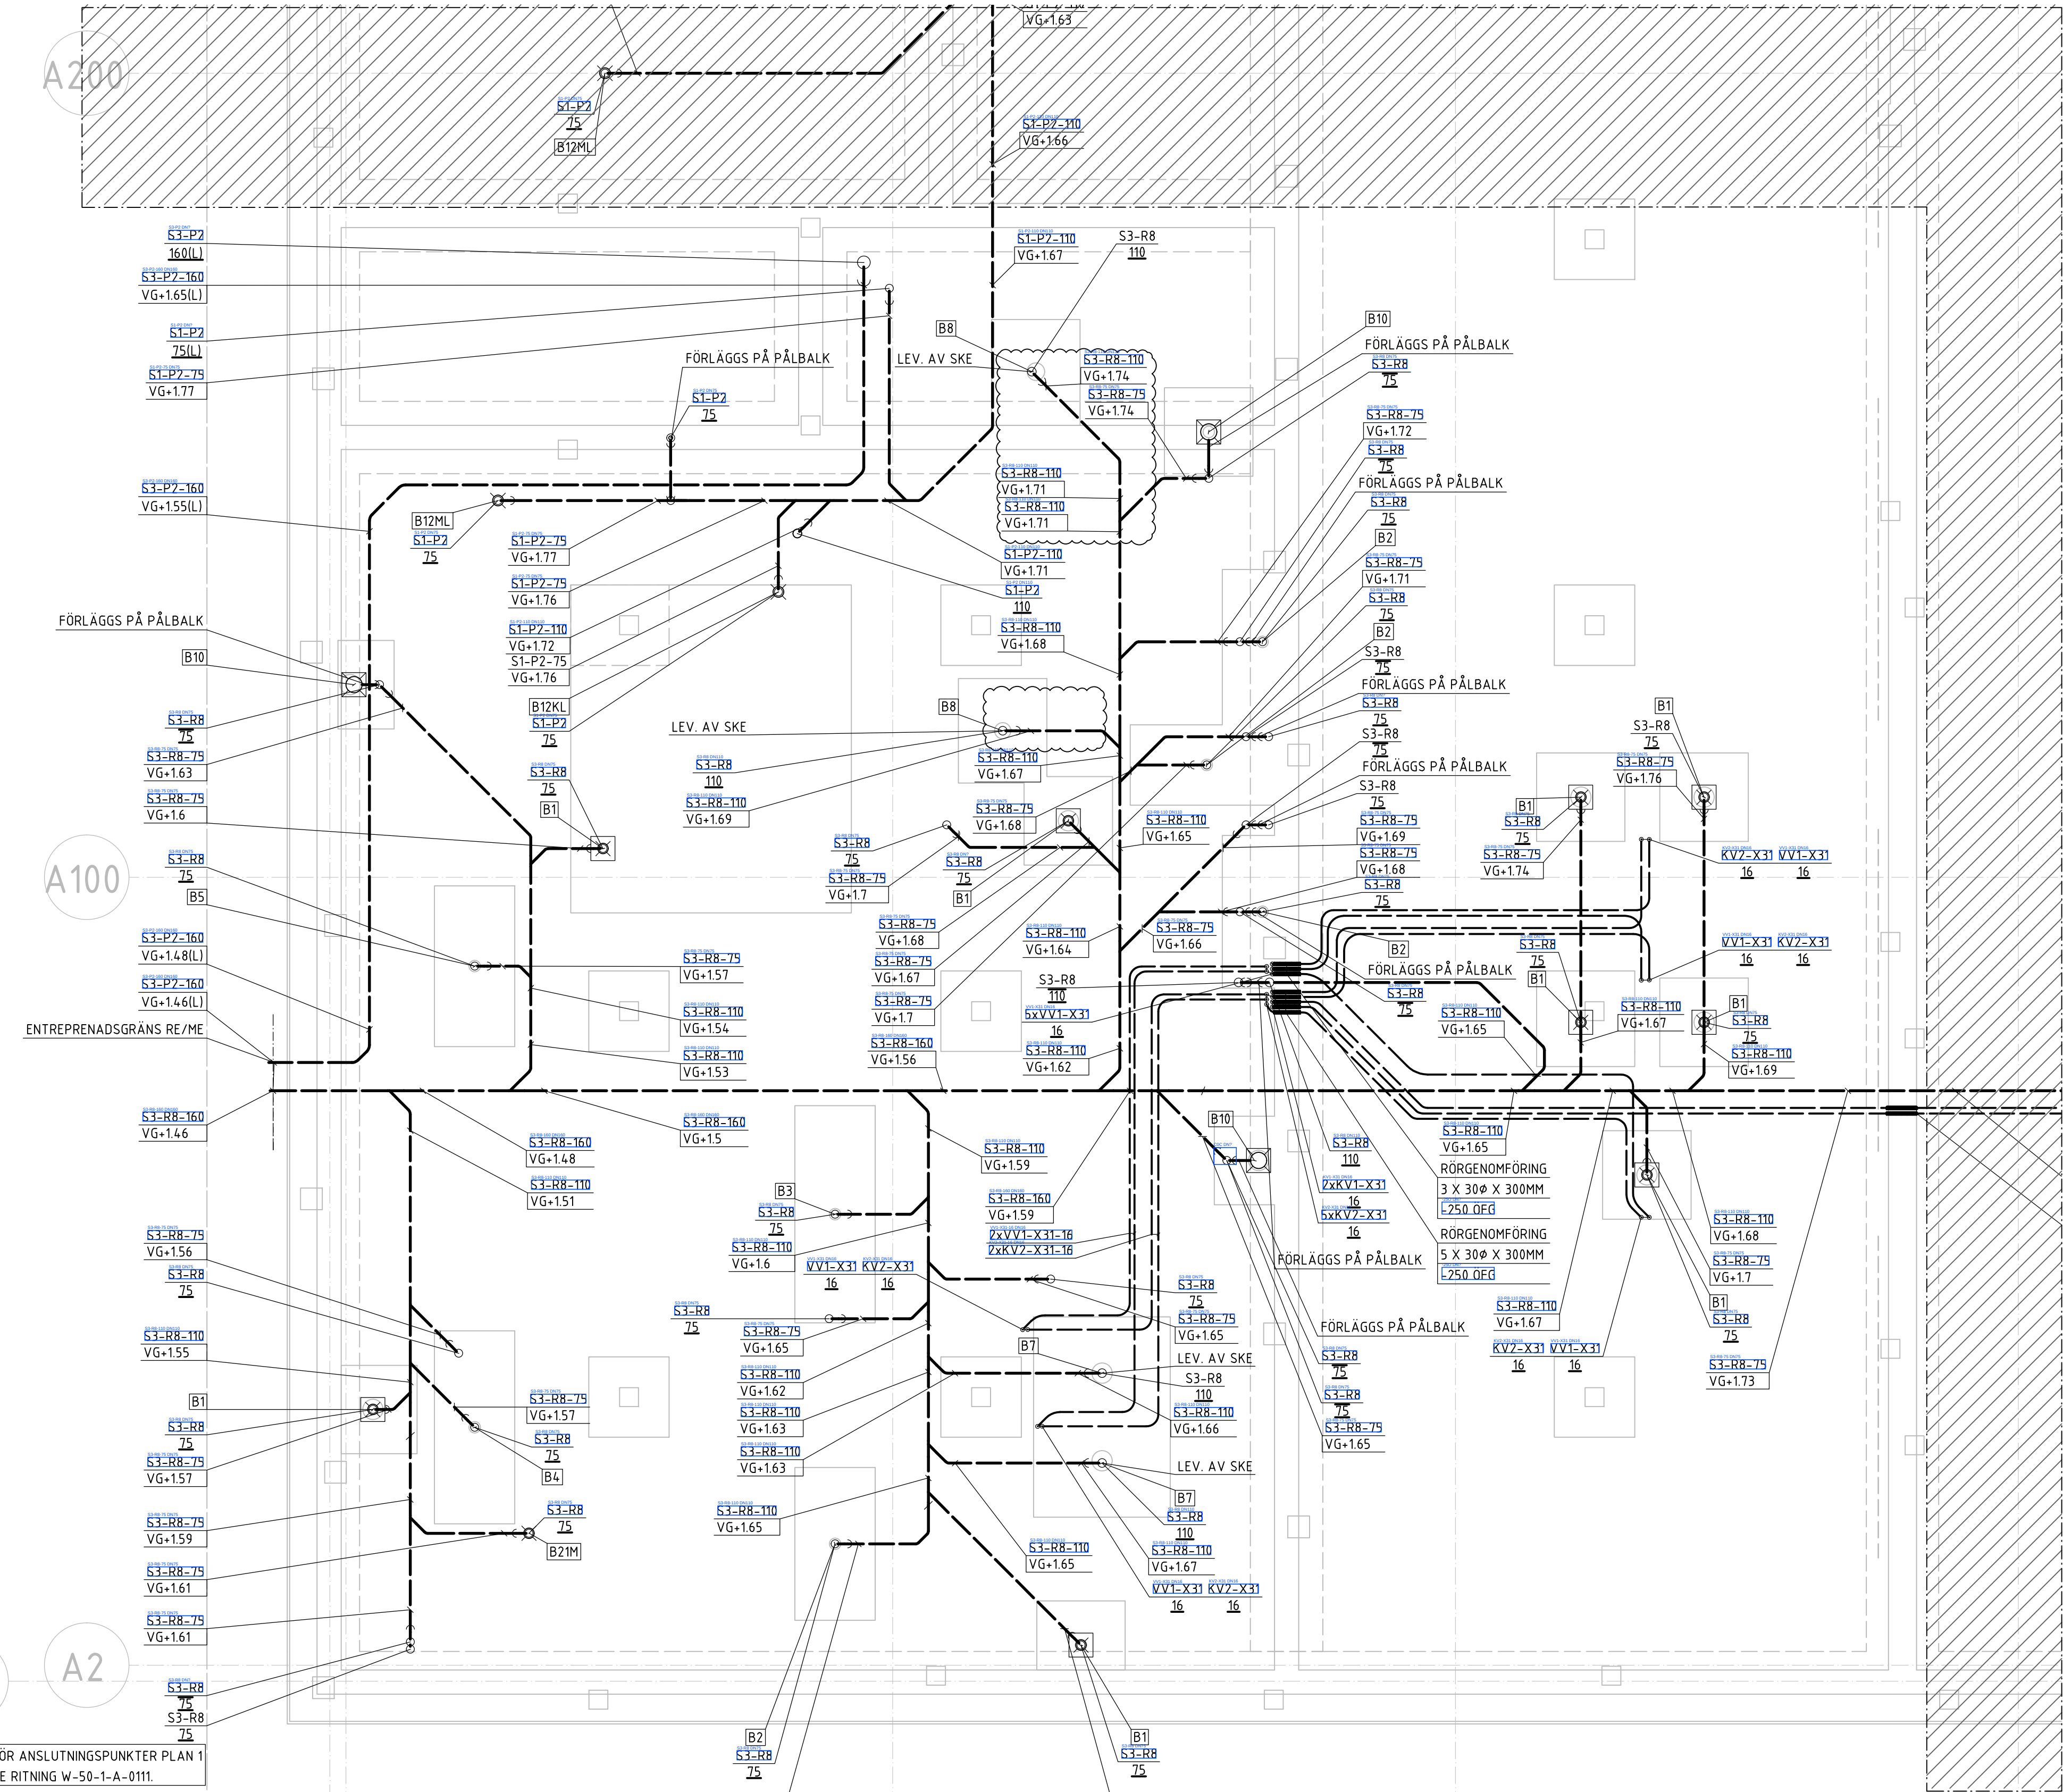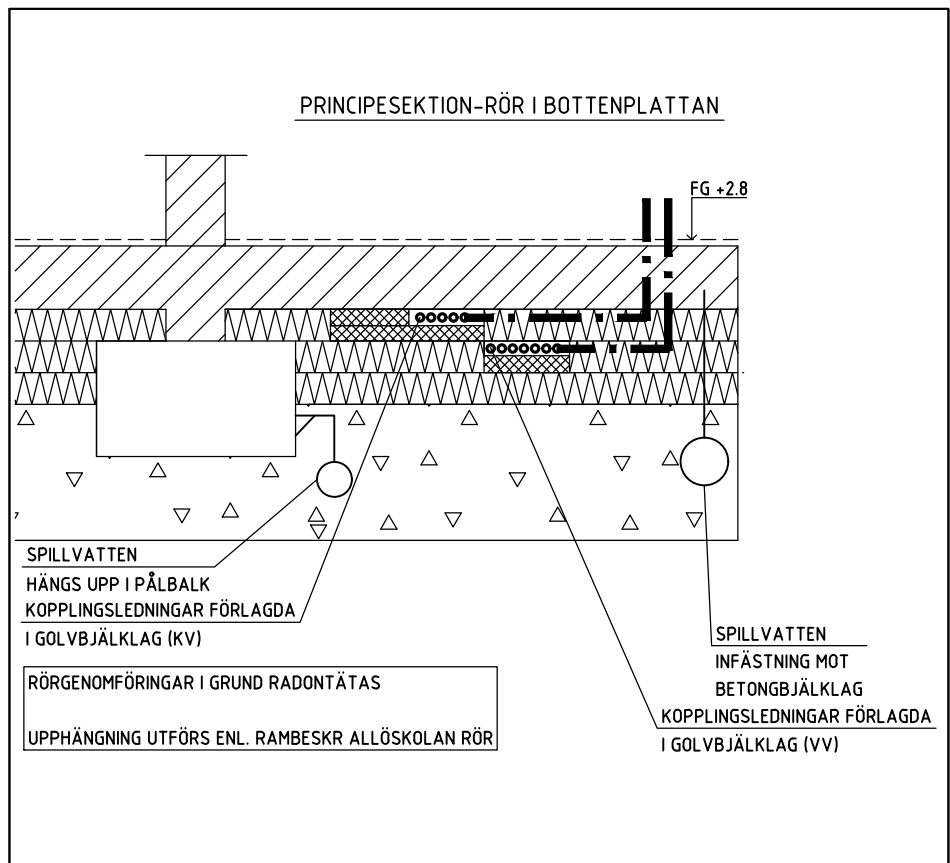

INGÅR I VS
B1-GOLVBRUNN 300x300 (8st)
B2-GOLVRÄNNÄ 1000x150 (4st)
B3-GOLVRÄNNÄ 1900x150 (1st)
B4-GOLVRÄNNÄ 1600x150 (1st)
B5-GOLVRÄNNÄ 1200x150 (1st)
B10-GOLVBRUNN 300x300 (3st)

INGÅR I SKE
B7-GOLVBRUNN 900x600 (2st)
B8-GOLVRÄNNÄ 500x300 (2st)

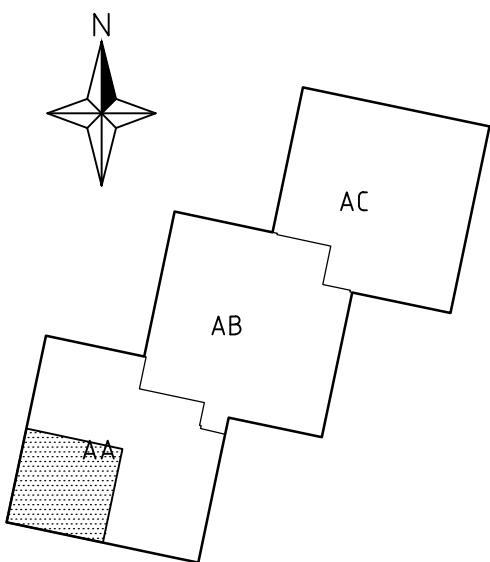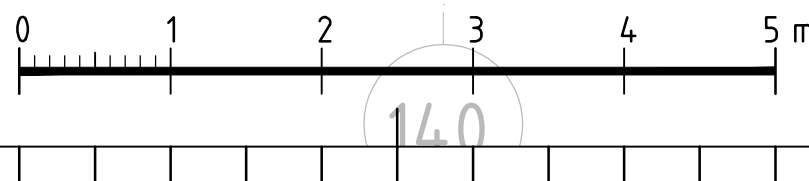

ORIENTERINGSPLAN