

FÖRKLARINGAR

SYSTEM + LÖPNUMMER
MATERIAL + VARIANTNR
DIMENSION
ISOLERINGTYP

XX00-X00-000/X00

SYSTEM VÄRME

FJV1 FJÄRRVÄRME

SYSTEM TAPPVATTEN

KV1 KALLVATTEN, OAVHÄRDAT, 5 °C

KV2 KALLVATTEN, AVHÄRDAT, 5 °C

VV1 VARMVATTEN, 55°C

VVC1 VARMVATTENCIRKULATION, 50°C

SYSTEM SPILLVATTEN

D1 DAGVATTEN, ALLMÄNT I MARK

S1 SPILLVATTEN, ALLMÄNT I MARK

S2 SPILLVATTEN, ALLMÄNT INOMHUS

S3 SPILLVATTEN FRÅN STORKÖK

MATERIAL RÖR

E13 PEM, TRYCKRÖR

S6 STÅLRÖR, TUBRÖR TRYCKKÄRLSKVALITET, SVETSFÖG

X31 LEDNINGAR AV PEX (PE-XA) MED RIR

MATERIAL SPILLVATTEN

E4 PE-RÖR, TRYCKRÖR, PN16

P2 LEDNINGAR AV PP-RÖR, SLÄTA

MARKAVLOPPSRÖR I BYGGNAD

R8 LEDNINGAR AV ROSTFRIA RÖR

ISOLERING

W MINERALULL FABRIKSMONTERAD ALU-PLÅT

V CELLGUMMISLANG

YTBEKLÄDNAD

B PLASTPLÅT

C MÖNSTERPRÄGLAD ALU-PLÅT

KOMPONENTER

ALxxx AVLÖFTARE

Bxxx GOLVBRUNN

BLxxx BLÅNDARE

DBxxx DISKBÄNKAR

DM DISKMASKIN

IL INSPEKTIONSLUCKA (UTFÖRS AV BE)

KM KOMBI-MASKIN

RLx RENSÖR, MED LOCK

SL1 SERVICELUCKA, 150x150, INGÅR I BE

TM TVÄTTMASKIN

TSxxx TVÄTTSTALL

VLOxxx VATTENLÄS

VKxxx VATTENKLOSETT

ÖVRIGT

ANSL ANSLUTNING

CL CENTRUMLINJE

FG FÄRDIGT GOLV

ÖFG ÖVER (FÄRDIGT) GOLV

INK INKÖPPLING

UK UNDERKANT

VG VATTENGÅNG

AVLOPPSLUFTARE

KOPPLINGSLEDNINGAR

FÖLJANDE GÄLLER OM EJ ANNAT ANGES:

DOLDA KV/VV(1-2)-X31

ANSL KV VV S

B - - 75

BL 16(15) 16(15) -

TS 16(12) 16(12) 75

UB 16(12) 16(12) 75

VK 16(12) - 110

B ENL. PM-2 2024-05-07 A.B.

A ENL. PM-1 2024-04-19 A.B.

REV ANT ÄNDRINGEN AVSER DATUM SIGN

BYGGHANDLING

FASTIGHETSBETECKNING

OSTRA KASERN 3



Västra Storgatan 12

291 80 KRISTIANSTAD

Telefon: 044-13 50 00

A

K

V

E

X L VINNERS AB +46 101 02 44 00

B

SK

ANSVARIG L.F.

RITAD/KONSTR AV A.B.

HANDLGGARE L.F.

PROJEKT NR 2029304

DATUM 2024-03-01

REV.DATUM 2024-05-07

OBJEKTID 268140

HUS AA

VARNING 01

DISCIPLIN W

ALLÖSKOLAN - HUS AA

VS-INSTALLATIONER





RÖR UNDER BOTTENPLATTA- DEL 1

FORMAT

SKALA A1 (A3) 1:50 (1:100)

RITINGSNUMMER W-50-1-A-0011

BET B

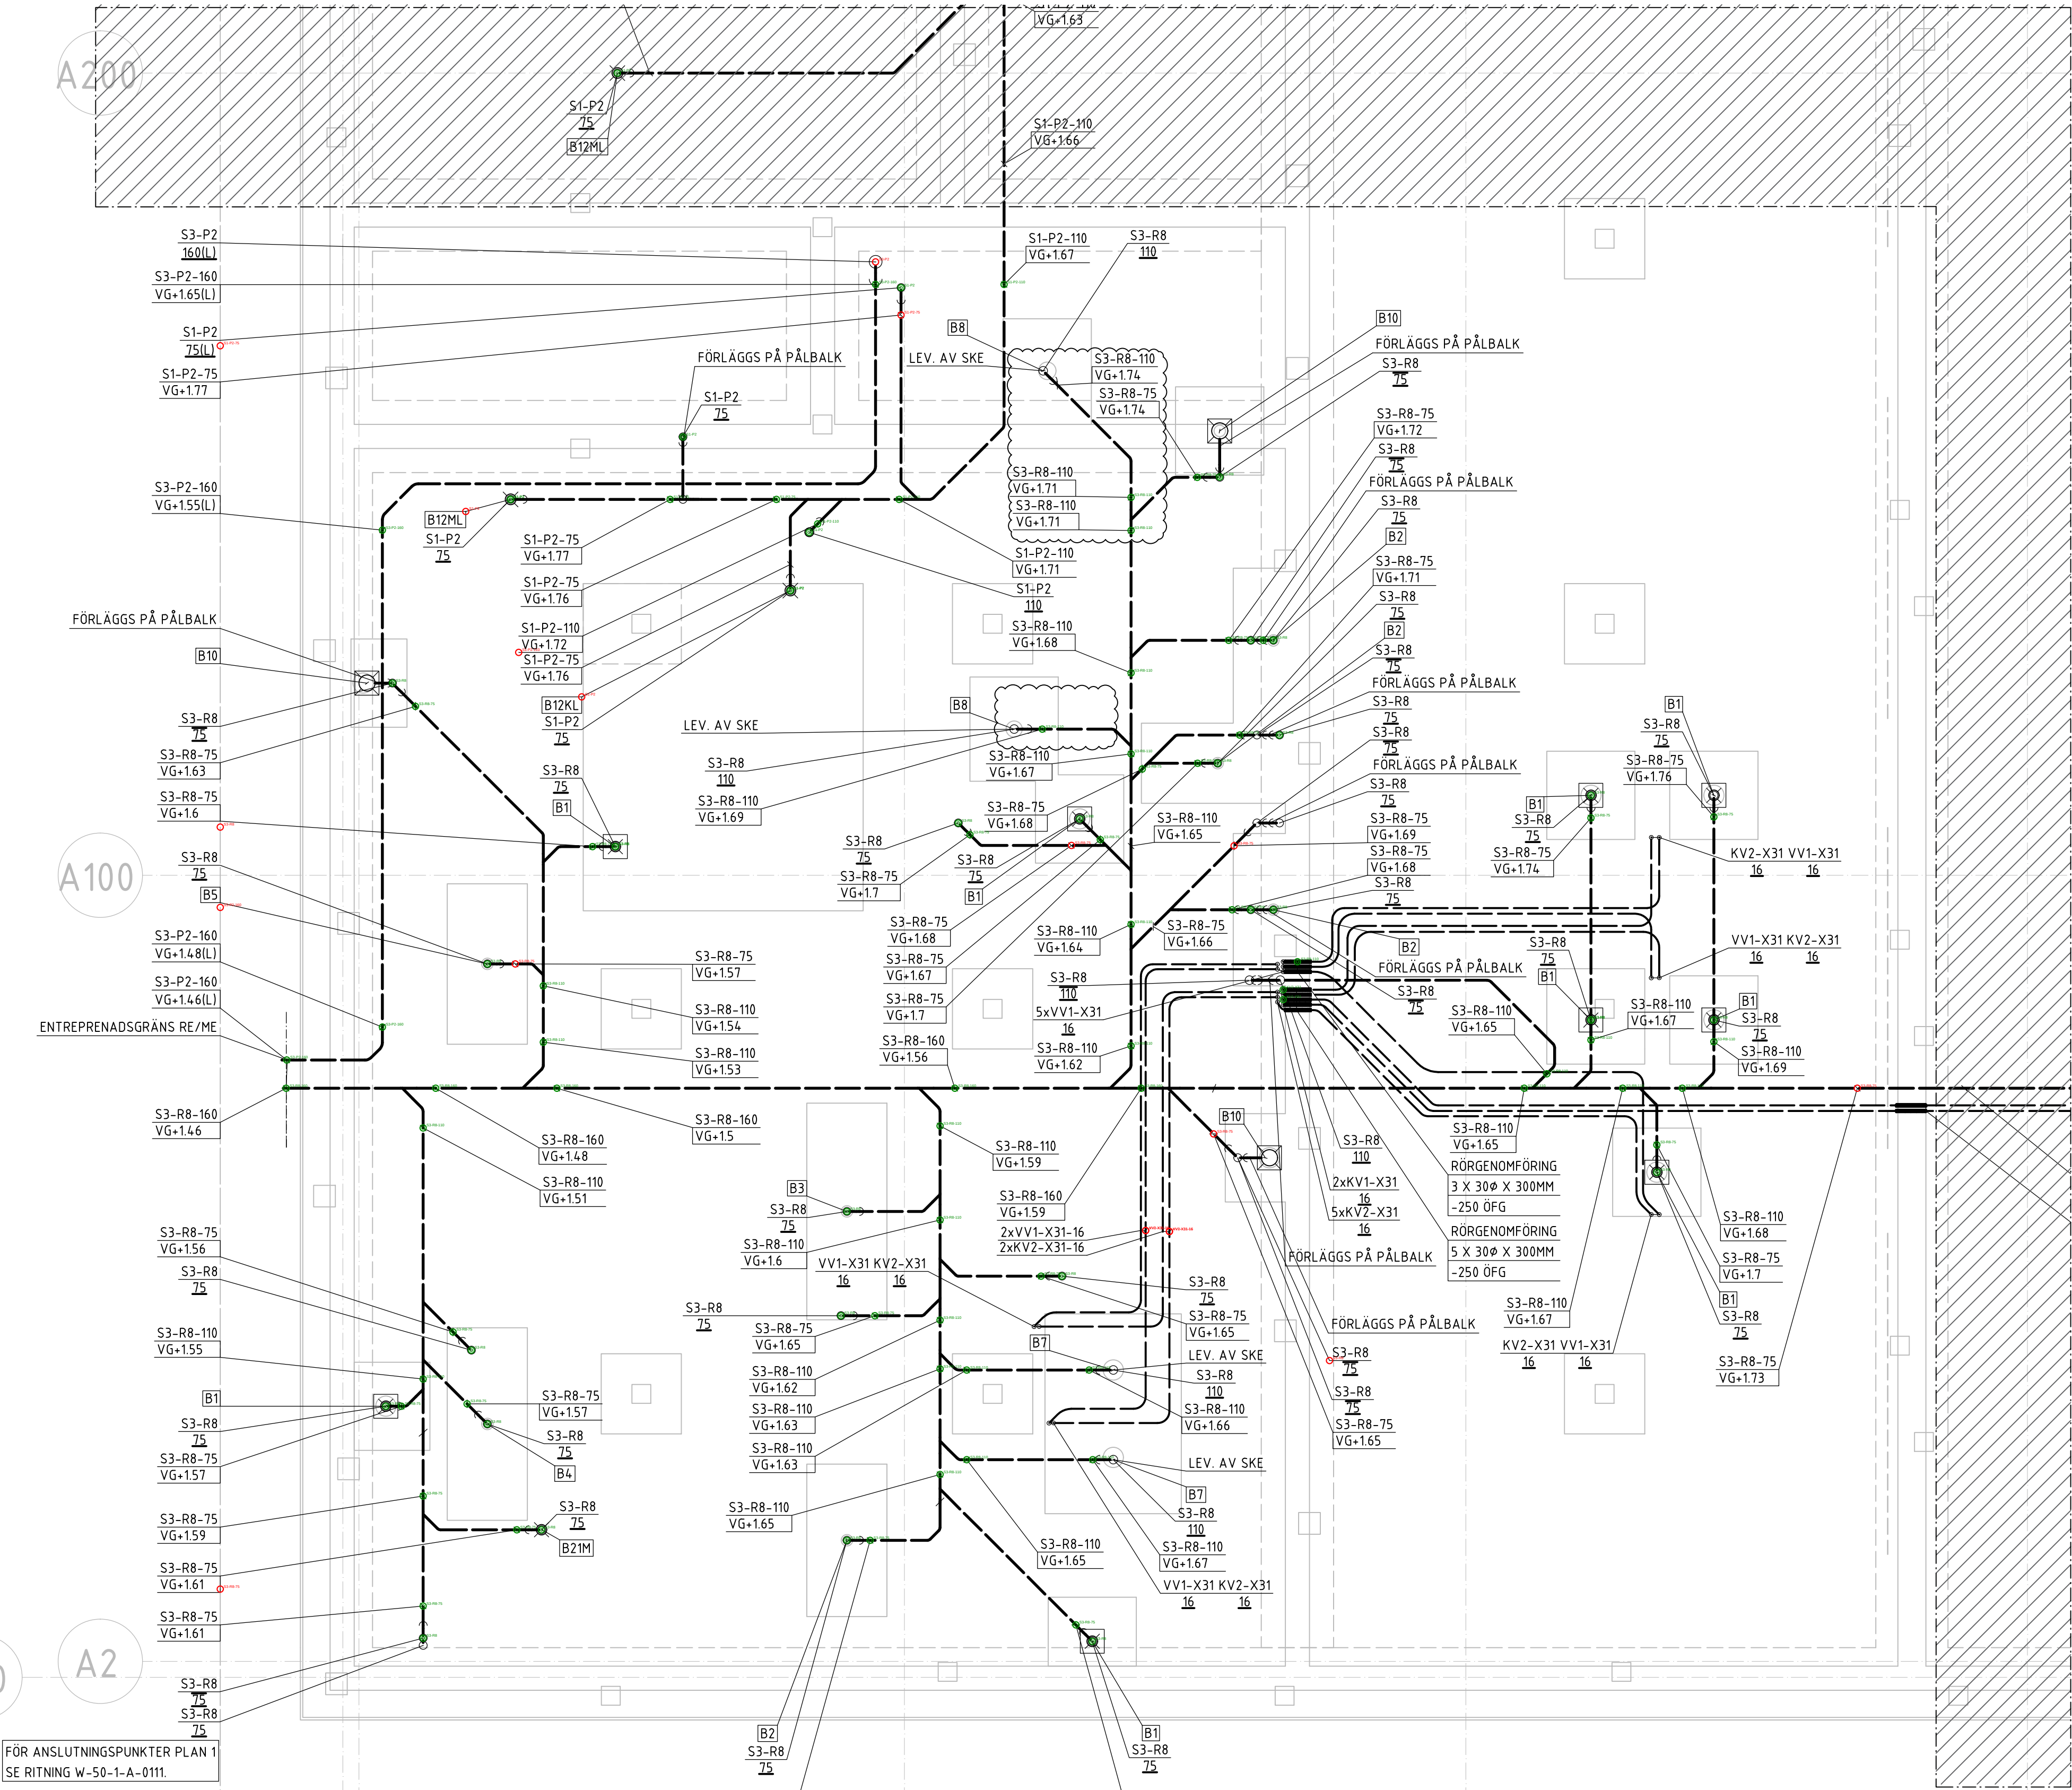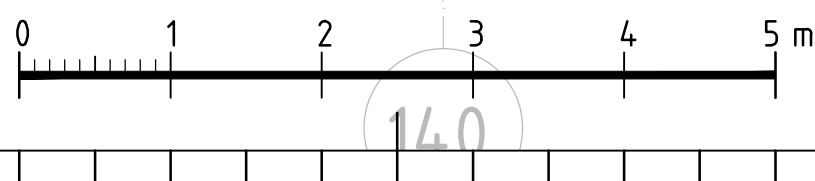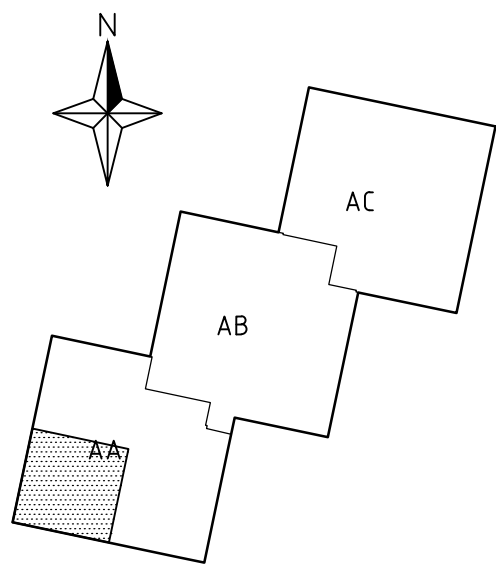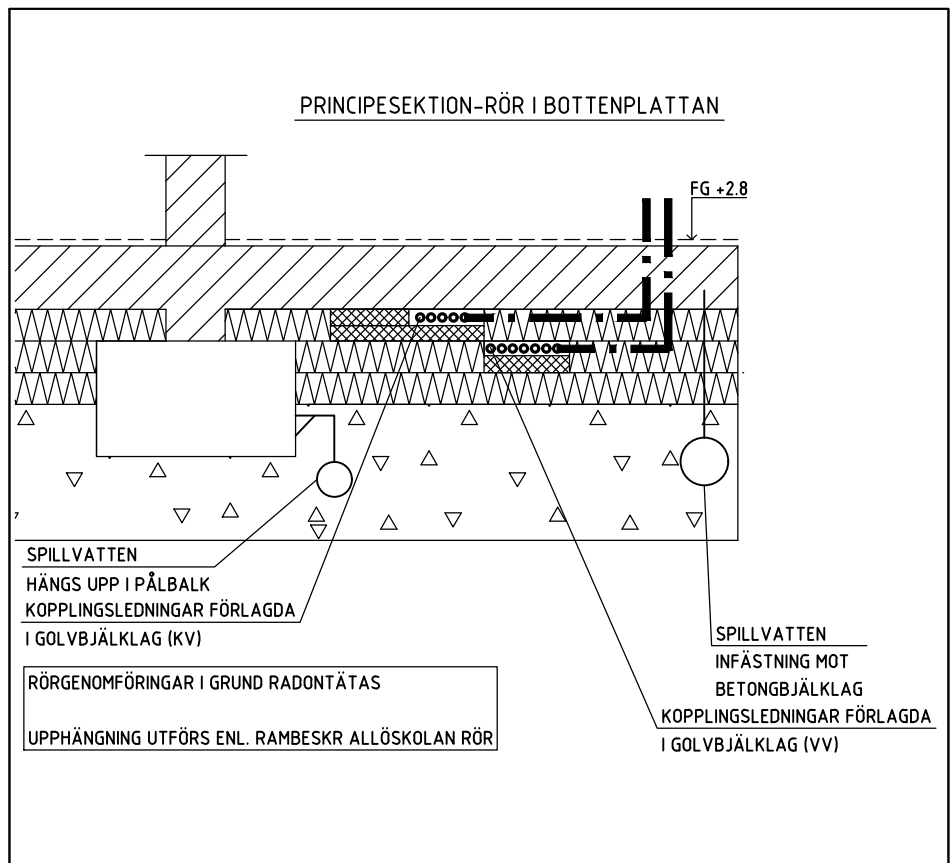

INGÅR I VS
B1-GOLVBRUNN 300x300 (8st)
B2-GOLVRÄNNÄ 1000x150 (4st)
B3-GOLVRÄNNÄ 1900x150 (1st)
B4-GOLVRÄNNÄ 1600x150 (1st)
B5-GOLVRÄNNÄ 1200x150 (1st)
B10-GOLVBRUNN 300x300 (3st)

INGÅR I SKE
B7-GOLVBRUNN 900x600 (2st)
B8-GOLVRÄNNÄ 500x300 (2st)

FÖR ANSLUTNINGSPUNKTER PLAN 1
SE RITNING W-50-1-A-0111.

LAGER