

SYSTEM + LÖPNUMMER
MATERIAL + VARIANTNR
DIMENSION
ISOLERINGSTYP

SYSTEM VÄRME
FJV1 FJÄRRVÄRME

KV1	KALLVATTEN, OAVHÄRDAT, 5 °C
KV2	KALLVATTEN, AVHÄRDAT, 5 °C
VV1	VARMVATTEN, 55°C
VVC1	VARMVATTENCIRKULATION, 50°C

D1	DAGVATTEN, ALLMÄNT I MARK
S1	SPILLVATTEN, ALLMÄNT I MARK
S2	SPILLVATTEN, ALLMÄNT INOMHUS
S3	SPILLVATTEN FRÅN STORKÖK

E13	PEM, TRYCKRÖR
S6	STÅLRÖR, TUBRÖR TRYCKKÄRLSKVALITET, SVETSFÖG
X31	LEDNINGAR AV PEX (PE-XA) MED RIR

E4	PE-RÖR, TRYCKRÖR, PN16
P2	LEDNINGAR AV PP-RÖR, SLÄTA MARKAVLOPPSRÖR I BYGGNAD
R8	LEDNINGAR AV ROSTFRIA RÖR

W	MINERALULL FABRIKSMONTERAD ALU-PLÅT
V	CELLGUMMISLANG
	<u>YTBEKLÄDNAD</u>
B	PLASTPLÅT
C	MÖNSTERPRÄGLAD ALU-PLÅT

ALxxx	AVLUFTARE
Bxxx	GOLVBRUNN
BLxxx	BLANDARE
DBxxx	DISKBÄNKAR
DM	DISKMASKIN
IL	INSPEKTIONSLUCKA (UTFÖRS AV BE)
KM	KOMBI-MASKIN
RLx	RENSRÖR, MED LOCK
SL1	SERVICELUCKA, 150x150, INGÅR I BE
TM	TVÄTTMASKIN
TSxxx	TVÄTTSTALL
VLOxxx	VATTENLÅS
VKxxx	VATTENKLOSETT

ANSL	ANSLUTNING
CL	CENTRUMLINJE
FG	FÄRDIGT GOLV
ÖFG	ÖVER (FÄRDIGT) GOLV
INK	INKOPPLING
UK	UNDERKANT
VG	VATTENGÅNG
(L)	AVLOPPSLUFTARE

FÖLJANDE GÄLLER OM EJ ANNAT ANGES:
DOLDA KV/VV(1-2)-X31



ANSL	KV	VV	S
B	-	-	75
BL	16(15)	16(15)	-
TS	16(12)	16(12)	75
UB	16(12)	16(12)	75
VK	16(12)	-	110

BYGGHANDLING



ALLÖSKOLAN - HUS AA
V5-INSTALLATIONER
RÖR UNDER BOTTENPLATTA- DEL 1

--	--	--

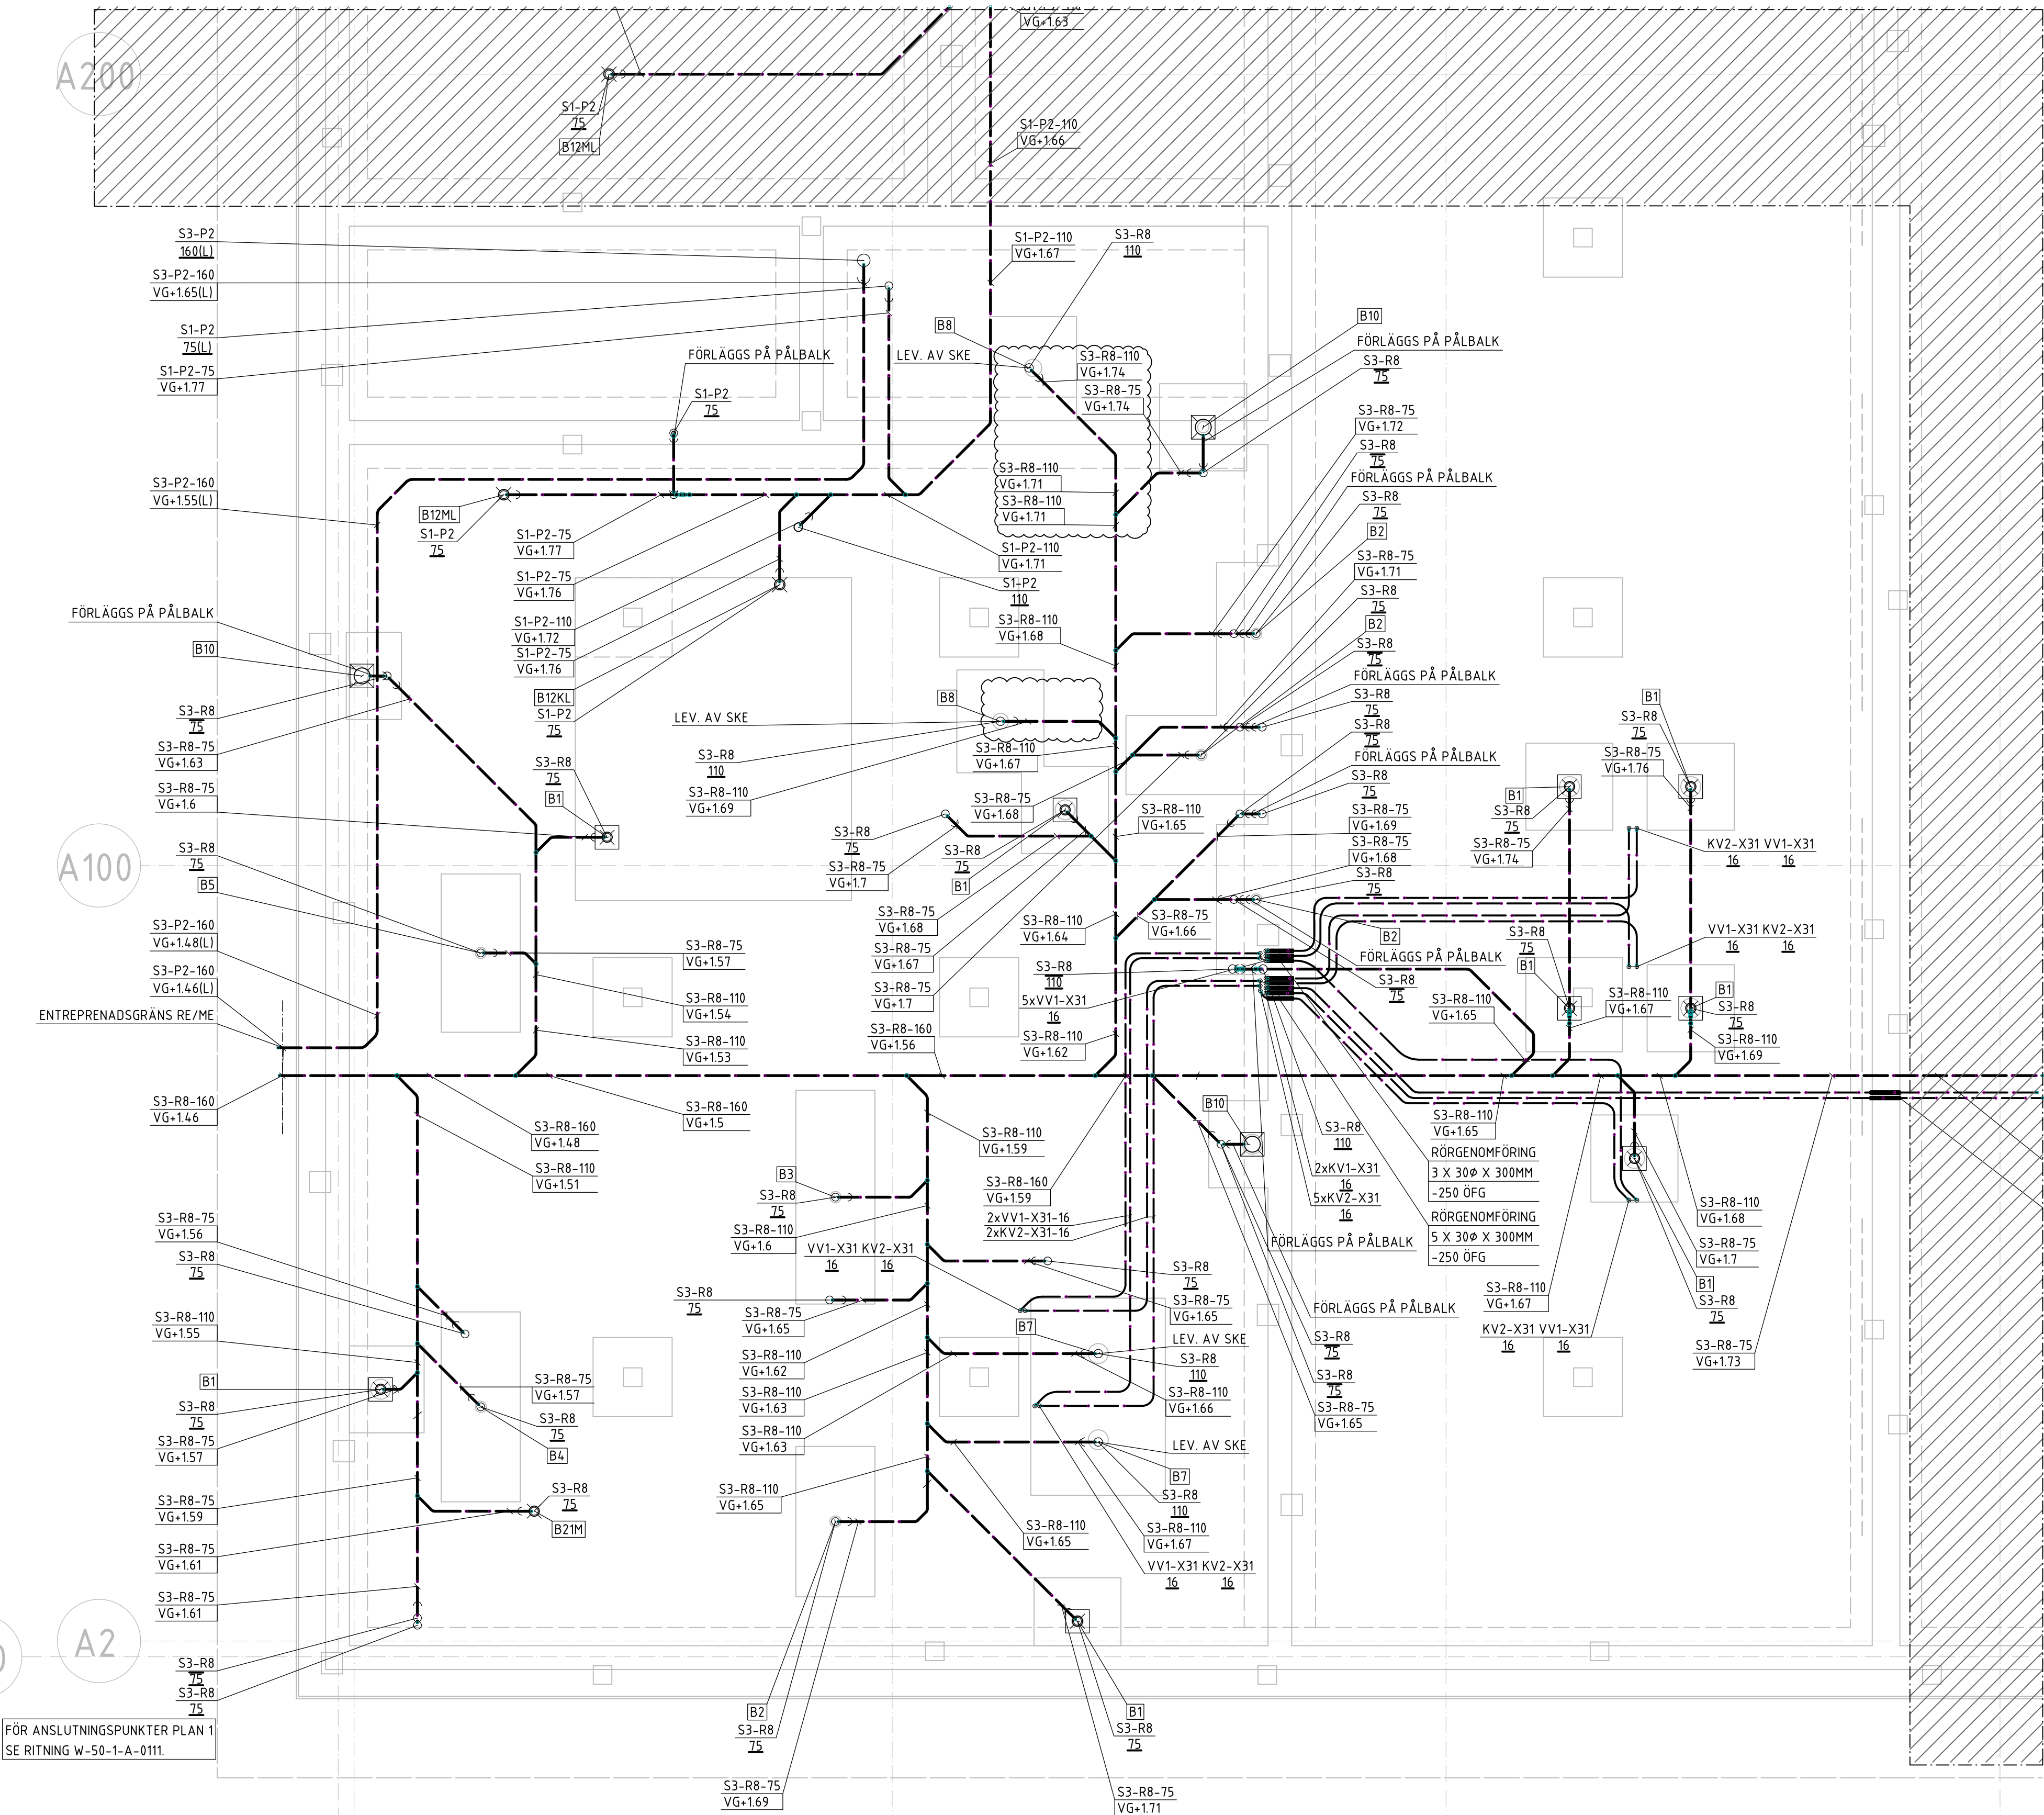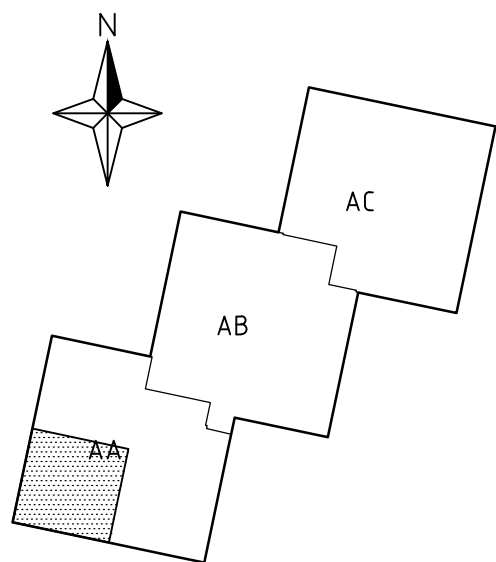

INGÅR I VS
B1-GOLVBRUNN 300x300 (8st)
B2-GOLVRÄNNA 1000x150 (4st)
B3-GOLVRÄNNA 1900x150 (1st)
B4-GOLVRÄNNA 1600x150 (1st)
B5-GOLVRÄNNA 1200x150 (1st)
B10-GOLVBRUNN 300x300 (3st)

INGÅR I SKE
B7-GOLVBRUNN 900x600 (2st)
B8-GOLVRÄNNA 500x300 (2st)

FÖR ANSLUTNINGSPUNKTER PLAN 1
SE RITNING W-50-1-A-0111.

A00

A2

00|

2

70

140

210