

FÖRKLARINGAR

SYSTEM + LÖPNUMMER  
MATERIAL + VARIANTNR  
DIMENSION  
ISOLERINGTYP

XX00-X00-000/X00  
SYSTEM VÄRME  
FJV1 FJÄRRVÄRME  
SYSTEM TAPPVATTEN  
KV1 KALLVATTEN, OAVHÄRDAT, 5 °C  
KV2 KALLVATTEN, AVHÄRDAT, 5 °C  
VV1 VARMVATTEN, 55°C  
VVC1 VARMVATTENCIRKULATION, 50°C

SYSTEM SPILLVATTEN  
D1 DAGVATTEN, ALLMÄNT I MARK  
S1 SPILLVATTEN, ALLMÄNT I MARK  
S2 SPILLVATTEN, ALLMÄNT INOMHUS  
S3 SPILLVATTEN FRÅN STORKÖK

MATERIAL RÖR  
E13 PEM, TRYCKRÖR  
S6 STÅLRÖR, TUBRÖR TRYCKKÄRLSKVALITET, SVETSGOG  
X31 LEDNINGAR AV PEX (PE-XA) MED RIR

MATERIAL SPILLVATTEN  
E4 PE-RÖR, TRYCKRÖR, PN16  
P2 LEDNINGAR AV PP-RÖR, SLÄTA  
MARKAVLOPPSRÖR I BYGGNAD  
R8 LEDNINGAR AV ROSTFRIA RÖR

ISOLERING  
W MINERALULL FABRIKSMONTERAD ALU-PLÅT  
V CELLGUMMISLANG  
YTBEKLÄDNAD  
B PLASTPLÅT  
C MÖNSTERPRÄGLAD ALU-PLÅT

KOMPONENTER  
ALxxx AVLUFTARE  
Bxxx GOLVBRUNN  
BLxxx BLANDARE  
DBxxx DISKBÄNKAR  
DM DISKMASKIN  
IL INSPEKTIONSLUCKA (UTFÖRS AV BE)  
KM KOMBI-MASKIN  
RLx RENSÖR, MED LOCK  
SL1 SERVICELUCKA, 150x150, INGÅR I BE  
TM TVÄTTMASKIN  
TSxxx TVÄTTSTALL  
VLOxxx VATTENLÄS  
VKxxx VATTENKLOSETT

ÖVRIGT  
ANSL ANSLUTNING  
CL CENTRUMLINJE  
FG FÄRDIGT GOLV  
ÖFG ÖVER (FÄRDIGT) GOLV  
INK INKÖPPLING  
UK UNDERKANT  
VG VATTENGÅNG  
(L) AVLOPPSLUFTARE

KOPPLINGSLEDNINGAR  
FÖLJANDE GÄLLER OM EJ ANNAT ANGES:  
DOLDA KV/VV(1-2)-X31  
ANSL KV VV S  
B - - 75  
BL 16(15) 16(15) -  
TS 16(12) 16(12) 75  
UB 16(12) 16(12) 75  
VK 16(12) - 110

|     |           |            |            |
|-----|-----------|------------|------------|
| B   | ENL. PM-2 | 2024-05-07 | A.B.       |
| A   | ENL. PM-1 | 2024-04-19 | A.B.       |
| REV | ÄNDRINGEN | AVSER      | DATUM SIGN |

BYGGHANDLING  
FASTIGHETSBETECKNING  
OSTRA KASERN 3







Kristianstads kommun

Västra Storgatan 12  
291 80 KRISTIANSTAD  
Telefon: 044-13 50 00

|            |                 |                  |
|------------|-----------------|------------------|
| A          |                 |                  |
| K          |                 |                  |
| V          |                 |                  |
| E          |                 |                  |
| X          | L VINNERS AB    | +46 101 02 44 00 |
| B          |                 |                  |
| SK         |                 |                  |
| ANSVARIG   | RITAD/KONSTR AV | HANDLGGARE       |
| L.F.       | A.B.            | L.F.             |
| PROJEKT NR | DATUM           | REV.DATUM        |
| 2029304    | 2024-03-01      | 2024-05-07       |
| OBJEKTID   | HUS             | VARNING          |
| 268140     | AA              | 01               |
|            |                 | DISCIPLIN        |
|            |                 | W                |

ALLÖSKOLAN - HUS AA  
VS-INSTALLATIONER  
RÖR UNDER BOTTENPLATTA- DEL 1  
FORMAT

|                               |                                |          |
|-------------------------------|--------------------------------|----------|
| SKALA A1 (A3)<br>1:50 (1:100) | RITINGSNUMMER<br>W-50-1-A-0011 | BET<br>B |
|-------------------------------|--------------------------------|----------|

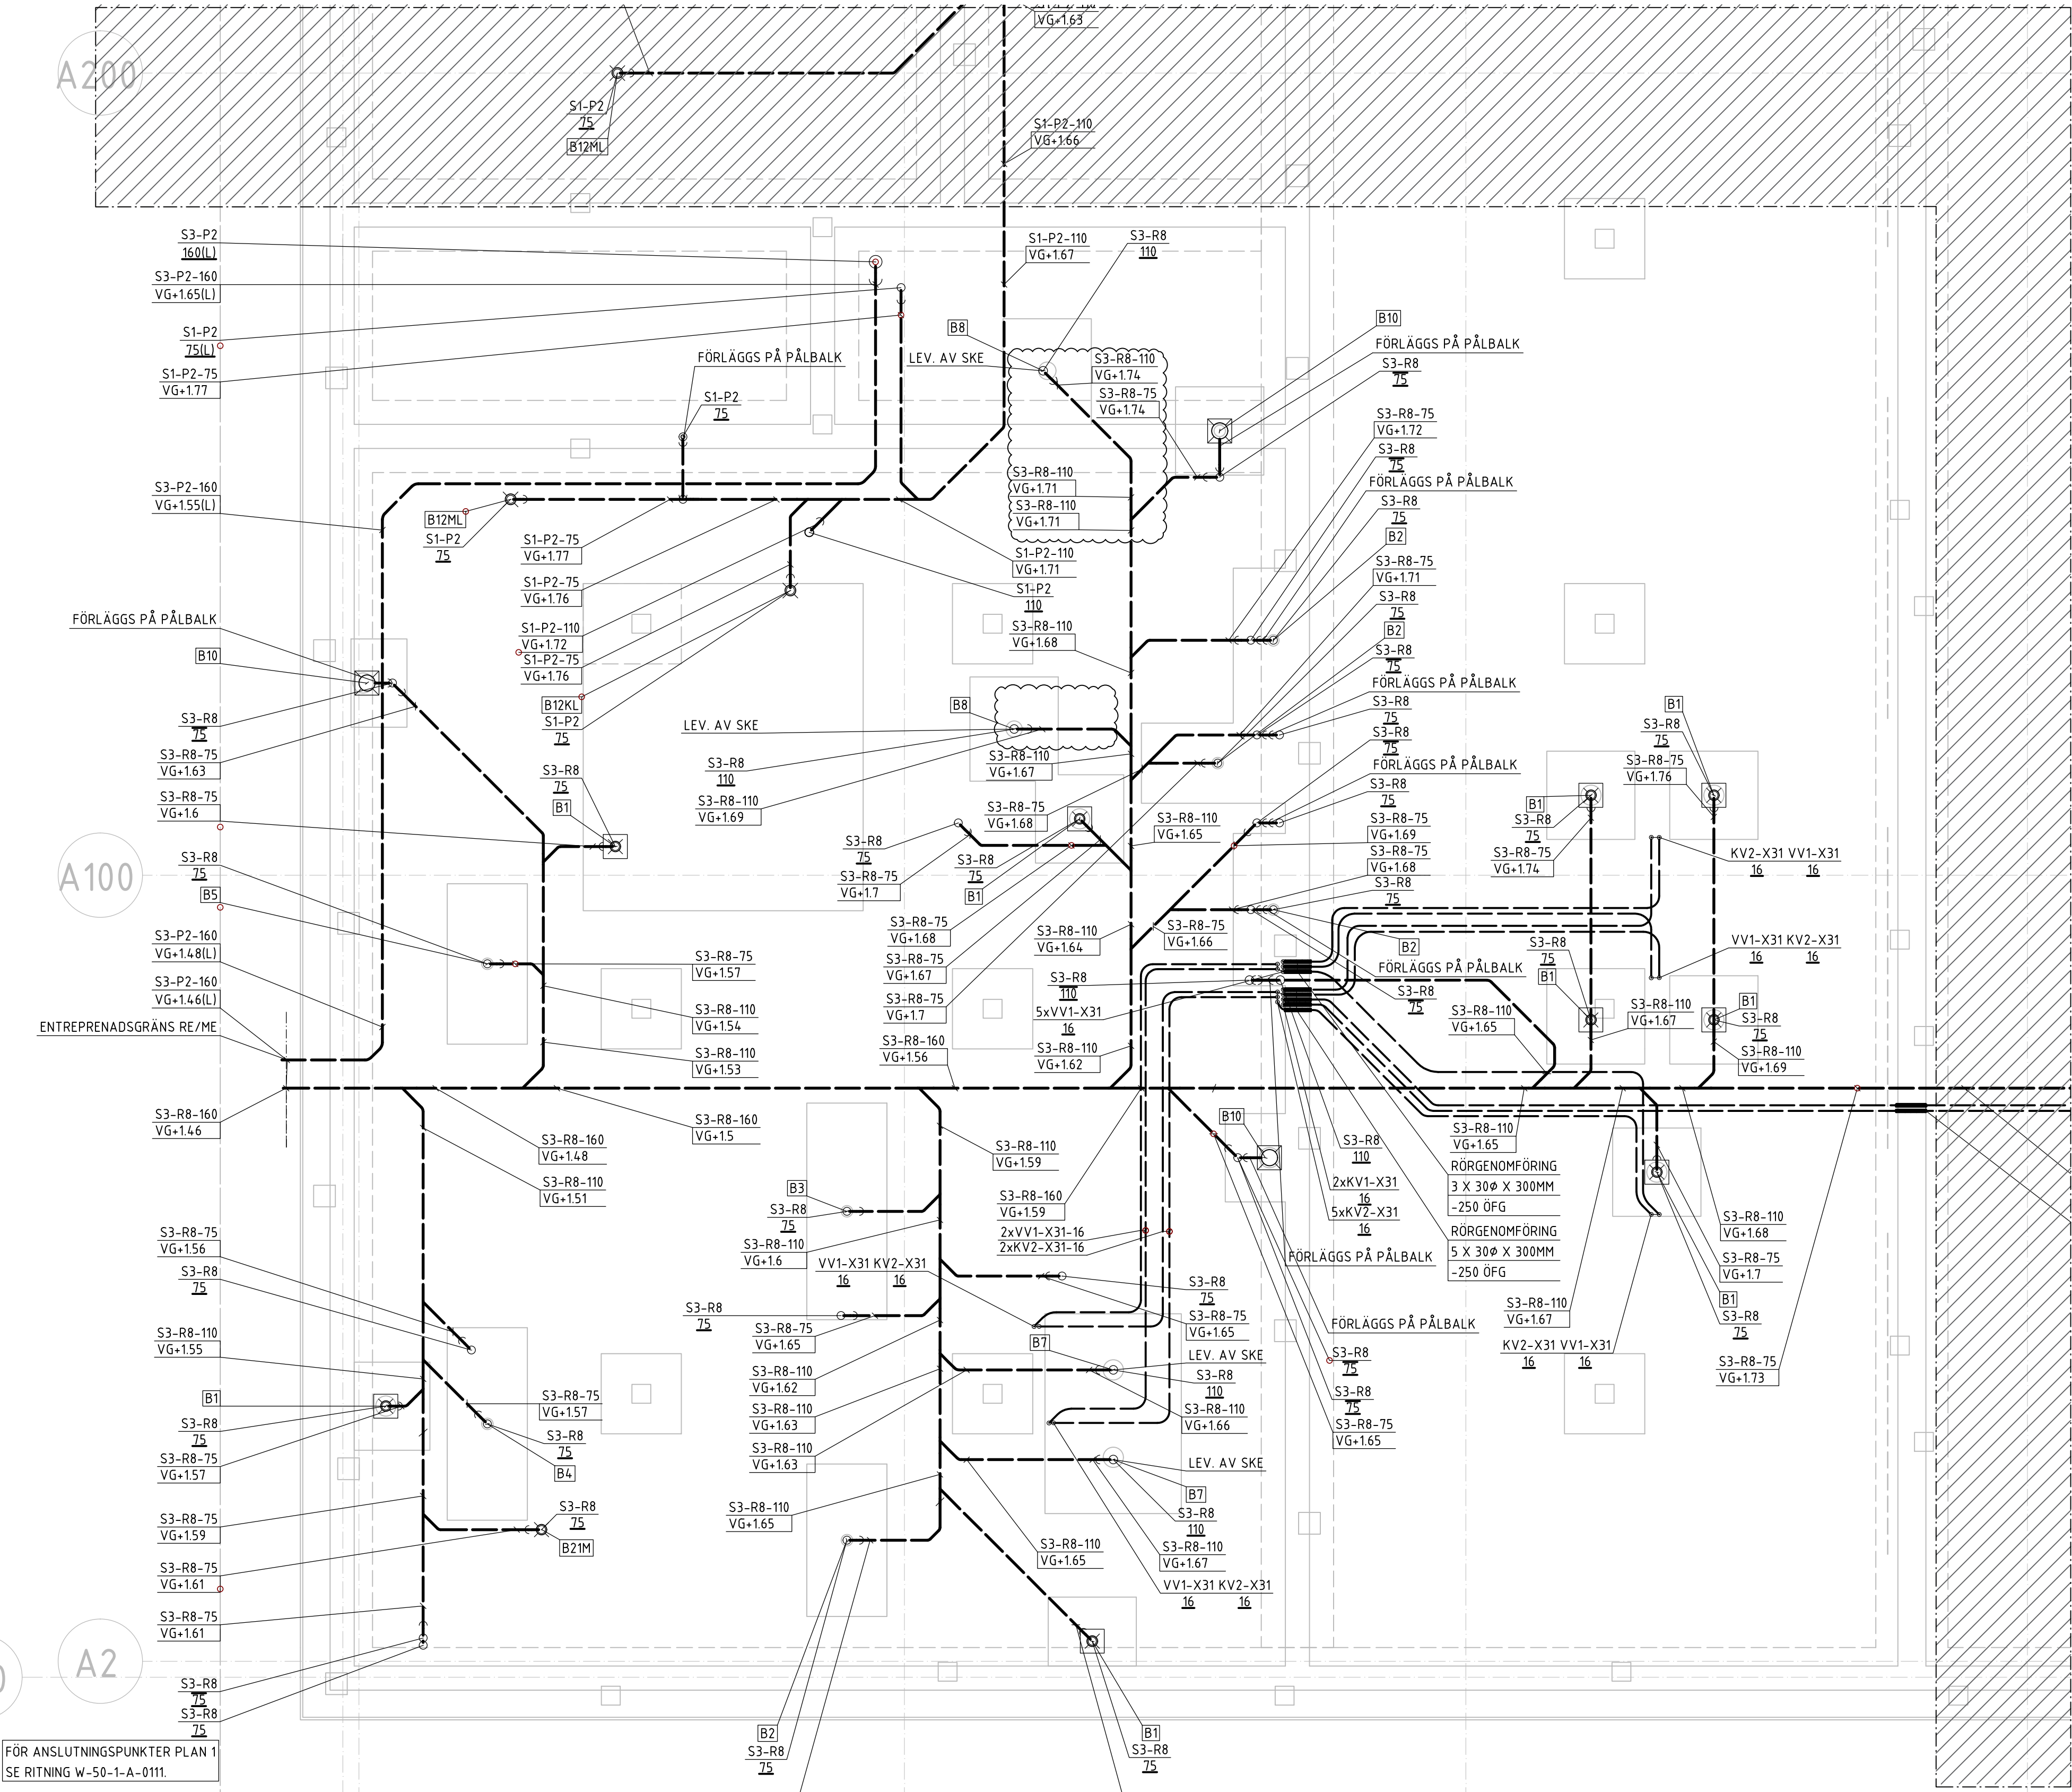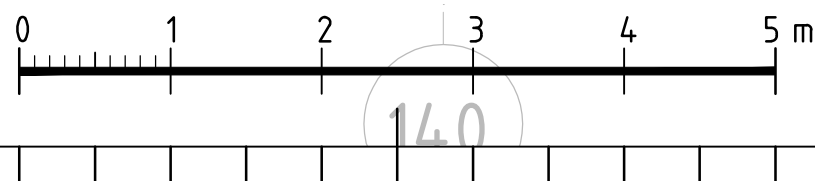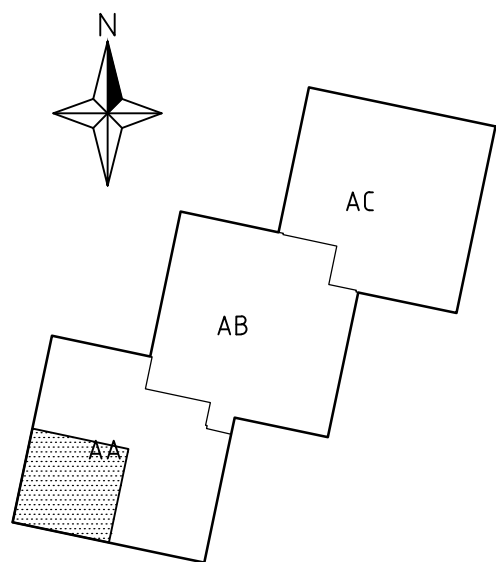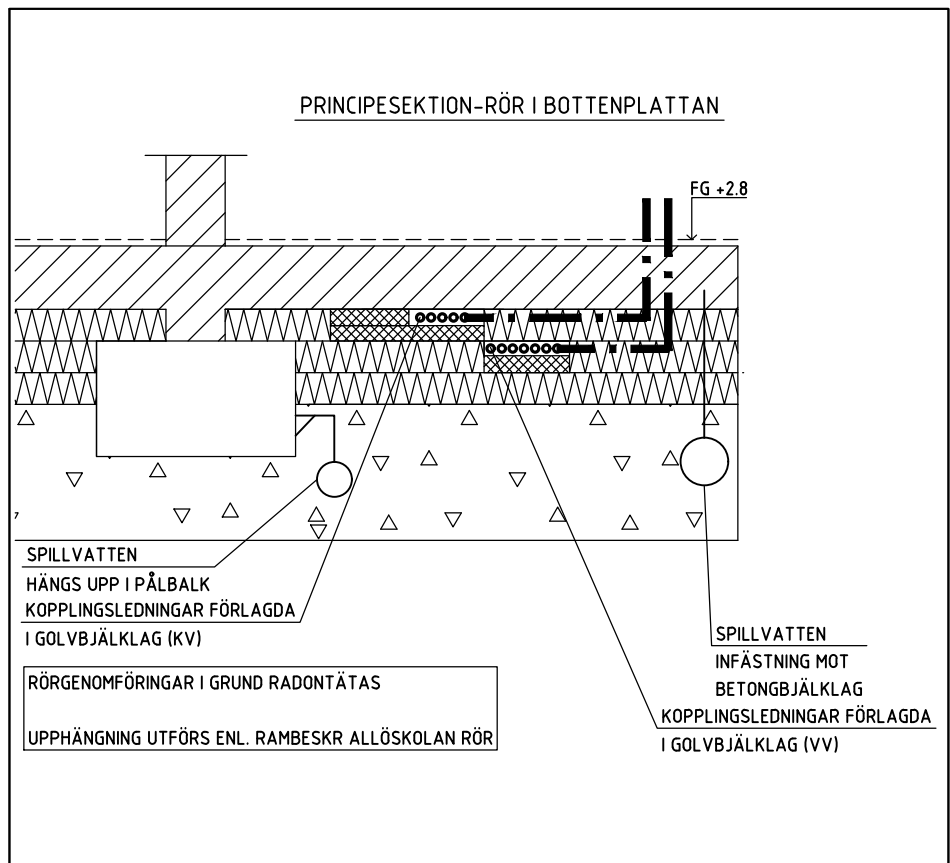

INGÅR I VS  
B1-GOLVBRUNN 300x300 (8st)  
B2-GOLVRÄNNA 1000x150 (4st)  
B3-GOLVRÄNNA 1900x150 (1st)  
B4-GOLVRÄNNA 1600x150 (1st)  
B5-GOLVRÄNNA 1200x150 (1st)  
B10-GOLVBRUNN 300x300 (3st)

INGÅR I SKE  
B7-GOLVBRUNN 900x600 (2st)  
B8-GOLVRÄNNA 500x300 (2st)

FÖR ANSLUTNINGSPUNKTER PLAN 1  
SE RITNING W-50-1-A-0111.