


XREF: .\\1\\SV\\SK-modell\\SK-16-P-0100-1764-A.dwg  
.\\1\\A\\A-modell\\A-10-P-0100-1764-A.dwg  
.\\1\\A\\A-modell\\orienteringsfig.dwg  
.\\1\\A\\A-modell\\orienteringsfig.dwg  
.\\1\\A\\A-modell\\orienteringsfig.dwg

LAGER: SB11

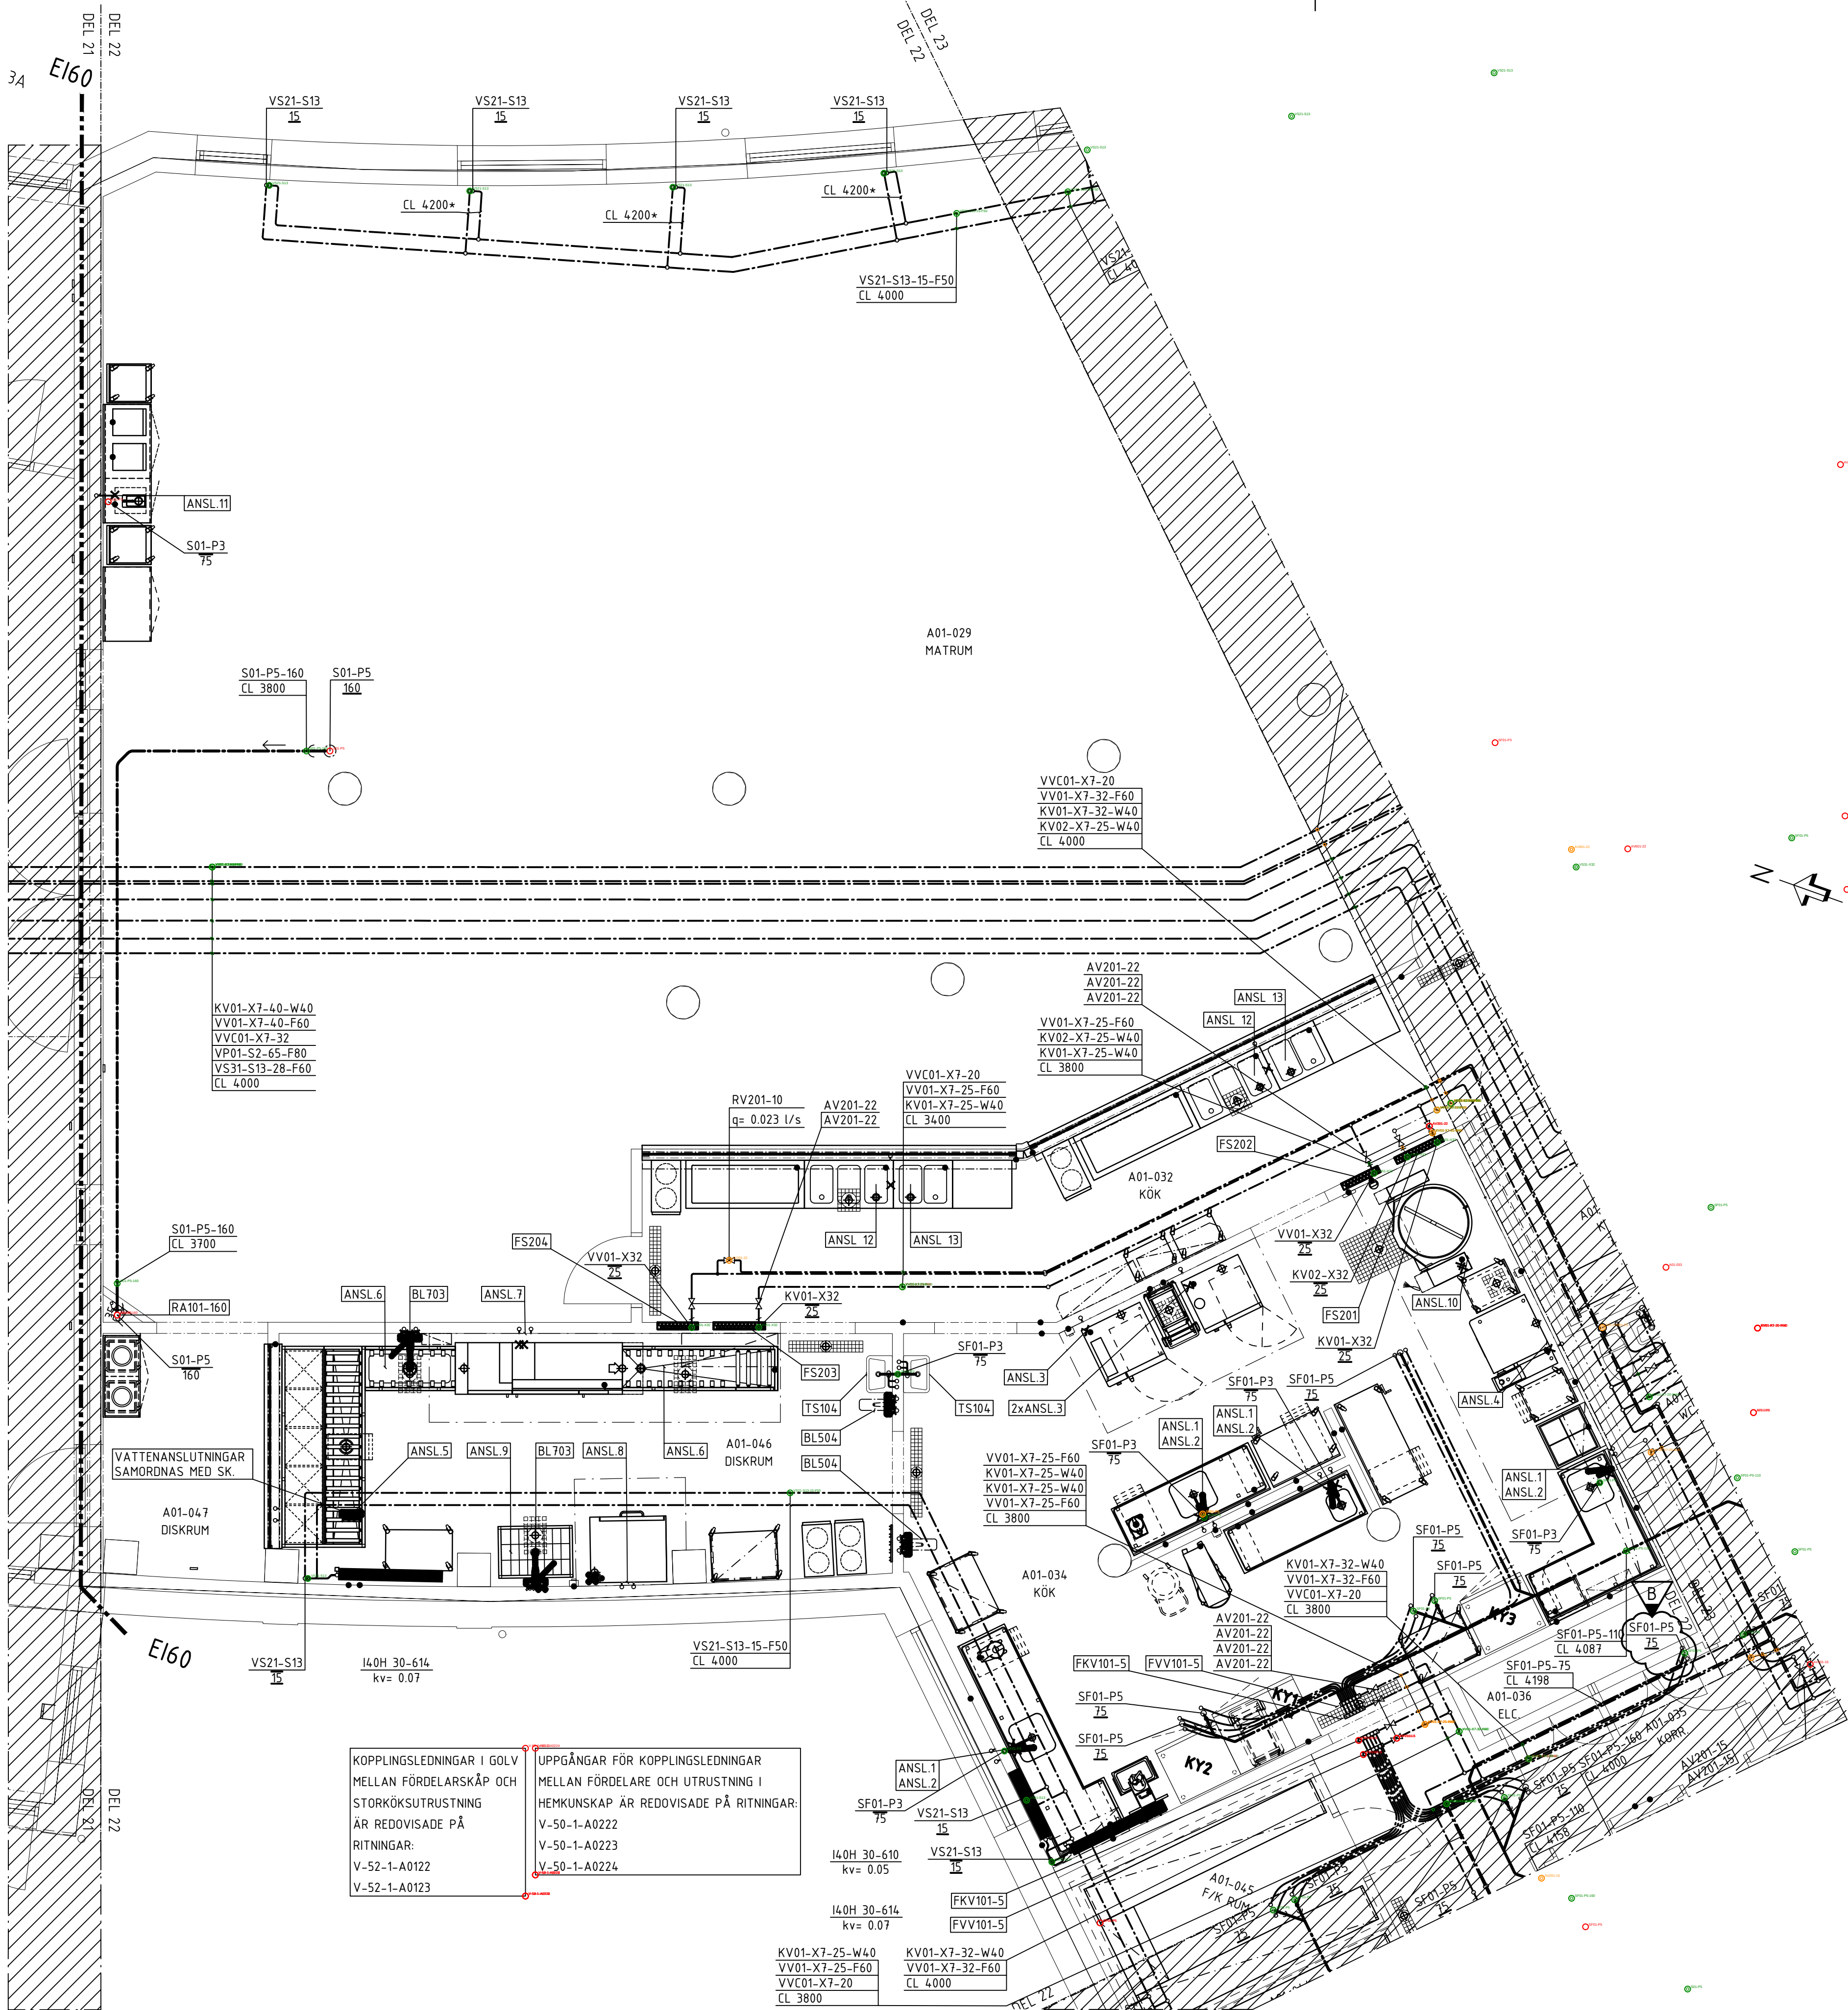

FÖRKLARINGAR  
BETECKNING RÖRSYSTEM  
VS11-S13-42-F100 - (100) mm  
(L-F) Ev. isolering.  
(42) Dimension  
(S13) Rörmaterial  
(11) Systemnummer  
(VS) Systembeteckning

TAPPVATTENSYSTEM  
KV01 Tappkallvatten  
KV02 Tappkallvatten, kombiugn  
VV01 Tappvarmvatten  
VVC01 Varmvattencirkulation

SPILLVATTENSYSTEM  
S01 Spillvatten  
SF01 Spillvatten, fettavskiljare

S01 Fall min: 1‰  
SF01 Fall min: 2‰

VÄRMEVATTENSYSTEM  
FJV01 Fjärrvärme  
VP01 Värmebärare, primär  
VS11 Värmebärare, sekundär, ventilation  
VS21 Värmebärare, sekundär, radiatorer  
VS31 Värmebärare, sekundär, golvvärme

RÖRLEDNINGAR  
G3 MA-rör  
K5 Kopparrör Frkr  
P2 PP markavloppsror  
P3 PP-rör (avlopp inomhus)  
P5 PP-rör (avlopp inomhus luddämpat)  
R2 Ledningar av syrafast stål  
R10 Rostfritt avloppsror, muff  
S2 Handelstub, stål  
S6 Tryckkärlsstål  
S13 Presskopplingsrör utv förs  
X7 PAL-RÖR  
X31 PEX-Rör  
X32 PEX-Rör, extraisolerade

ISOLERING AV INSTALLATIONER  
-F Mineralull  
-W Mineralull, diffusionstät

VV01 & VVC01 SAMISOLERAS

SAKVAROR  
Enl. BESKRIVNING AVSEENDE  
VÄRME- OCH SANITÄTSANLÄGGNING  
HANDLINGSNUMMER 11.A.2.1

MÄRKNING AV STYRKOMPONENTER  
Föregås av 1764-A-

ÖVRIGT  
CL xxxx\* = Samma rördimension som  
stick och isolering F50

KOPPLINGSLEDNINGAR  
FRÅN FÖRDELARE TILL  
APPARAT ENLIGT TABELL  
OM INGET ANNAT ANGES

|          |          |
|----------|----------|
| VV01-X31 | KV01-X31 |
| BL       | 16       |
| TS       | 16       |
| UB       | 16       |
| VK       | 16       |

|     |     |                 |        |            |
|-----|-----|-----------------|--------|------------|
| B   | 1   | PM5-W           | 231113 | K. PERSSON |
| A   | 0   | PM1-W           | 230601 | K. PERSSON |
| BET | ANT | ÄNDRINGEN AVSER | DATUM  | SEN        |

## BYGGHANDLING



HYLLIE NYA HÖGSTADIUM OCH SPORTHALL 3  
NYBYGGNAD AV SKOLA OCH SPORTHALL 5800



|                |                  |            |                |
|----------------|------------------|------------|----------------|
| FÖRETAG        | SWECO SVERIGE AB | TEL        | 040 - 16 70 00 |
| UPPDRAGSNUMMER | 30025113         | RITAD AV   | K. PERSSON     |
| DATUM          | 2023-01-31       | HANDLAGARE | D. HAGSTRÖM    |
|                |                  | REVISOR    | J. ÅKESSON     |

|               |               |      |     |            |           |
|---------------|---------------|------|-----|------------|-----------|
| OBJEKTSNUMMER | BYGGNAD       | PLAN | DEL | UNDERGRUPP | DISCIPLIN |
| 1764          | A             | 01   | 22  | 50         | W         |
| SKALA         | RITINGSNUMMER | BET  |     |            |           |
| 1:50          | V-50-1-A0122  | B    |     |            |           |

SKALA 1:50 (A1) 0 1 2 3 4 5