


XREF: .\1\SVK\SK-model\SK-46-P-0100-1764-A.dwg  
.\1\A\A-model\A-40-P-0100-1764-A.dwg  
.\1\A\A-model\orient\orient.dwg  
.\1\A\A-model\orient\orient.dwg  
.\1\A\A-model\orient\orient.dwg

LAGER: SB11

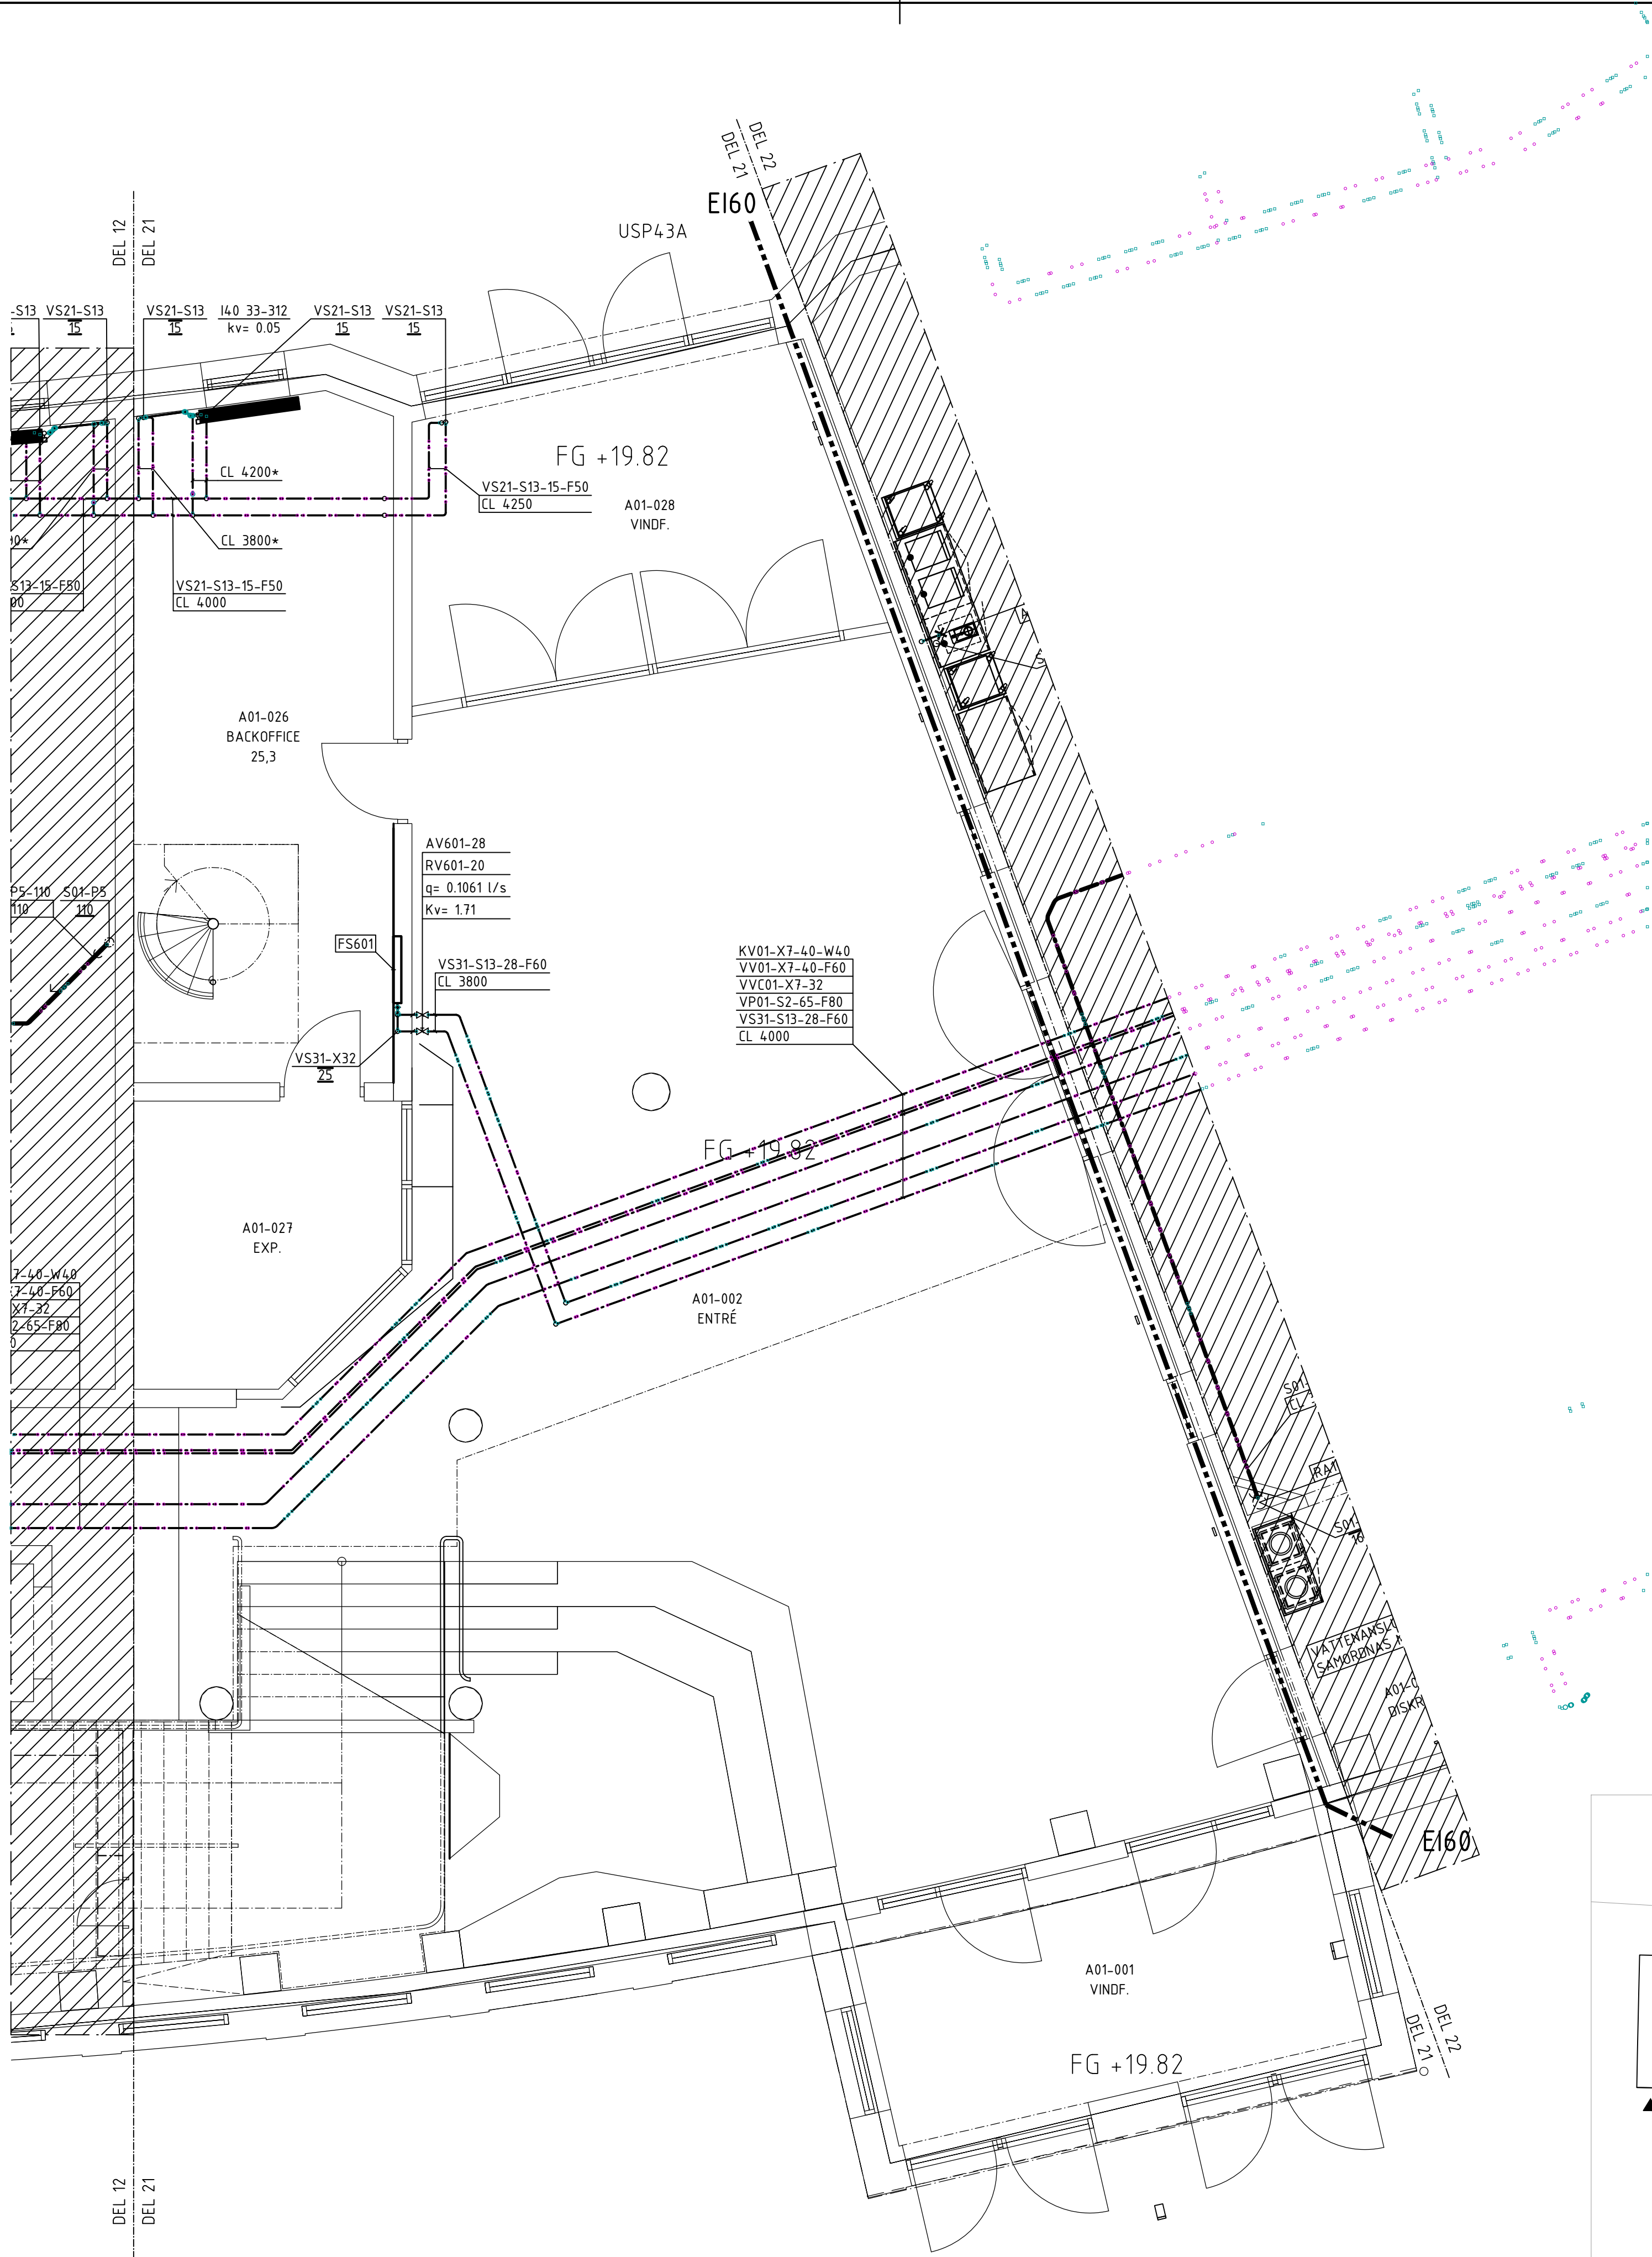

FÖRKLARINGAR

BETECKNING RÖRSYSTEM

VS11-S13-42-F100 - (100) mm (L-F) Ev. isolering. (42) Dimension (S13) Rörmaterial (11) Systemnummer (VS) Systembeteckning

TAPPVATTENSYSTEM

KV01 Tappkallvatten

KV02 Tappkallvatten, kombiugnar

VV01 Tappvarmvatten

VVC01 Varmvattencirkulation

SPILLVATTENSYSTEM

S01 Spillvatten

SF01 Spillvatten, fettavskiljare

S01 Fall min: 1%

SF01 Fall min: 2%

VÄRMEVATTENSYSTEM

FJV01 Fjärrvärme

VP01 Värmebärare, primär

VS11 Värmebärare, sekundär, ventilation

VS21 Värmebärare, sekundär, radiatorer

VS31 Värmebärare, sekundär, golvvärme

RÖRLEDNINGAR

G3 MA-rör

K5 Kopparrör.Frkr

P2 PP markavloppsror

P3 PP-rör (avlopp inomhus)

P5 PP-rör (avlopp inomhus (juddäpat))

R2 Ledningar av syrafäst stål

R10 Rostfritt avloppsror, muff

S2 Handelsstub, stål

S6 Tryckkärlsstål

S13 Presskopplingsrör utv förs

X7 PAL-RÖR

X31 PEX-RIR

X32 PEX-RIR, extraisolerade

ISOLERING AV INSTALLATIONER

-F Mineralull

-W Mineralull, diffusionstät

VV01 & VVC01 SAMISOLERAS

SAKVAROR

Enl. BESKRIVNING AVSEENDE

VÄRME- OCH SANITETSANLÄGGNING

HANDLINGSNUMMER 11.A.2.1

MÄRKNING AV STYRKOMPONENTER

Föregås av 1764-A-

ÖVRIGT

CL xxxx\* = Samma rördimension som stück och isolering F50

KOPPLINGSLEDNINGAR

FRÅN FÖRDELARE TILL APPARAT ENLIGT TABELL OM INGET ANNAT ANGES

| VV01-X31 |    | KV01-X31 |    |
|----------|----|----------|----|
| BL       | 16 | 16       | 16 |
| TS       | 16 | 16       | 16 |
| UB       | 16 | 16       | 16 |
| VK       | 16 | 16       | 16 |

|                                                                                       |               |                                |                         |                      |
|---------------------------------------------------------------------------------------|---------------|--------------------------------|-------------------------|----------------------|
| A                                                                                     | O             | PM1-W                          | 230601                  | K. PERSSON           |
| BET                                                                                   | ANT           | ÄNDRINGEN AVSER                | DATUM                   | SEN                  |
| BYGGHANDLING                                                                          |               |                                |                         |                      |
|  |               | Malmö stad<br>Stadsfastigheter |                         |                      |
| HYLLIE NYA HÖGSTADIUM OCH SPORTHALL 3 PROJEKT NR 30025113                             |               |                                |                         |                      |
| NYBYGGNAD AV SKOLA OCH SPORTHALL 5800                                                 |               |                                |                         |                      |
|  |               |                                |                         |                      |
| Sweco Sverige AB - Tele: 08-695 60 00 - www.sweco.se                                  |               |                                |                         |                      |
| FÖRETAG SWECO SVERIGE AB                                                              |               |                                | TEL                     | 040 - 16 70 00       |
| UPPDRAGSNUMMER 30025113                                                               |               | RITAD AV K. PERSSON            | HANDLAGGARE D. HAGSTRÖM |                      |
| DATUM 2023-01-31                                                                      |               | REV. DATUM 2023-06-01          | ANSVARIG J. ÅKESSON     |                      |
| RUNDSTICKAN 1<br>RÖRINSTALLATIONER<br>HUS A PLAN 1 DEL 21                             |               |                                |                         |                      |
| OBJEKTSNUMMER                                                                         | BYGGNAD       | PLAN                           | DEL                     | UNDERGRUPP DISCIPLIN |
| 1764                                                                                  | A             | 01                             | 21                      | 50 W                 |
| SKALA                                                                                 | RITINGSNUMMER |                                |                         | BET                  |
| 1:50                                                                                  | V-50-1-A0121  |                                |                         | A                    |

SKALA 1:50 (A1) 0 1 2 3 4 5

\\SELUF5002\PROJEKT\23332\30025113\_HYLLIE\_NYA\_HOGSTADIUMSKOLA\000\0 CAD\WMV-MODELLV-50-P-0100-1764-A.DWG PERSSON, KRISTOFFER