


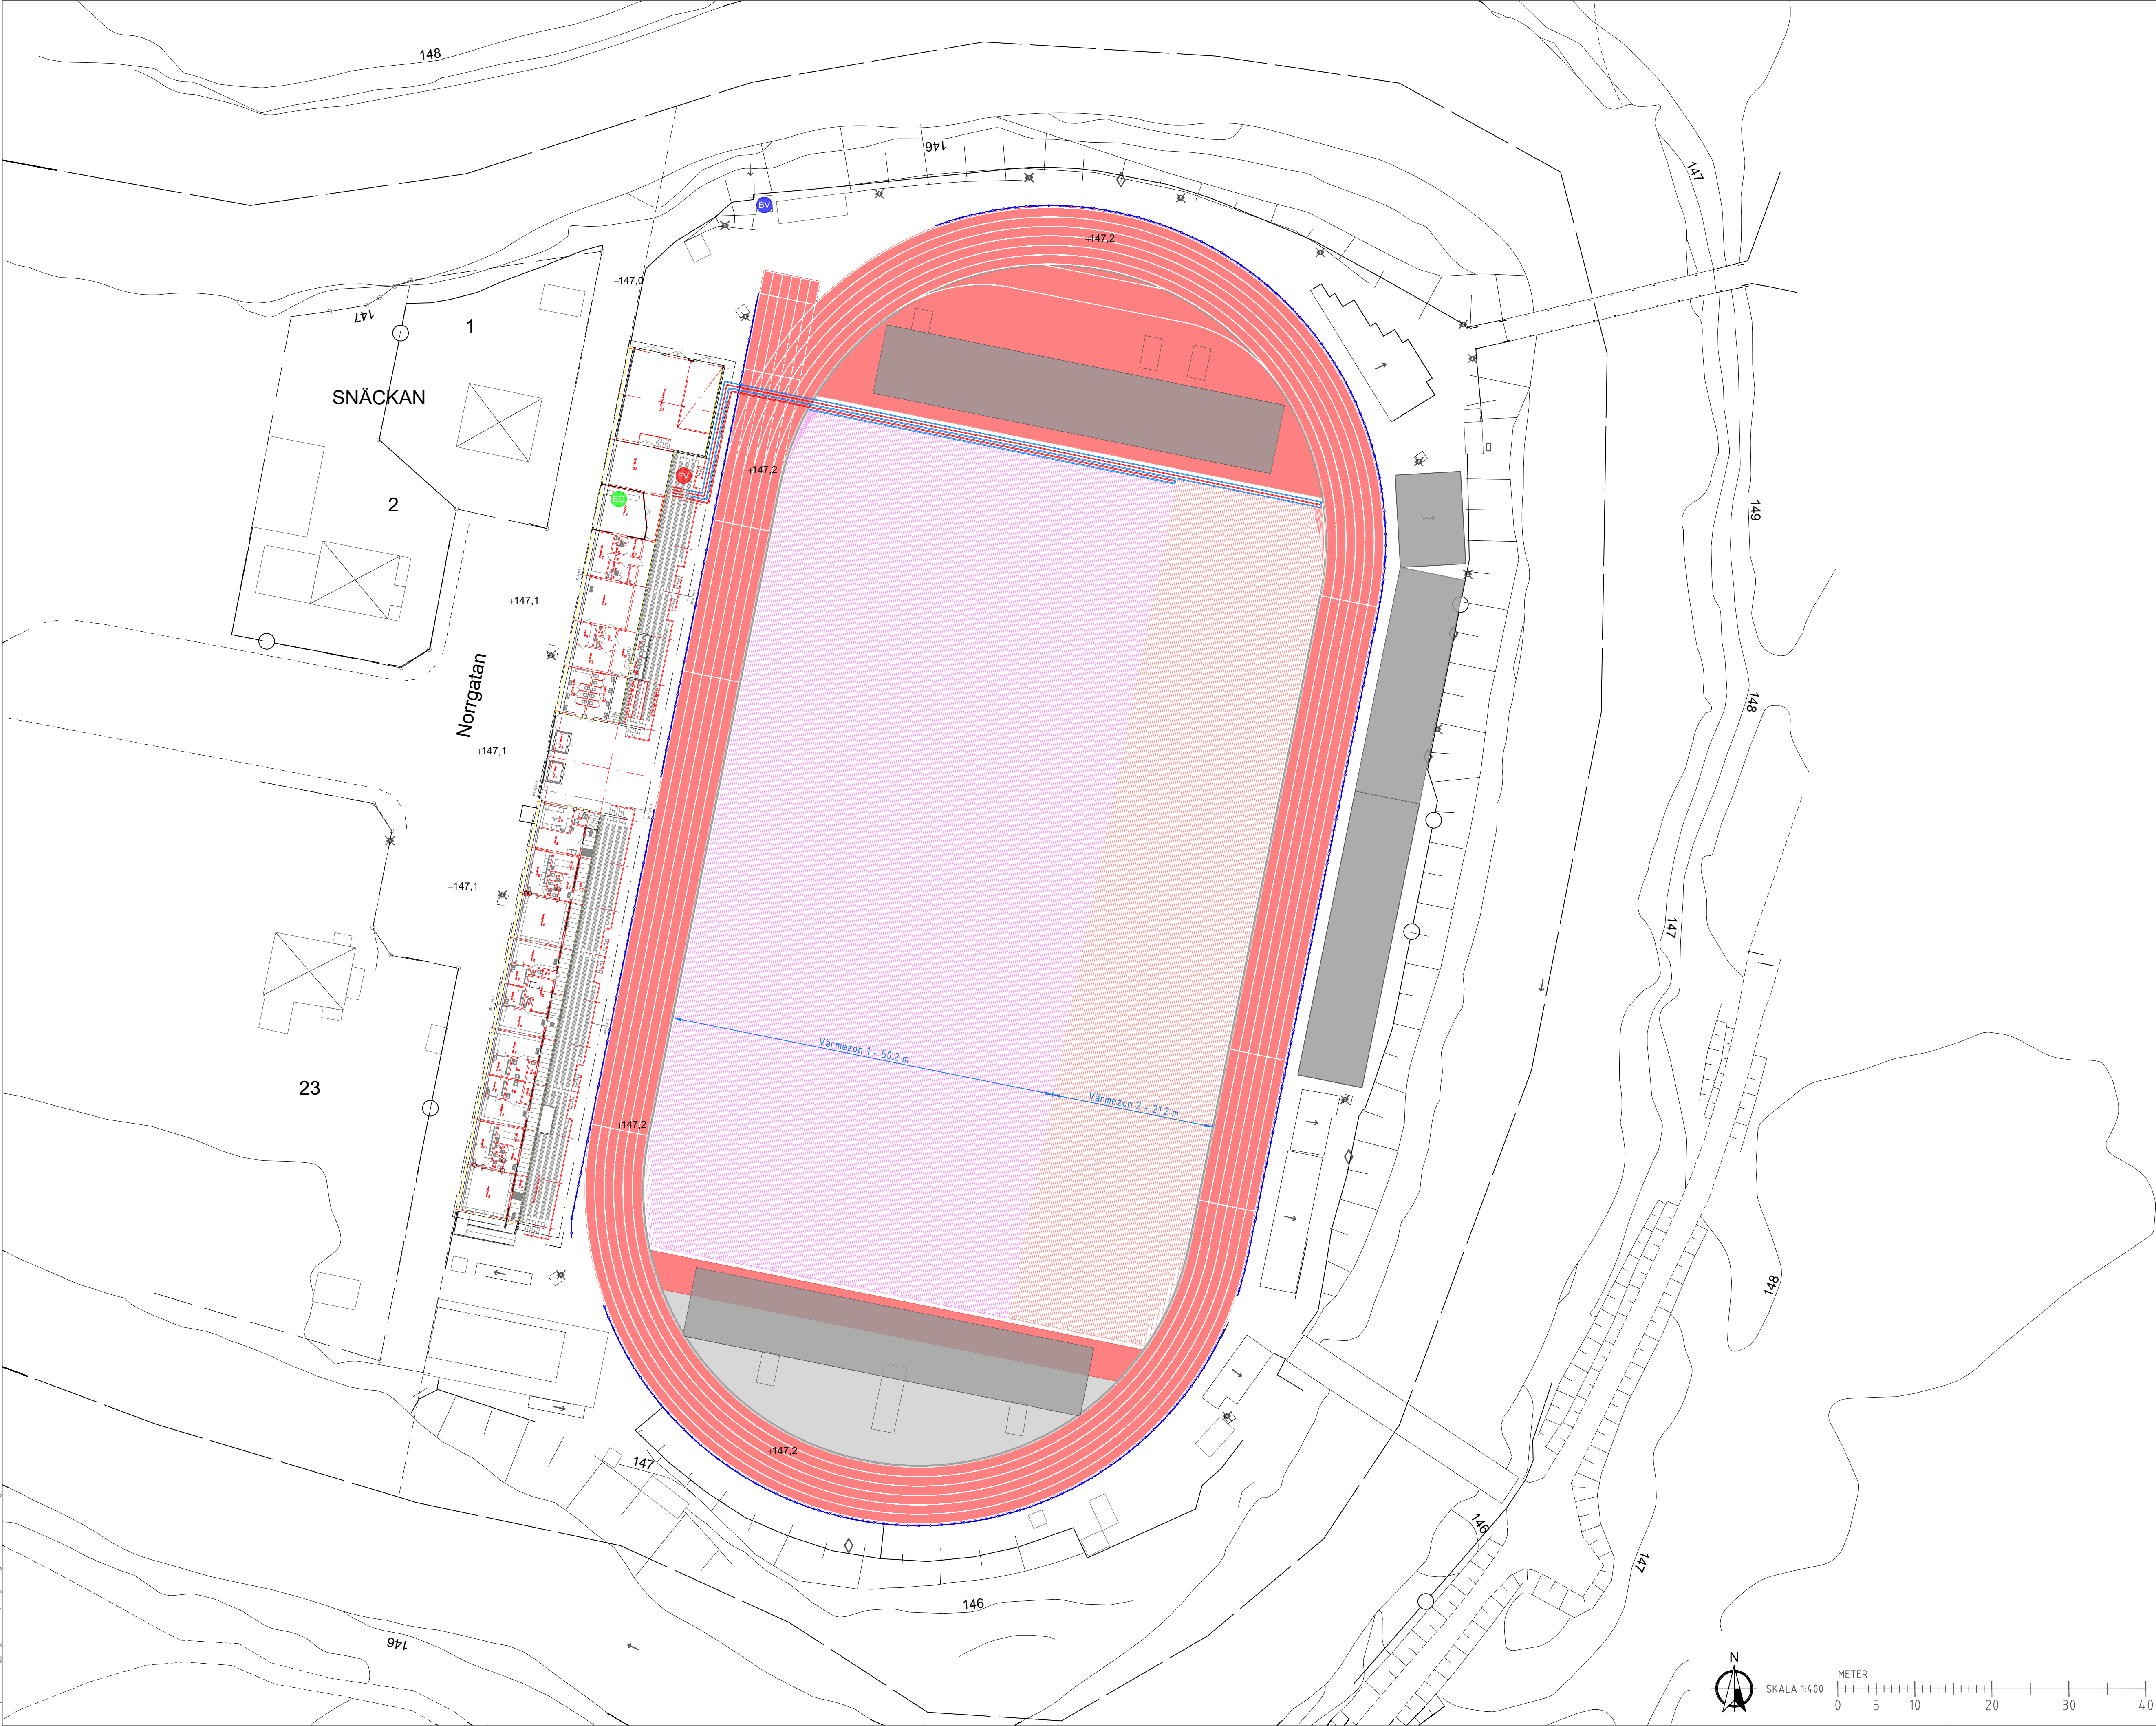

FÖRKLARINGAR

- Arbetsområde
- Räcke
- Nytt skåp med eluttag
- Bevatningspump
- Ny fjärrvärmecentral
- Befintlig elcentral

BET	ANT	ÄNDRINGEN AVSER	DATUM	SIGN
-----	-----	-----------------	-------	------

HANDLUSTYP
FORFRÅGNINGSUNDERLAG
PROJEKTENAMNING
MARKVÄRME OCH HYBRIDGRÄSPLAN
UPPDRAGSGIVARE



UPPDRAG NR		RTAD/KONSTR AV	PROJEKTNUMMER
2026-03-05		ANSVARIG	DISCIPLIN
MARKVÄRME OCH HYBRIDGRÄSPLAN		FINNVEDSVÄLLEN VÄRNAMO	
MARKVÄRMESYSTEM I MARK		REV	
FORMAT	SKALA	RITNINGSR	
A1	1:400	M-10-1-002	