

FÖRKLARINGAR

SYSTEM + LÖPNUMMER
MATERIAL + VARIANTNR
DIMENSION
ISOLERINGTYP

XX00-X00-000/X00
SYSTEM VÄRME
FJV1 FJÄRRVÄRME

SYSTEM TAPPVATTEN
KV1 KALLVATTEN, OAVHÄRDAT, 5 °C
KV2 KALLVATTEN, AVHÄRDAT, 5 °C
VV1 VARMVATTEN, 55°C
VVC1 VARMVATTENCIRKULATION, 50°C

SYSTEM SPILLVATTEN
D1 DAGVATTEN, ALLMÄNT I MARK
S1 SPILLVATTEN, ALLMÄNT I MARK
S2 SPILLVATTEN, ALLMÄNT INOMHUS
S3 SPILLVATTEN FRÅN STORKÖK

MATERIAL RÖR
E13 PEM, TRYCKRÖR
S6 STÅLRÖR, TUBRÖR TRYCKKÄRLSKVALITET, SVETSGOG
X31 LEDNINGAR AV PEX (PE-XA) MED RIR

MATERIAL SPILLVATTEN
E4 PE-RÖR, TRYCKRÖR, PN16
P2 LEDNINGAR AV PP-RÖR, SLÄTA
MARKAVLOPPSRÖR I BYGGNAD
R8 LEDNINGAR AV ROSTFRIA RÖR

ISOLERING
W MINERALULL FABRIKSMONTERAD ALU-PLÅT
V CELLGUMMISLANG
YTBEKLÄDNAD
B PLASTPLÅT
C MÖNSTERPRÄGLAD ALU-PLÅT

KOMPONENTER
ALxxx AVLUFTARE
Bxxx GOLVBRUNN
BLxxx BLÅNDARE
DBxxx DISKBÄNKAR
DM DISKMASKIN
IL INSPEKTIONSLUCKA (UTFÖRS AV BE)
KM KOMBI-MASKIN
RLx RENSÖR, MED LOCK
SL1 SERVICELUCKA, 150x150, INGÅR I BE
TM TVÄTTMASKIN
TSxxx TVÄTTSTALL
VLOxxx VATTENLÅS
VKxxx VATTENKLOSETT

ÖVRIGT
ANSL ANSLUTNING
CL CENTRUMLINJE
FG FÄRDIGT GOLV
ÖFG ÖVER (FÄRDIGT) GOLV
INK INKÖPPLING
UK UNDERKANT
VG VATTENGÅNG
(L) AVLOPPSLUFTARE

KOPPLINGSLEDNINGAR
FÖLJANDE GÄLLER OM EJ ANNAT ANGES:
DOLDA KV/VV1(1-2)-X31
ANSL KV VV S
B - - 75
BL 16(15) 16(15) -
TS 16(12) 16(12) 75
UB 16(12) 16(12) 75
VK 16(12) - 110

B	ENL. PM-2	2024-05-07	A.B.
A	ENL. PM-1	2024-04-19	A.B.
REV	ÄNDRINGEN	AVSER	DATUM SIGN

BYGGHANDLING
FASTIGHETSBETECKNING
OSTRA KASERN 3







Kristianstads
kommun

Västra Storgatan 12
291 80 KRISTIANSTAD
Telefon: 044-13 50 00

A		
K		
V		
E		
X	L VINNERSG AB	+46 101 02 44 00
B		
SK		
ANSVARIG L.F.	RITAD/KONSTR AV A.B.	HANDLGGARE L.F.
PROJEKT NR 2029304	DATUM 2024-03-01	REV.DATUM 2024-05-07
OBJEKTID 268140	HUS AA	VARNING 01
		DISCIPLIN W

ALLÖSKOLAN - HUS AA
VS-INSTALLATIONER
RÖR UNDER BOTTENPLATTA- DEL 1
FORMAT

SKALA A1 (A3) 1:50 (1:100)	RITINGSNUMMER W-50-1-A-0011	BET B
-------------------------------	--------------------------------	----------

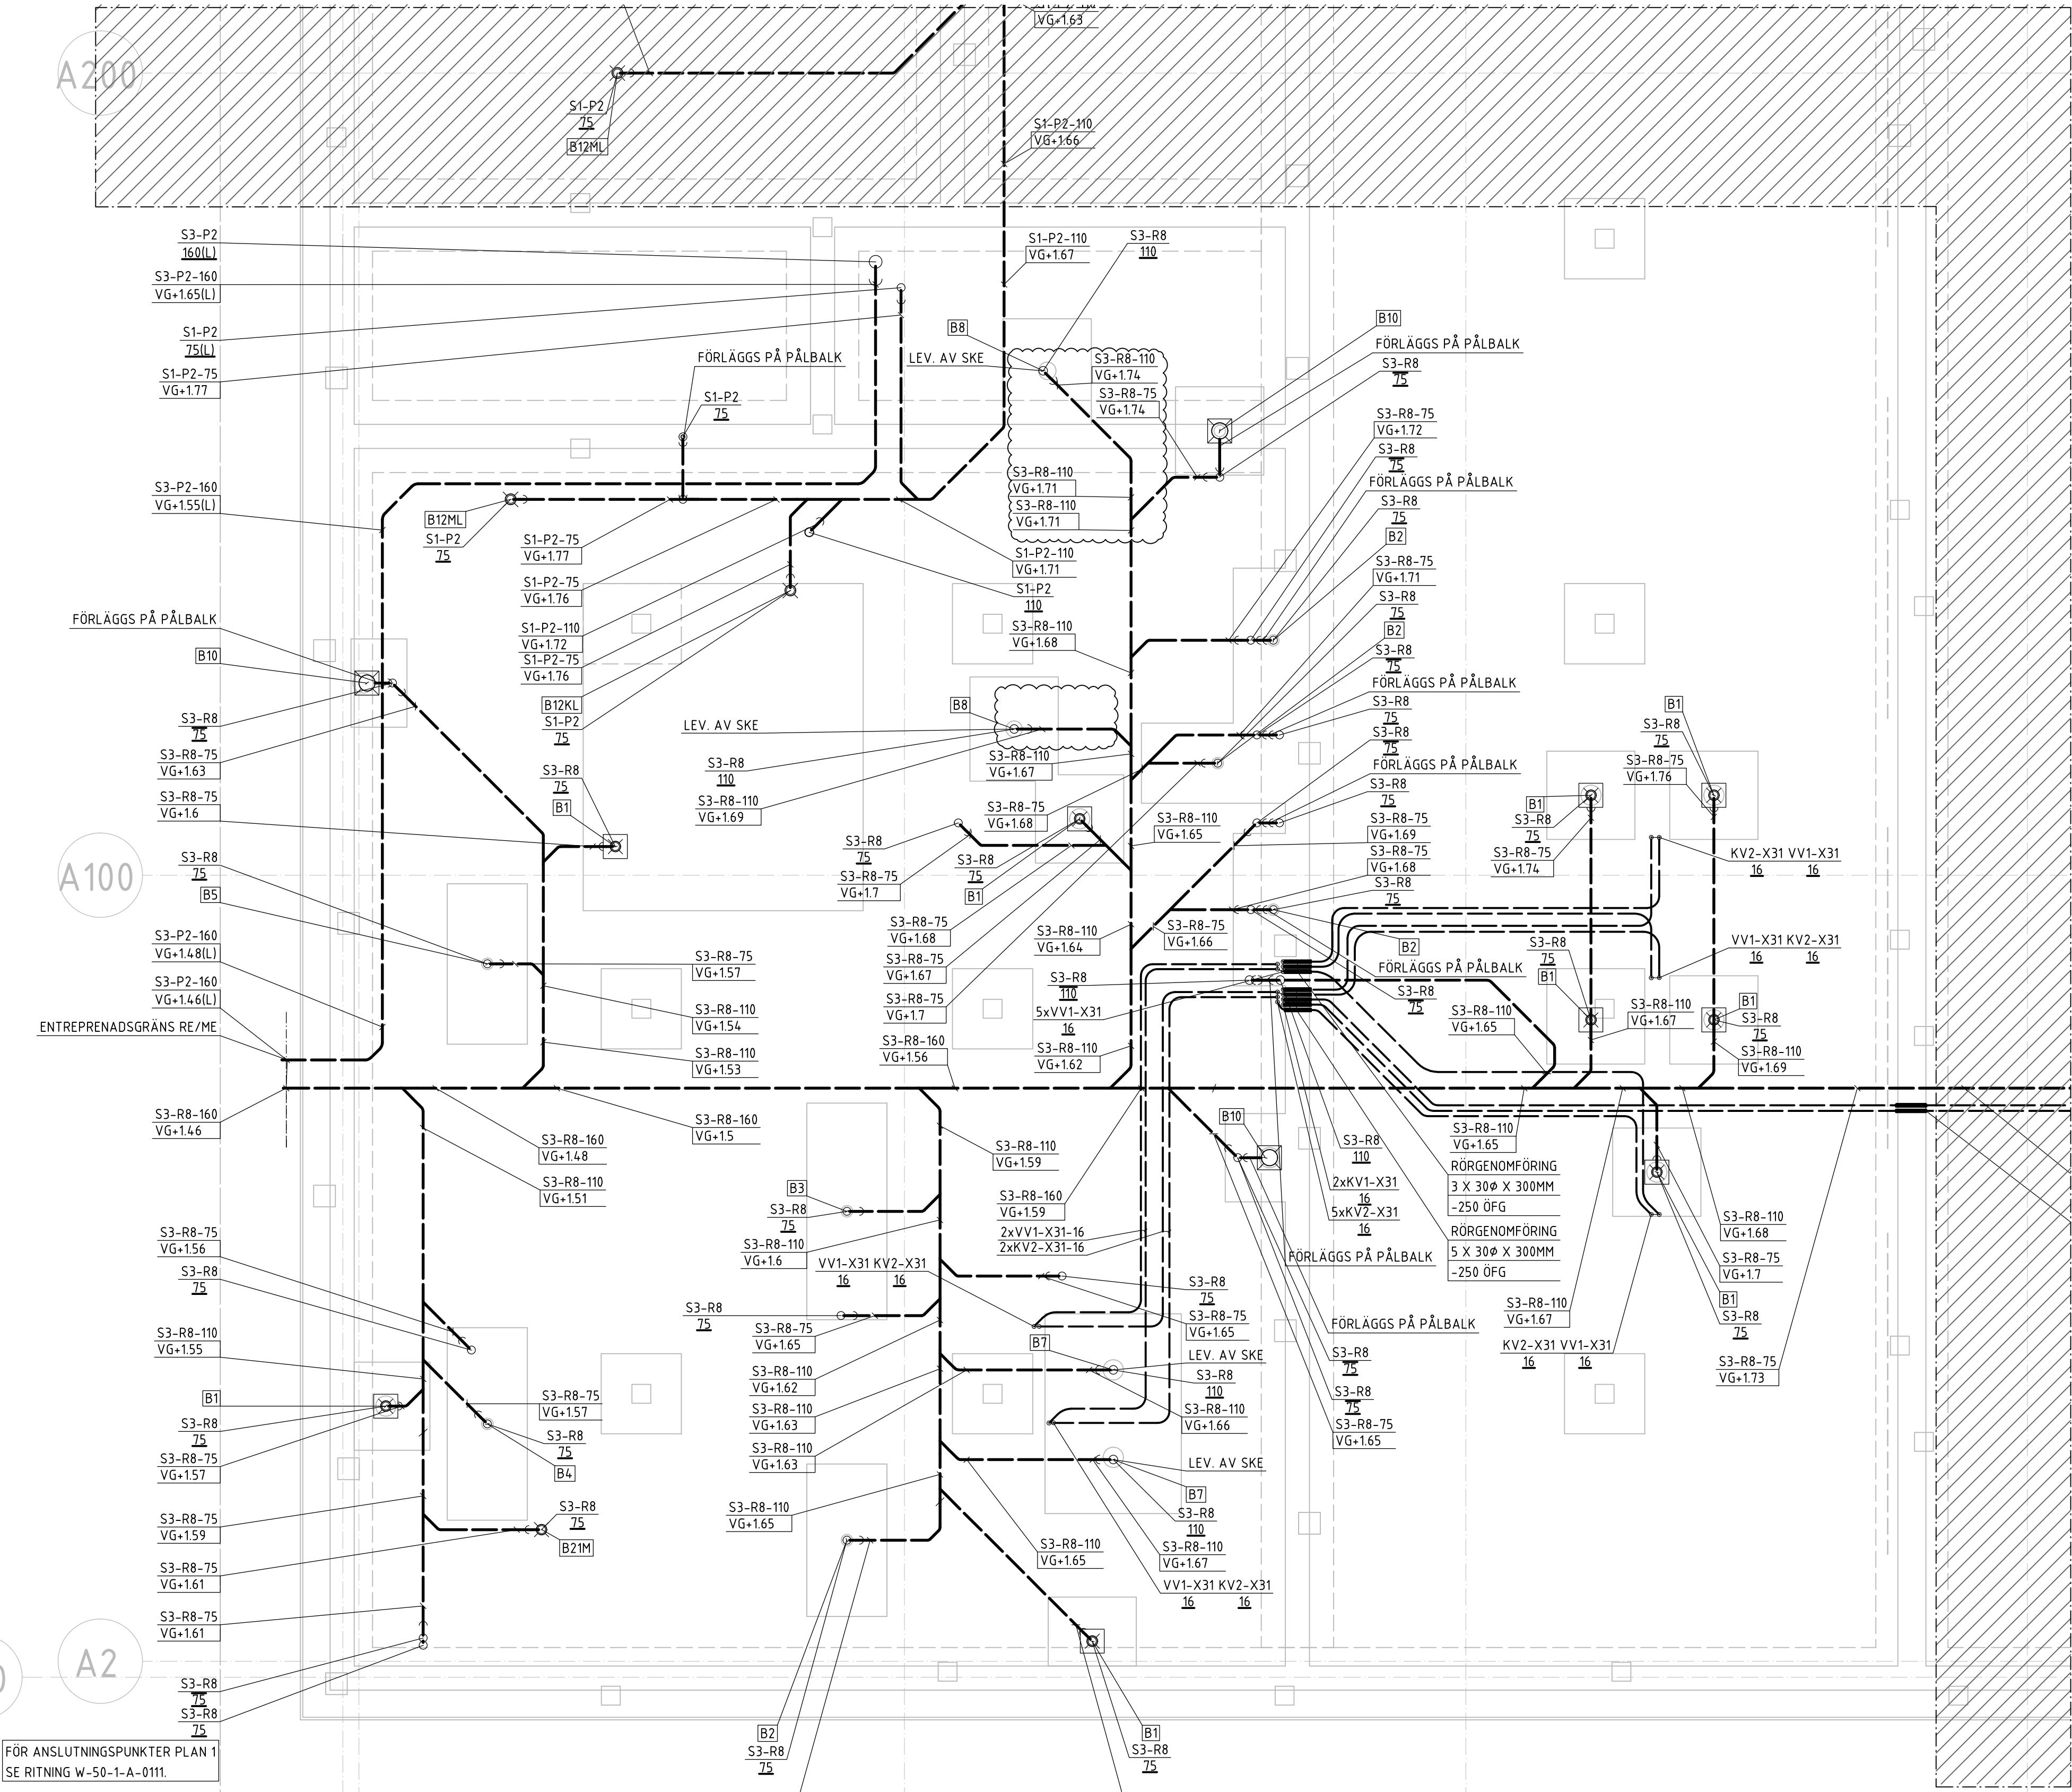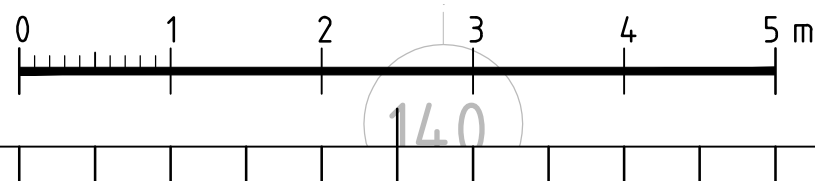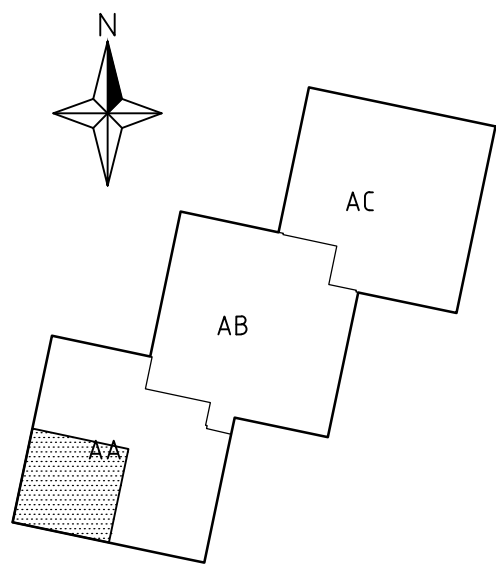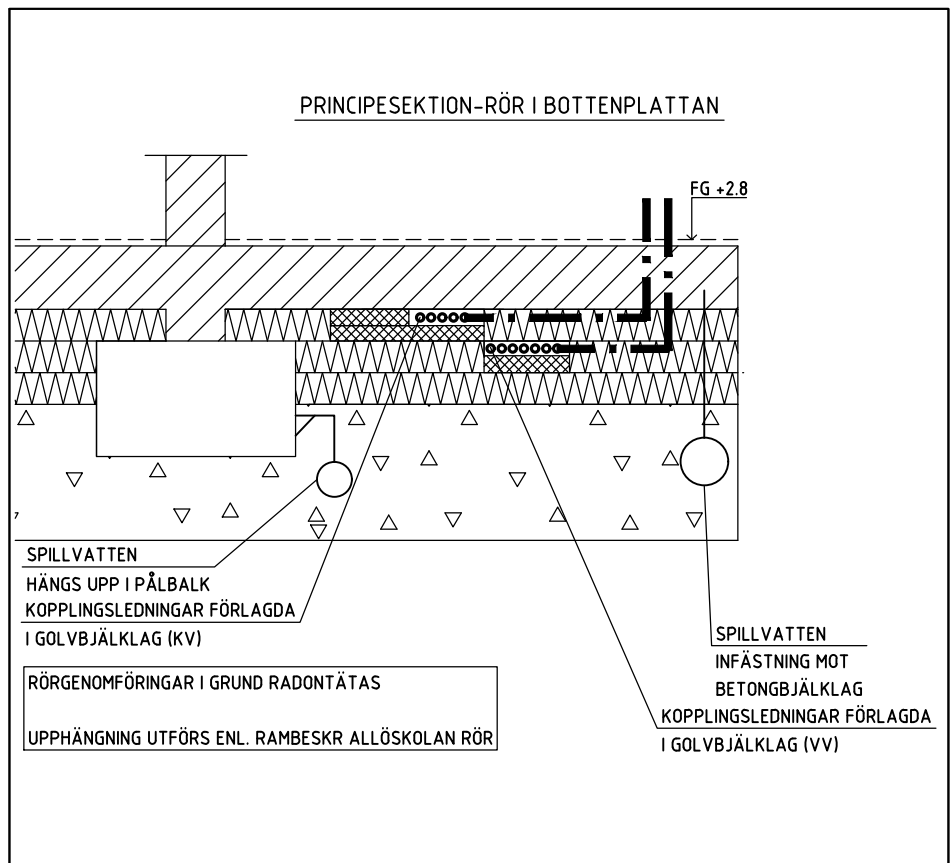

INGÅR I VS
B1-GOLVBRUNN 300x300 (8st)
B2-GOLVRÄNNA 1000x150 (4st)
B3-GOLVRÄNNA 1900x150 (1st)
B4-GOLVRÄNNA 1600x150 (1st)
B5-GOLVRÄNNA 1200x150 (1st)
B10-GOLVBRUNN 300x300 (3st)

INGÅR I SKE
B7-GOLVBRUNN 900x600 (2st)
B8-GOLVRÄNNA 500x300 (2st)

FÖR ANSLUTNINGSPUNKTER PLAN 1
SE RITNING W-50-1-A-011.