
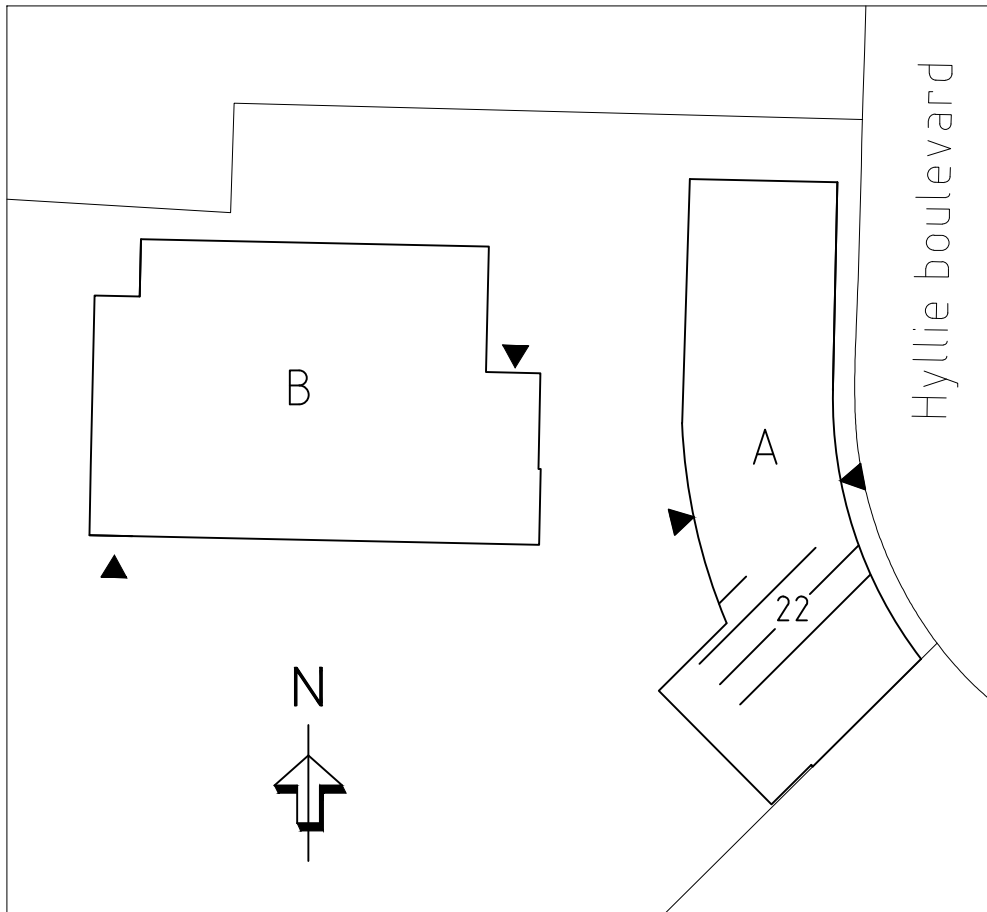


XREF: .\1\SVK\SK-modell\SK-16-P-0100-1764-A.dwg
.\1\A.A-modell\A-10-P-0100-1764-A.dwg
.\1\A.A-modell\orienteringsfig.dwg
.\1\A.A-modell\orienteringsfig.dwg
.\1\A.A-modell\orienteringsfig.dwg

LAGER: SB11

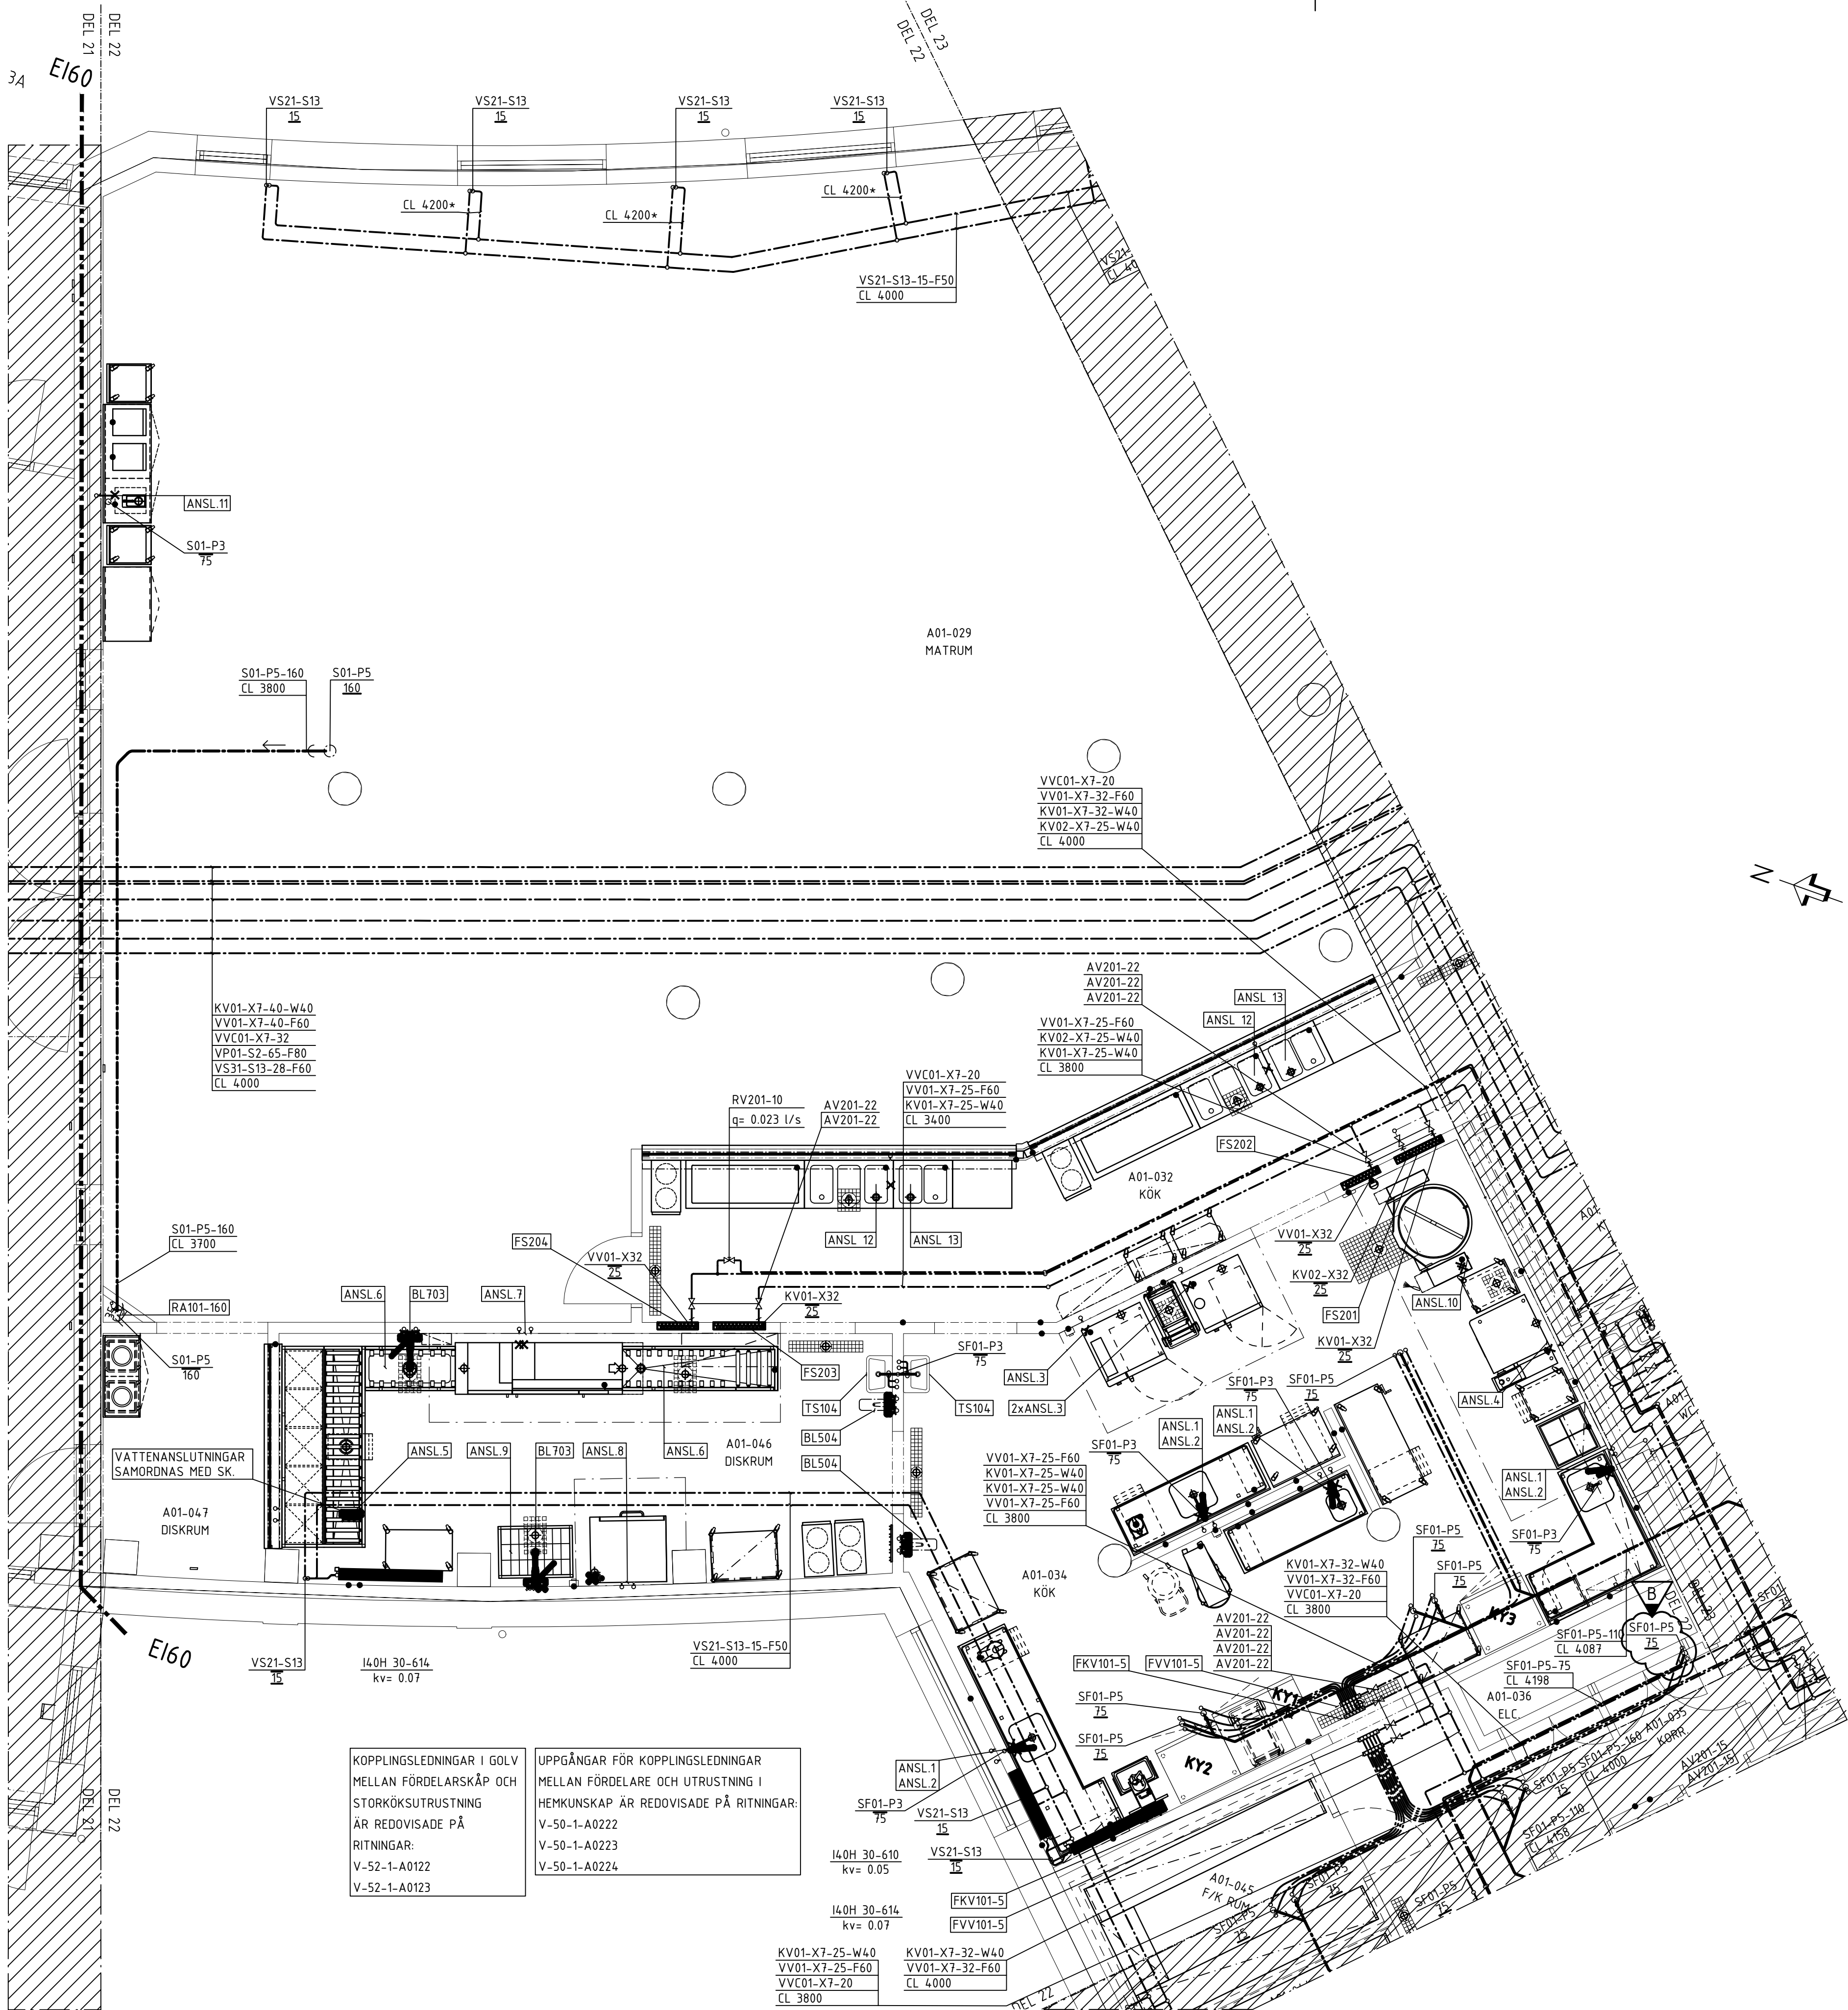

FÖRKLARINGAR

BETECKNING RÖRSYSTEM

VS11-S13-42-F100 - (100) mm

(L-F) Ev. isolering.

(42) Dimension

(S13) Rörmaterial

(11) Systemnummer

(VS) Systembeteckning

TAPPVATTENSYSTEM

KV01 Tappkallvatten

KV02 Tappkallvatten, kombiugn

VV01 Tappvarmvatten

VVC01 Varmvattencirkulation

SPILLVATTENSYSTEM

S01 Spillvatten

SF01 Spillvatten, fettavskiljare

S01 Fall min: 1%

SF01 Fall min: 2%

VÄRMEVATTENSYSTEM

FJV01 Fjärrvärme

VP01 Värmebärare, primär

VS11 Värmebärare, sekundär, ventilation

VS21 Värmebärare, sekundär, radiatorer

VS31 Värmebärare, sekundär, golvvärme

RÖRLEDNINGAR

G3 MA-rör

K5 Kopparrör Frkr

P2 PP markavloppsror

P3 PP-rör (avlopp inomhus)

P5 PP-rör (avlopp inomhus luddämpat)

R2 Ledningar av syrafast stål

R10 Rostfritt avloppsror, muff

S2 Handelsstub, ståltub

S6 Tryckkärlsstål

S13 Presskopplingsrör utv förs

X7 PAL-RÖR

X31 PEX-RIR

X32 PEX-RIR, extraisolerade

ISOLERING AV INSTALLATIONER

-F Mineralull

-W Mineralull, diffusionstät

VV01 & VVC01 SAMISOLERAS

SAKVAROR

Enl. BESKRIVNING AVSEENDE

VÄRME- OCH SANITÄTSANLÄGGNING

HANDLINGSNUMMER 11.A.2.1

MÄRKNING AV STYRKOMPONENTER

Föregås av 1764-A-

ÖVRIGT

CL xxxx* = Samma rördimension som stick och isolering F50

KOPPLINGSLEDNINGAR

FRÅN FÖRDELARE TILL APPARAT ENLIGT TABELL OM INGET ANNAT ANGES

VV01-X31	KV01-X31
BL	TS
TS	UB
UB	VK

B	1	PM5-W	231113	K. PERSSON
A	0	PM1-W	230601	K. PERSSON
BET	ANT	ÄNDRINGEN AVSER	DATUM	SEN
BYGGHANDLING				
 Malmö stad Stadsfastigheter				
HYLLIE NYA HÖGSTADIUM OCH SPORSTALL 3			PROJEKT NR	
NYBYGGNAD AV SKOLA OCH SPORSTALL			5800	
 SWECO Sweco Sverige AB - Tel: 08-695 60 00 - www.sweco.se				
FÖRETAG			TEL	
SWECO SVERIGE AB			040 - 16 70 00	
UPPDRAGSNUMMER			HANDLÄGGARE	
30025113			D. HAGSTRÖM	
DATUM			ANSVARIG	
2023-01-31			J. ÅKESSON	
RUNDSTICKAN 1				
RÖRINSTALLATIONER				
HUS A PLAN 1 DEL 22				
OBJEKTSNUMMER	BYGGNAD	PLAN	DEL	UNDERGRUPP
1764	A	01	22	50
SKALA	RITINGSNUMMER	BET		
1:50	V-50-1-A0122	B		

\\SELUP05002\PROJEKT\213321\30025113_HYLLIE_NYA_HÖGSTADIUM\0000_0 CAD\WV-MODELL\V-50-P-0100-1764-A.DWG PERSSON, KRISTOFFER