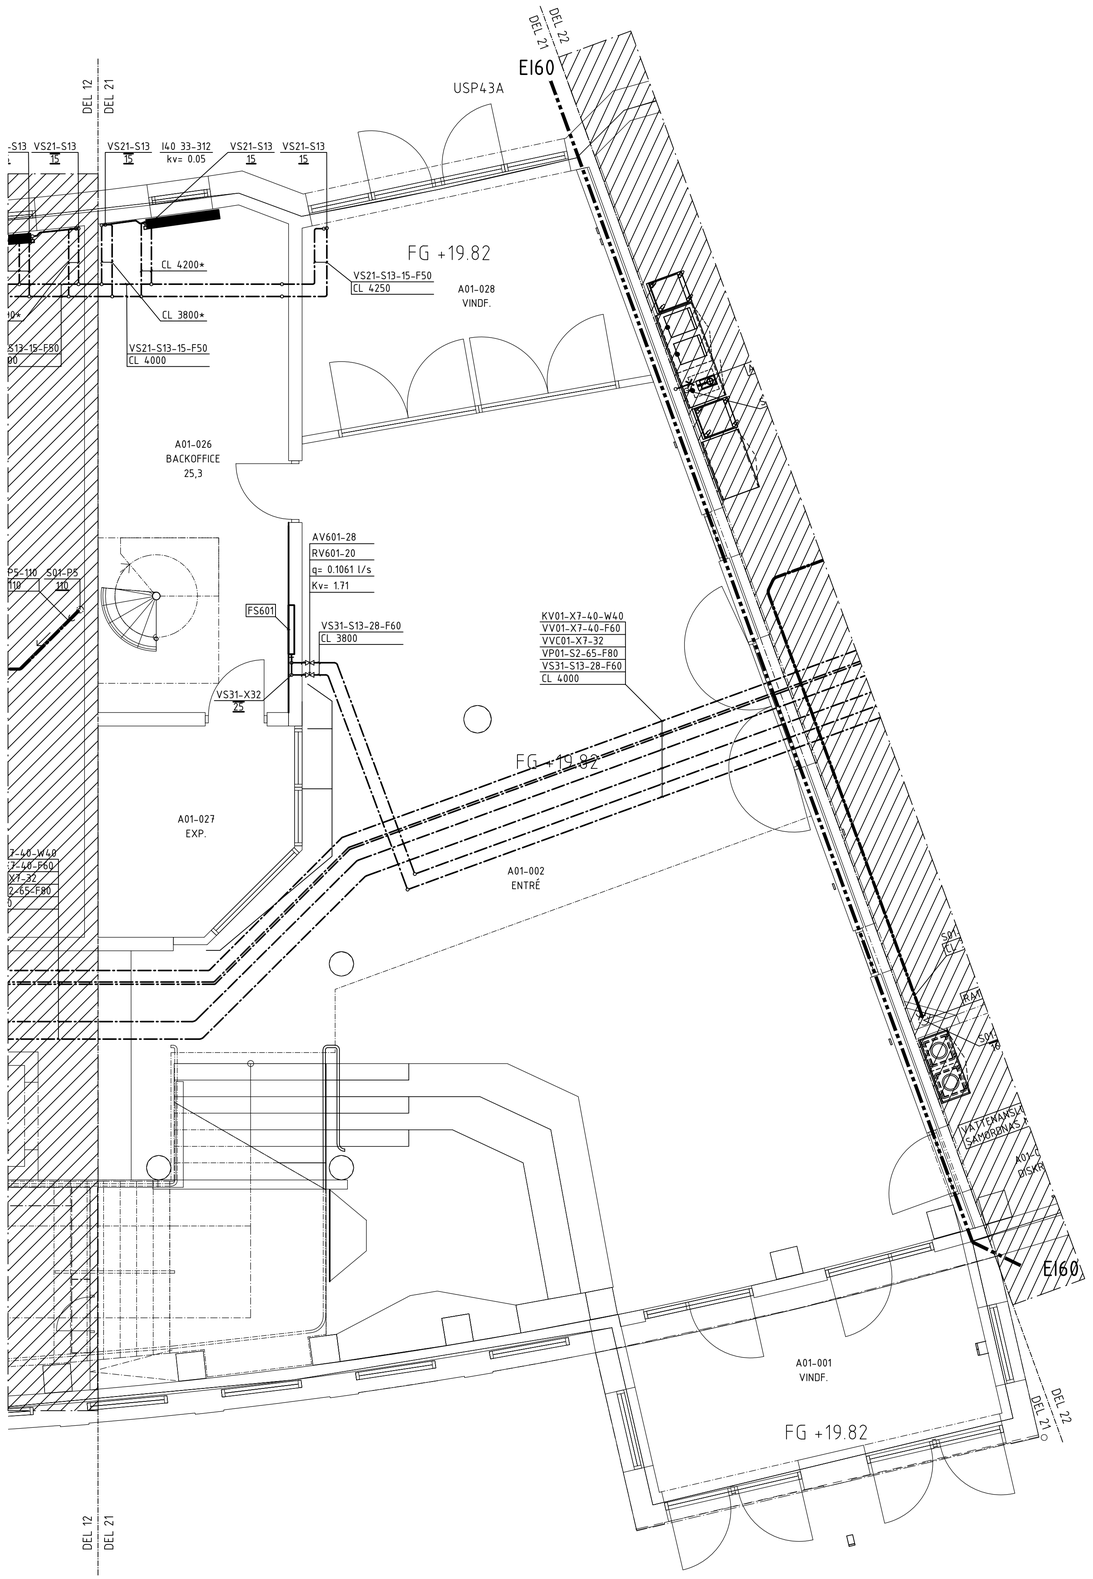

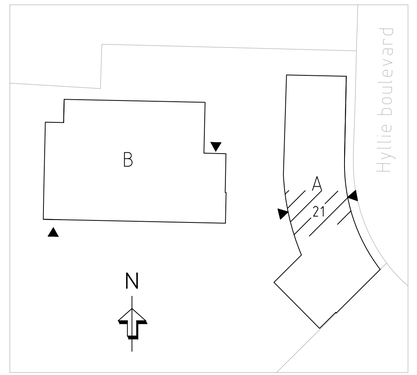

FÖRKLARINGAR

BETECKNING RÖRSYSTEM
VS11-S13-42-F100 — (100) mm
(-F) Ev. isolering.
(42) Dimension
(S13) Rörmaterial
(11) Systemnummer
(VS) Systembeteckning

TAPPVATTENSYSTEM
KV01 Tappkallvatten
KV02 Tappkallvatten, kombiugnar
VV01 Tappvarmvatten
VVC01 Varmvattencirkulation

SPILLVATTENSYSTEM
S01 Spillvatten
SF01 Spillvatten, fettavskiljare

S01 Fall min: 1%
SF01 Fall min: 2%

VÄRMEVATTENSYSTEM
FJV01 Fjärrvärme
VP01 Värmebärare, primär
VS11 Värmebärare, sekundär, ventilation
VS21 Värmebärare, sekundär, radiatorer
VS31 Värmebärare, sekundär, golvvärme

RÖRLEDNINGAR
G3 MA-rör
K5 Kopparrör Frkr
P2 PP marksavloppsrör
P3 PP-rör (avlopp inomhus)
P5 PP-rör (avlopp inomhus ljuddämpat)
R2 Ledningar av syrafast stål
R10 Rostfritt avloppsrör, muff
S2 Handelstub, stålrub
S6 Tryckkärlsstål
S13 Presskopplingsrör utv förs
X7 PAL-RÖR
X31 PEX-RiR
X32 PEX-RiR, extraisolerade

ISOLERING AV INSTALLATIONER
-F Mineralull
-W Mineralull, diffusionstät

VV01 & VVC01 SAMISOLERAS

SAKVAROR
Enl. BESKRIVNING AVSEENDE
VÄRME- OCH SANITETSANLÄGGNING
HANDLINGSNUMMER 11.A.2.1

MÄRKNING AV STYRKOMPONENTER
Föregås av 1764-A-

ÖVRIGT
CL xxxx* = Samma rördimension som stick och isolering F50

KOPPLINGSLEDNINGAR FRÅN FÖRDELARE TILL APPARAT ENLIGT TABELL OM INGET ANNAT ANGES		
	VV01-X31	KV01-X31
BL	16x	16x
TS	16x	16x
UB	16x	16x
VK		16x

BET	ANT	ÄNDRINGEN AVSER	DATUM	SIGN
A	0	PM1-W	230601	K. PERSSON

BYGGHANDLING

Malmö stad
Stadsfastigheter

HYLLIE NYA HÖGSTADIUM OCH SPORTHALL 3 PROJEKT NR
NYBYGGNAD AV SKOLA OCH SPORTHALL 5800

SWECO
Sweco Sverige AB - Tele: 08-695 60 00 - www.sweco.se

FÖRETAG		TEL
SWECO SVERIGE AB		040 - 16 70 00
UPPDRAGSNUMMER	RITAD AV	HANDLÄGGARE
30025113	K. PERSSON	D. HAGSTRÖM
DATUM	REV. DATUM	ANSVARIG
2023-01-31	2023-06-01	J. ÅKESSON

RUNDSTICKAN 1
RÖRINSTALLATIONER
HUS A PLAN 1 DEL 21

OBJEKTSNUMMER	BYGGNAD	PLAN	DEL	UNDERGRUPP	DISCIPLIN
1764	A	01	21	50	W

SKALA	RITNINGSNUMMER	BET
1:50	V-50-1-A0121	A

SKALA 1:50 (A1) 0 1 2 3 4 5

LAGER: SB11

XREF: ..\SK\SK-modell\SK-46-P-0100-1764-A.dwg
..\..\VA\A-modell\VA-40-P-0100-1764-A.dwg
..\..\VA\A-modell\orienterings fig.dwg
..\Slips\Slips - Skola.dwg

PLO: 2023-05-30 09:56 \\SELUDFS002\PROJEKT\243321\30025113_HYLLIE_NYA_HÖGSTADIESKOLA\000\10 CAD\VVW-MODELL\V-50-P-0100-1764-A.DWG PERSSON, KRISTOFFER