


XREF: .\\1\\SK\\SK-modell\\SK-16-P-0100-1764-A.dwg
.\\1\\A\\A-modell\\A-10-P-0100-1764-A.dwg
.\\1\\A\\A-modell\\orienteringsfig.dwg
.\\1\\A\\A-modell\\orienteringsfig.dwg
.\\1\\A\\A-modell\\orienteringsfig.dwg

LAGER: SB11

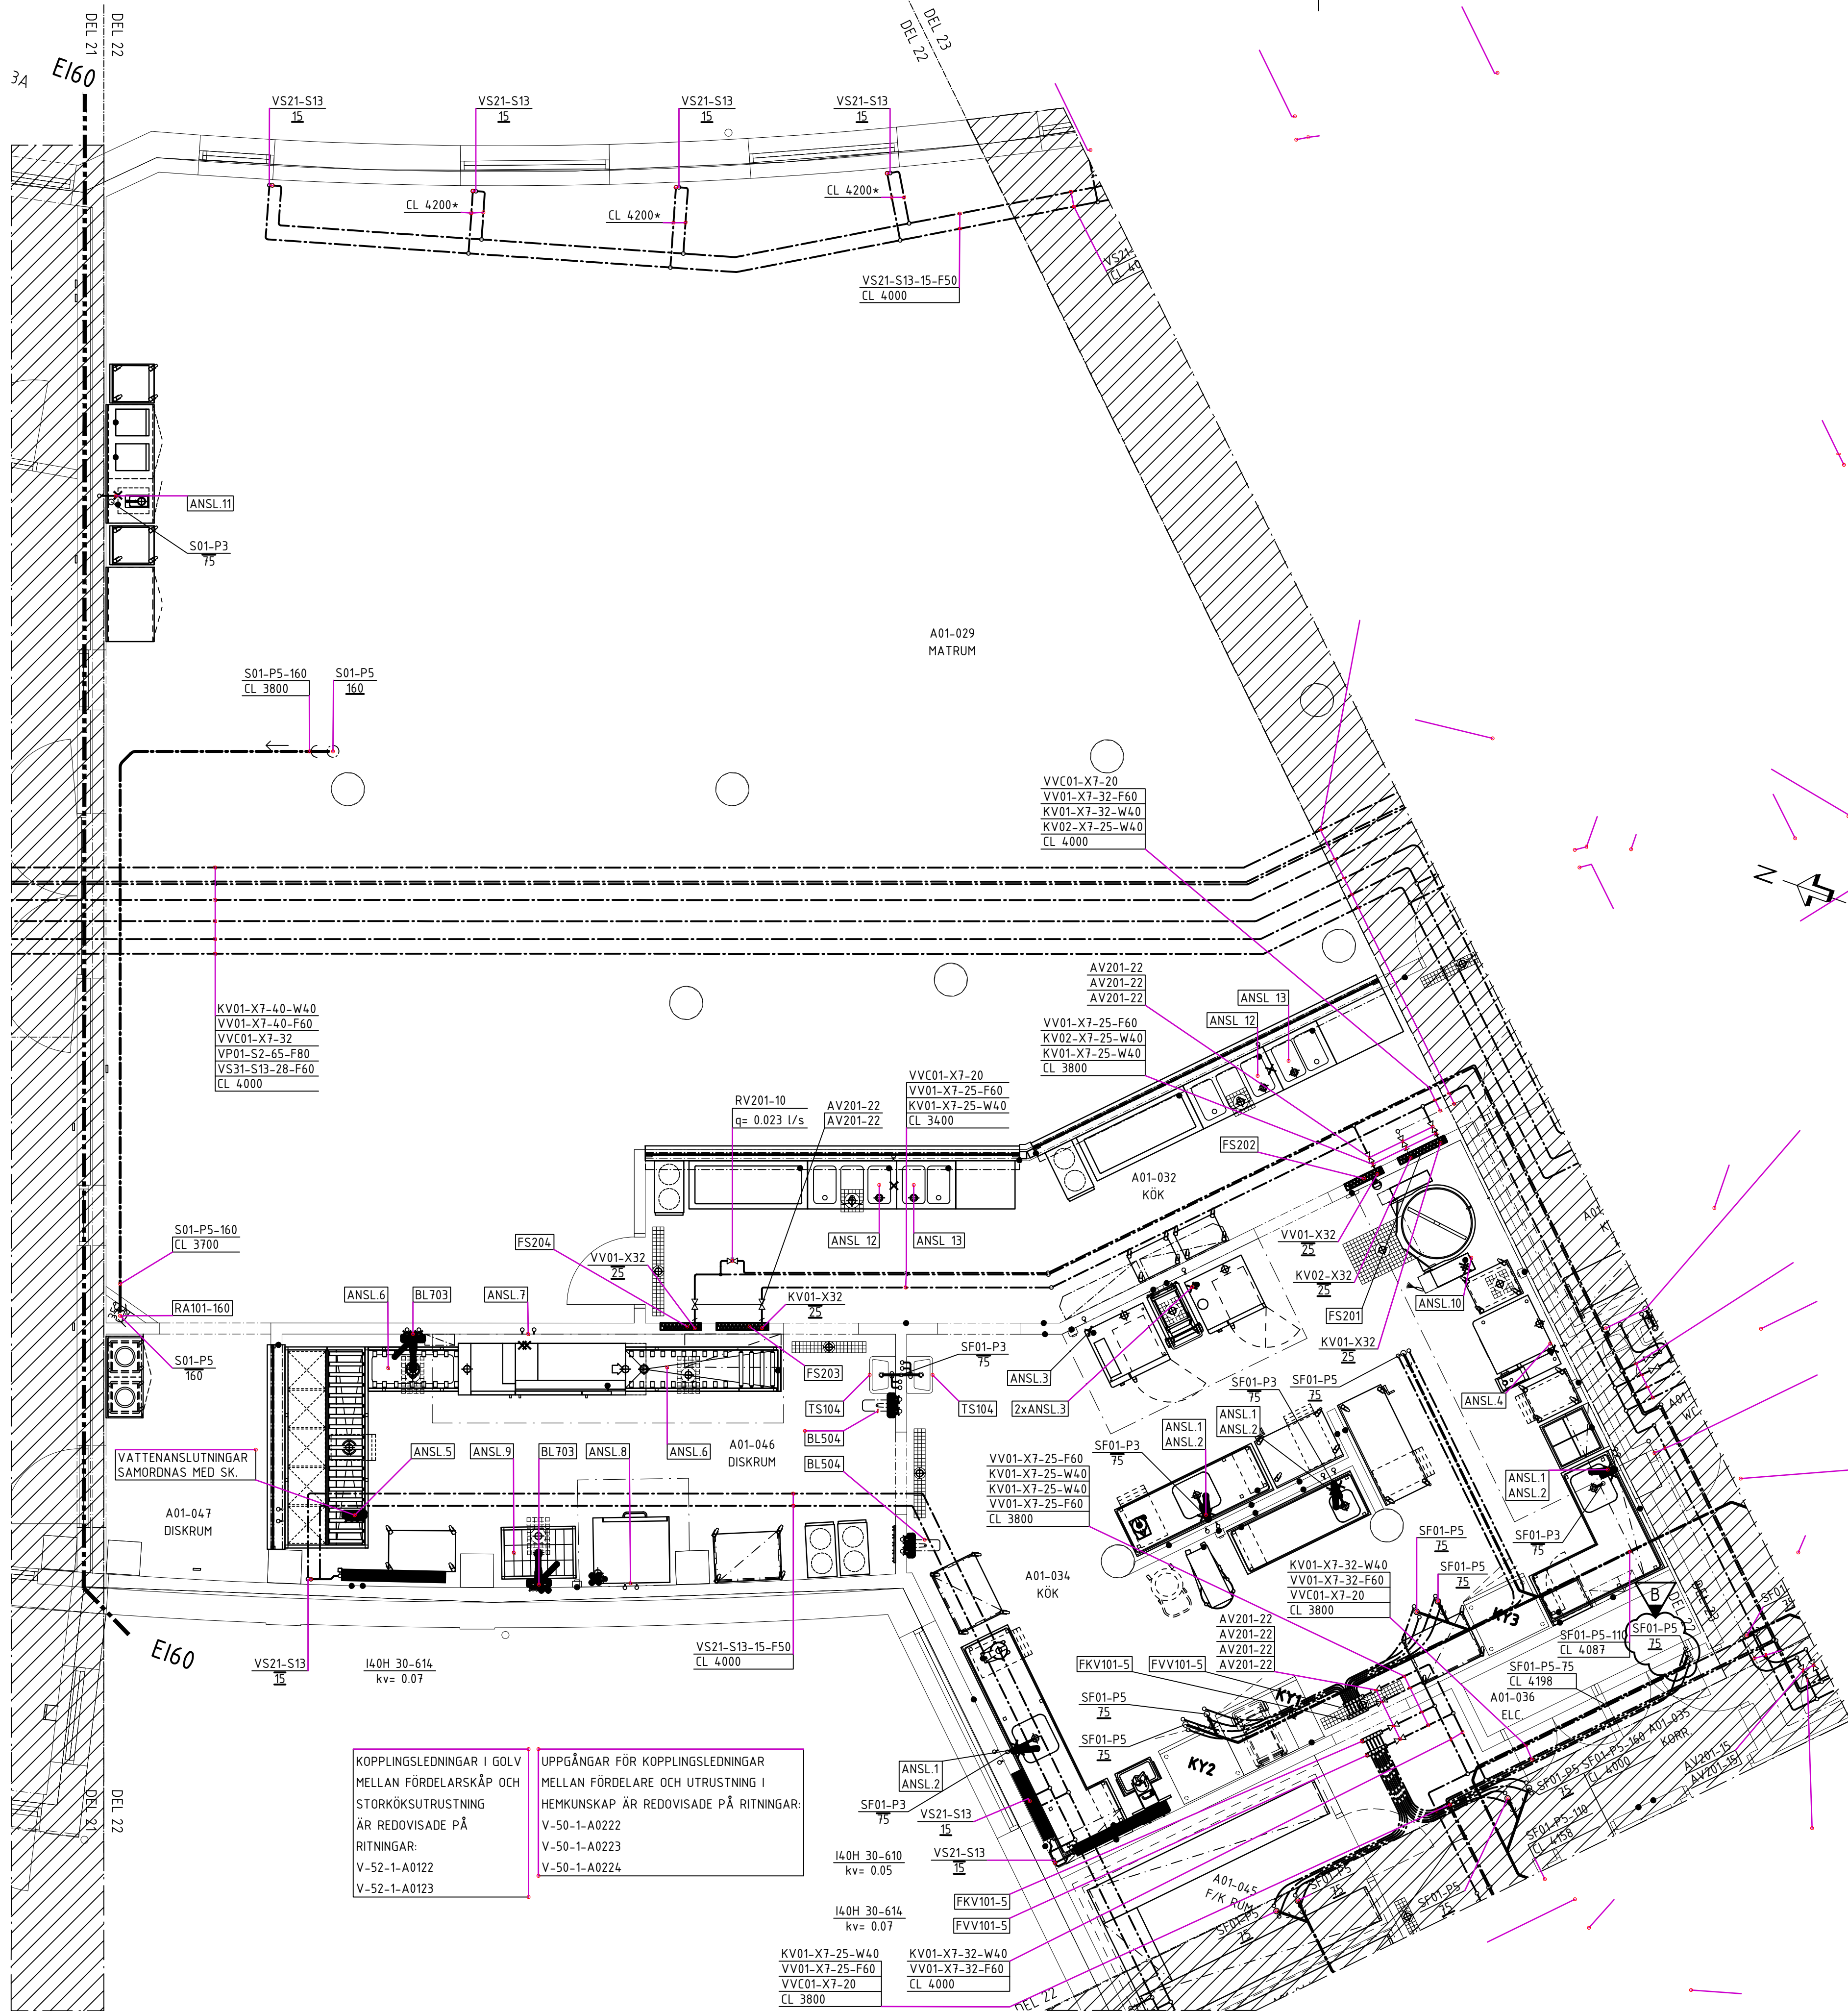

FÖRKLARINGAR
BETECKNING RÖRSYSTEM
VS11-S13-42-F100 - (100) mm
(L-F) Ev. isolering.
(42) Dimension
(S13) Rörmaterial
(11) Systemnummer
(VS) Systembeteckning

TAPPVATTENSYSTEM
KV01 Tappkallvatten
KV02 Tappkallvatten, kombiugn
VV01 Tappvarmvatten
VVC01 Varmvattencirkulation

SPILLVATTENSYSTEM
S01 Spillvatten
SF01 Spillvatten, fettavskiljare

S01 Fall min: 1%
SF01 Fall min: 2%

VÄRMEVATTENSYSTEM
FJV01 Fjärrvärme
VP01 Värmebärare, primär
VS11 Värmebärare, sekundär, ventilation
VS21 Värmebärare, sekundär, radiatorer
VS31 Värmebärare, sekundär, golvvärme

RÖRLEDNINGAR
G3 MA-rör
K5 Kopparrör, Frkr
P2 PP markavloppsror
P3 PP-rör (avlopp inomhus)
P5 PP-rör (avlopp inomhus luddämpat)
R2 Ledningar av syrefast stål
R10 Rostfritt avloppsror, muff
S2 Handelsstub, stålhub
S6 Tryckkärslstål
S13 Presskopplingsrör utv förs
X7 PAL-RÖR
X31 PEX-RIR
X32 PEX-RIR, extraisolerade

ISOLERING AV INSTALLATIONER
-F Mineralull
-W Mineralull, diffusionstät

VV01 & VVC01 SAMISOLERAS

SAKVAROR
Enl. BESKRIVNING AVSEENDE
VÄRME- OCH SANITETSANLÄGGNING
HANDLINGSNUMMER 11.A.2.1

MÄRKNING AV STYRKOMPONENTER
Föregås av 1764-A-

ÖVRIGT
CL xxxx* = Samma rördimension som
stick och isolering F50

KOPPLINGSLEDNINGAR
FRÅN FÖRDELARE TILL
APPARAT ENLIGT TABELL
OM INGET ANNAT ANGES

VV01-X31	KV01-X31
BL	TS
TS	UB
UB	VK
VK	


KOPPLINGSLEDNINGAR I GOLV
MELLAN FÖRDELARSKÅP OCH
STÖRKÖKSUTRUSTNING
ÄR REDOVISADE PÅ
RITNINGAR:
V-52-1-A0122
V-52-1-A0123

UPPGÅNGAR FÖR KOPPLINGSLEDNINGAR
MELLAN FÖRDELARE OCH UTRUSTNING I
HEMKUNSKAP ÄR REDOVISADE PÅ RITNINGAR:
V-50-1-A0222
V-50-1-A0223
V-50-1-A0224

KV01-X7-25-W40
VV01-X7-25-F60
VVC01-X7-20
CL 3800

KV01-X7-32-W40
VV01-X7-32-F60
VVC01-X7-20
CL 4000

SKALA 1:50 (A1) 0 1 2 3 4 5

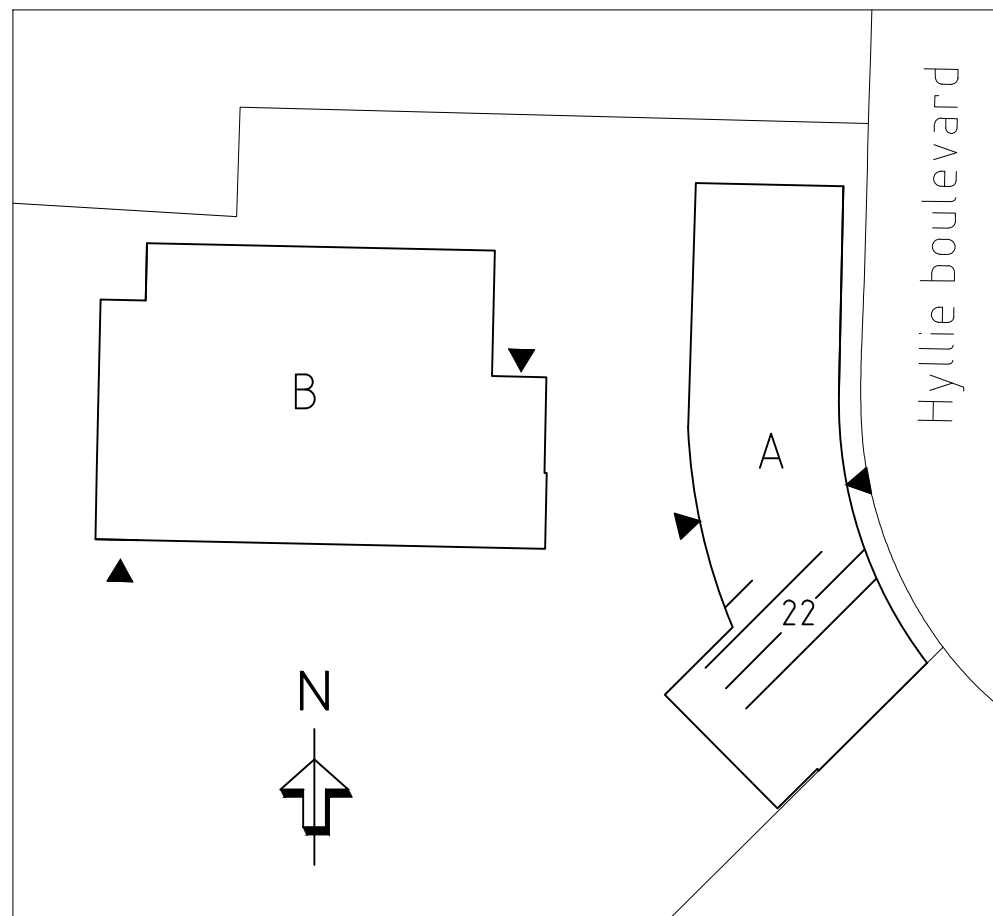

B	1	PM5-W	231113	K. PERSSON
A	0	PM1-W	230601	K. PERSSON
BET	ANT	ÄNDRINGEN AVSER	DATUM	SEN
BYGGHANDLING				
 Malmö stad Stadsfastigheter				
HYLLIE NYA HÖGSTADIUM OCH SPORTHALL 3 PROJEKT NR				
NYBYGGNAD AV SKOLA OCH SPORTHALL 5800				
 SWECO				
Sweco Sverige AB - Tel: 08-695 60 00 - www.sweco.se				
FÖRETAG SWECO SVERIGE AB			TEL 040 - 16 70 00	
UPPDRAGSNUMMER 30025113			HANDLÄGGARE D. HAGSTRÖM	
DATUM 2023-01-31			ANSVARIG J. ÅKESSON	
RUNDSTICKAN 1				
RÖRINSTALLATIONER				
HUS A PLAN 1 DEL 22				
OBJEKTSNUMMER	BYGGNAD	PLAN	DEL	UNDERGRUPP DISCIPLIN
1764	A	01	22	50 W
SKALA	RITINGSNUMMER			BET
1:50	V-50-1-A0122			B

\\SELUP\\5002\\PROJEKT\\21332\\30025113_HYLLIE_NYA_HÖGSTADIUM\\A000\\NO CAD\\V\\W-MODELL\\V-50-P-0100-1764-A.DWG PERSSON, KRISTOFFER

2023-11-13 08:17