


XREF: .\1\SVK\SK-model\SK-46-P-0100-1764-A.dwg
.1\A.A-model\A-40-P-0100-1764-A.dwg
.1\A.A-model\orienteringsfig.dwg
.1\Slips\Slips - Skola.dwg

LAGER: SB11

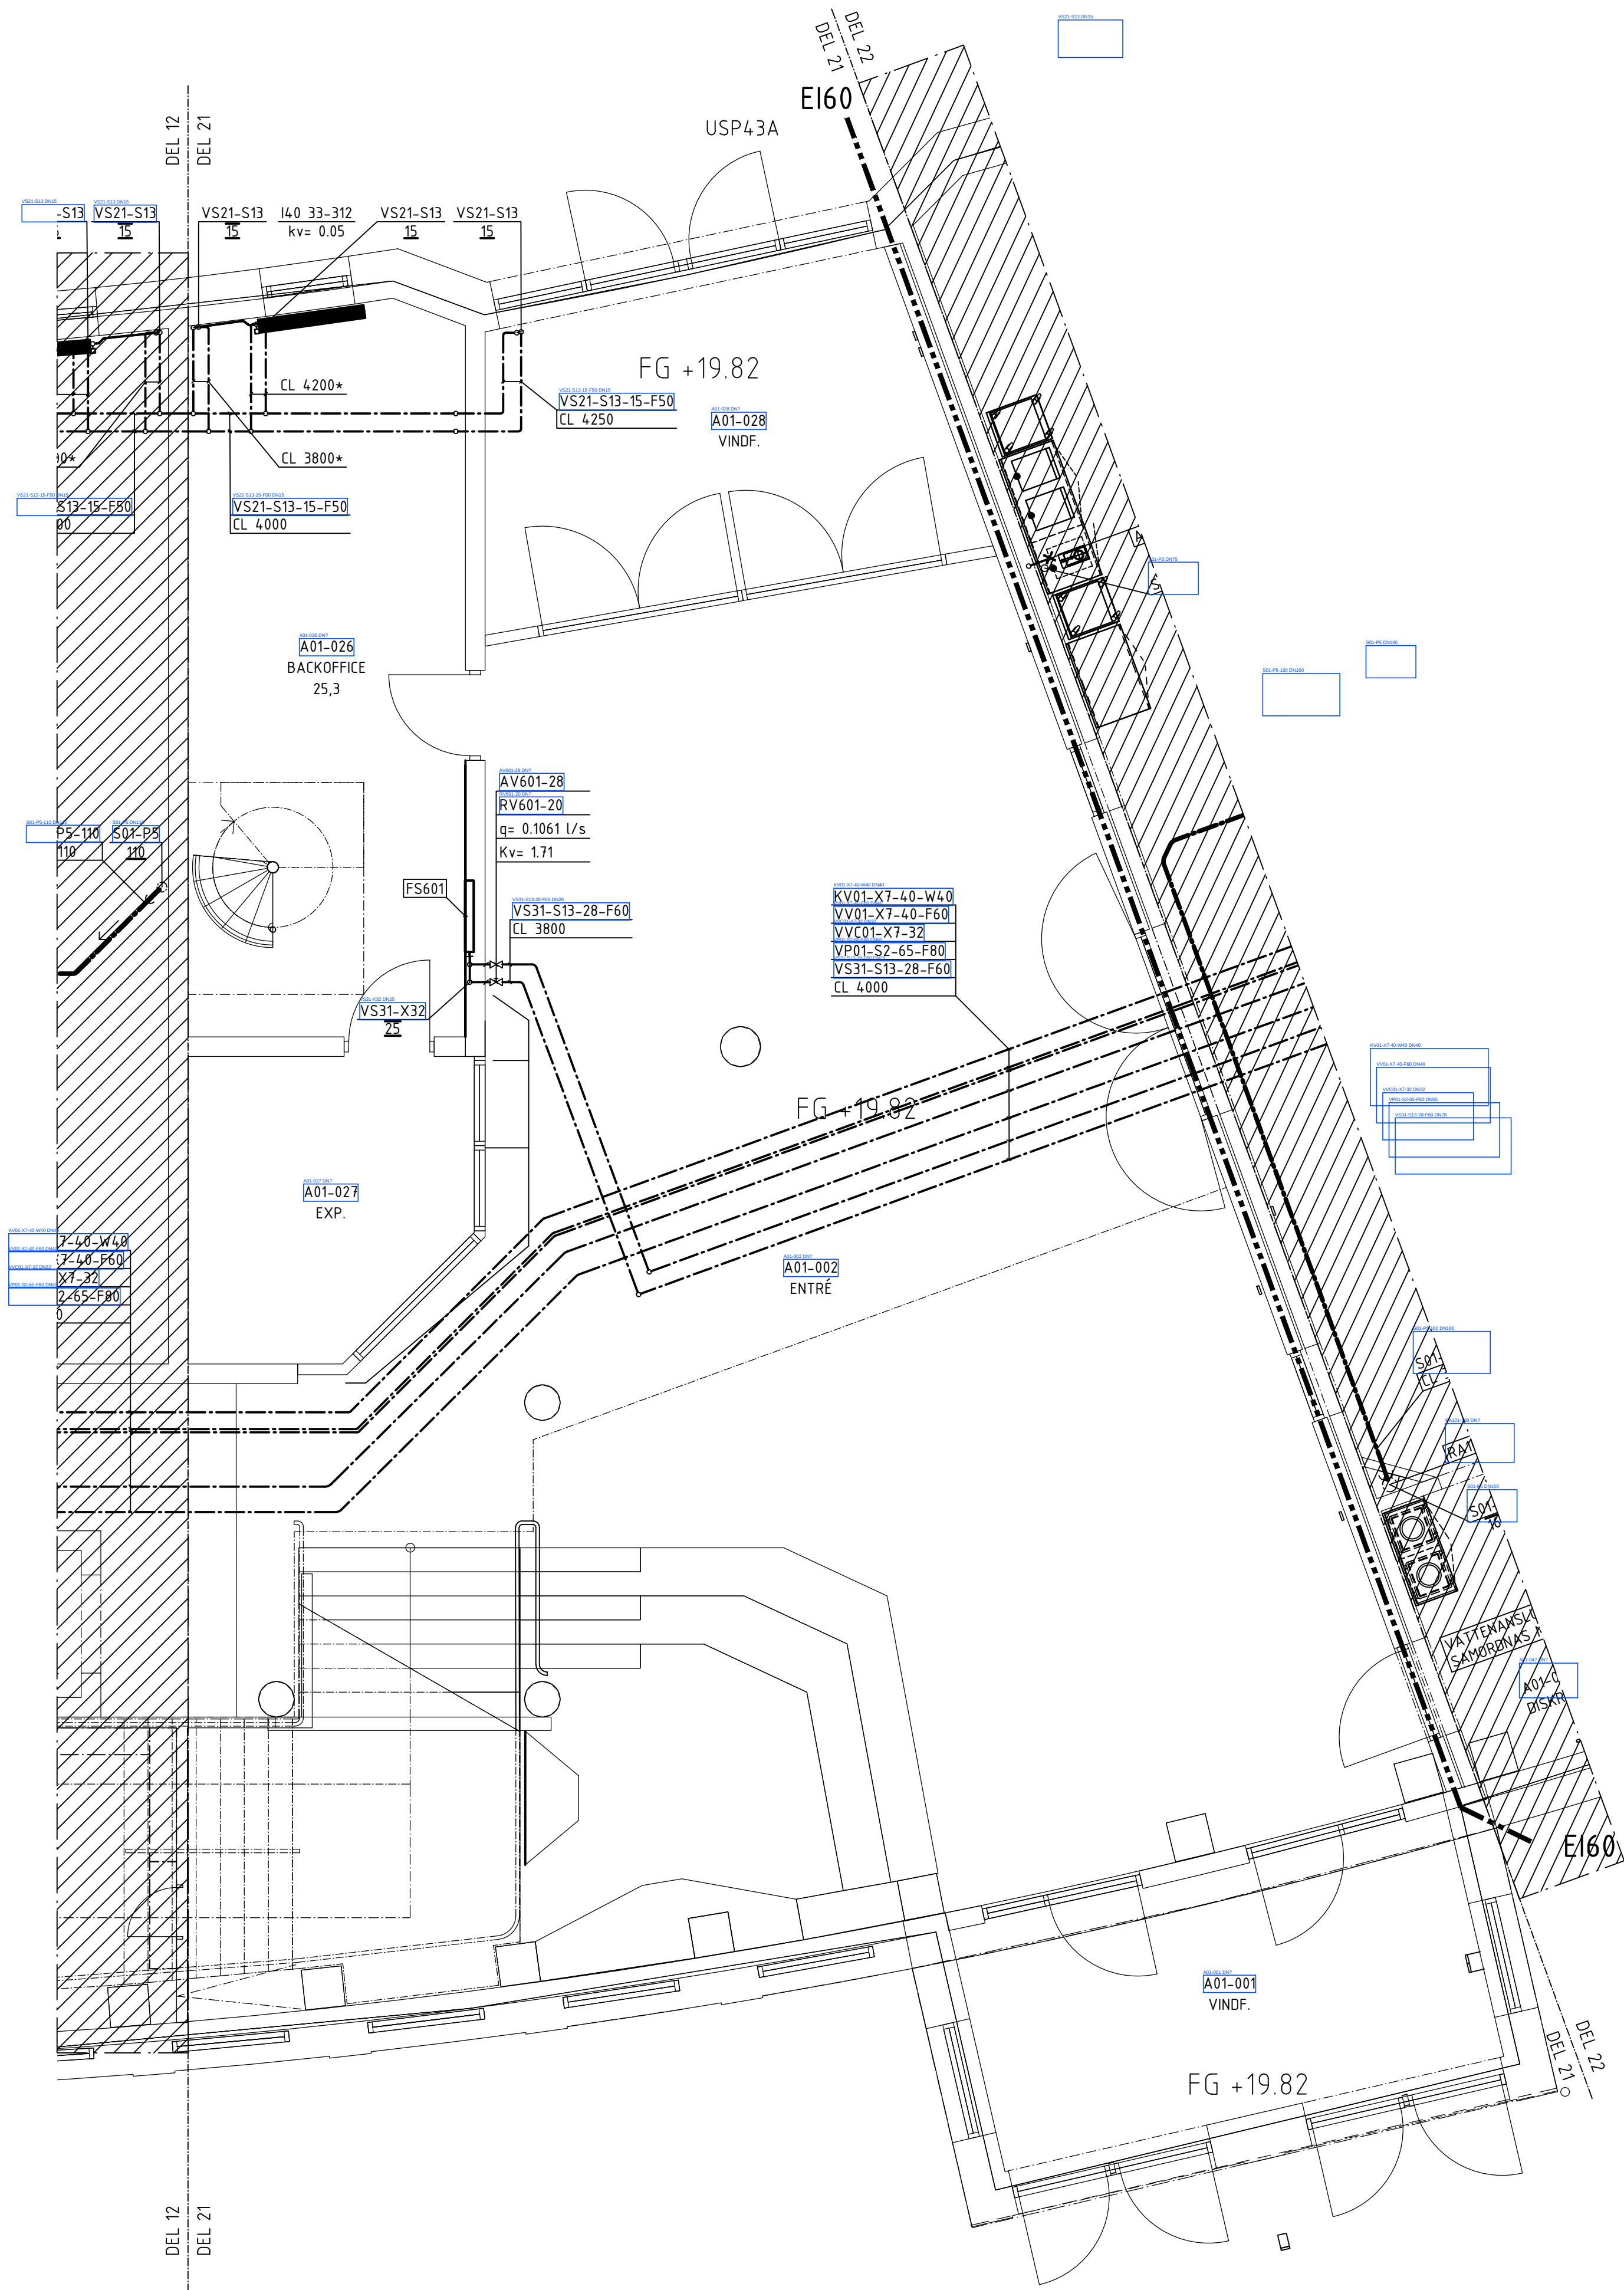

SKALA 1:50 (A1) 0 1 2 3 4 5

FÖRKLARINGAR

BETECKNING RÖRSYSTEM

VS11-S13-42-F100 - (100) mm (L-F) Ev. isolering. (42) Dimension (S13) Rörmaterial (11) Systemnummer (VS) Systembeteckning

TAPPVATTENSYSTEM

KV01 Tappkallvatten

KV02 Tappkallvatten, kombiugnar

VV01 Tappvarmvatten

VVC01 Varmvattencirkulation

SPILLVATTENSYSTEM

S01 Spillvatten

SF01 Spillvatten, fettavskiljare

S01 Fall min: 1%

SF01 Fall min: 2%

VÄRMEVATTENSYSTEM

FJV01 Fjärrvärme

VP01 Värmebärare, primär

VS11 Värmebärare, sekundär, ventilation

VS21 Värmebärare, sekundär, radiatorer

VS31 Värmebärare, sekundär, golvvärme

RÖRLEDNINGAR

G3 MA-rör

K5 Kopparrör.Frkr

P2 PP markavloppsror

P3 PP-rör (avlopp inomhus)

P5 PP-rör (avlopp inomhus luddämpat)

R2 Ledningar av syrafast stål

R10 Rostfritt avloppsror, muff

S2 Handelsstub, stål

S6 Tryckkärlsstål

S13 Presskopplingsrör utv förs

X7 PAL-RÖR

X31 PEX-RIR

X32 PEX-RIR, extraisolerade

ISOLERING AV INSTALLATIONER

-F Mineralull

-W Mineralull, diffusionstät

VV01 & VVC01 SAMISOLERAS

SAKVAROR

Enl. BESKRIVNING AVSEENDE

VÄRME- OCH SANITETSANLÄGGNING

HANDLINGSNUMMER 11.A.2.1

MÄRKNING AV STYRKOMPONENTER

Föregås av 1764-A-

ÖVRIGT

CL xxxx* = Samma rördimension som stick och isolering F50

KOPPLINGSLEDNINGAR

FRÅN FÖRDELARE TILL

APPARAT ENLIGT TABELL

OM INGET ANNAT ANGES

	VV01-X31	KV01-X31
BL	16	16
TS	16	16
UB	16	16
VK	16	16

A	O	PM1-W	230601	K. PERSSON
BET	ANT	ÄNDRINGEN AVSER	DATUM	SEN
BYGGHANDLING				
 Malmö stad Stadsfastigheter				
HYLLIE NYA HÖGSTADIUM OCH SPORTHALL 3 PROJEKT NR 30025113				
NYBYGGNAD AV SKOLA OCH SPORTHALL 5800				
 Sweco Sverige AB - Tele: 08-695 60 00 - www.sweco.se				
FORETAG	SWECO SVERIGE AB	TEL	040 - 16 70 00	
UPPDRAGSNUMMER	30025113	RITAD AV	K. PERSSON	HANDLAGARE
DATUM	2023-01-31	REV. DATUM	2023-06-01	ANSVARIG
				J. ÅKESSON
RUNDSTICKAN 1				
RÖRINSTALLATIONER				
HUS A PLAN 1 DEL 21				
OBJEKTSNUMMER	BYGGNAD	PLAN	DEL	UNDERGRUPP
1764	A	01	21	50
SKALA	RITINGSNUMMER	BET		
1:50	V-50-1-A0121	A		

FILE: .\1\SVK\SK-model\SK-46-P-0100-1764-A.dwg PROJECT: 30025113 HYLLIE_NYA_HOGSTADIUMSKOLA_00010 CAD: VAW-MODELLV-50-P-0100-1764-A.DWG PERSSON, KRISTOFFER