


XREF: .\1\SVK\SK-model\SK-46-P-0100-1764-A.dwg
.1\A.A-model\A-40-P-0100-1764-A.dwg
.1\A.A-model\orient\enrigsfig.dwg
.1\Slips\Slips - Skola.dwg

LAGER: SB11

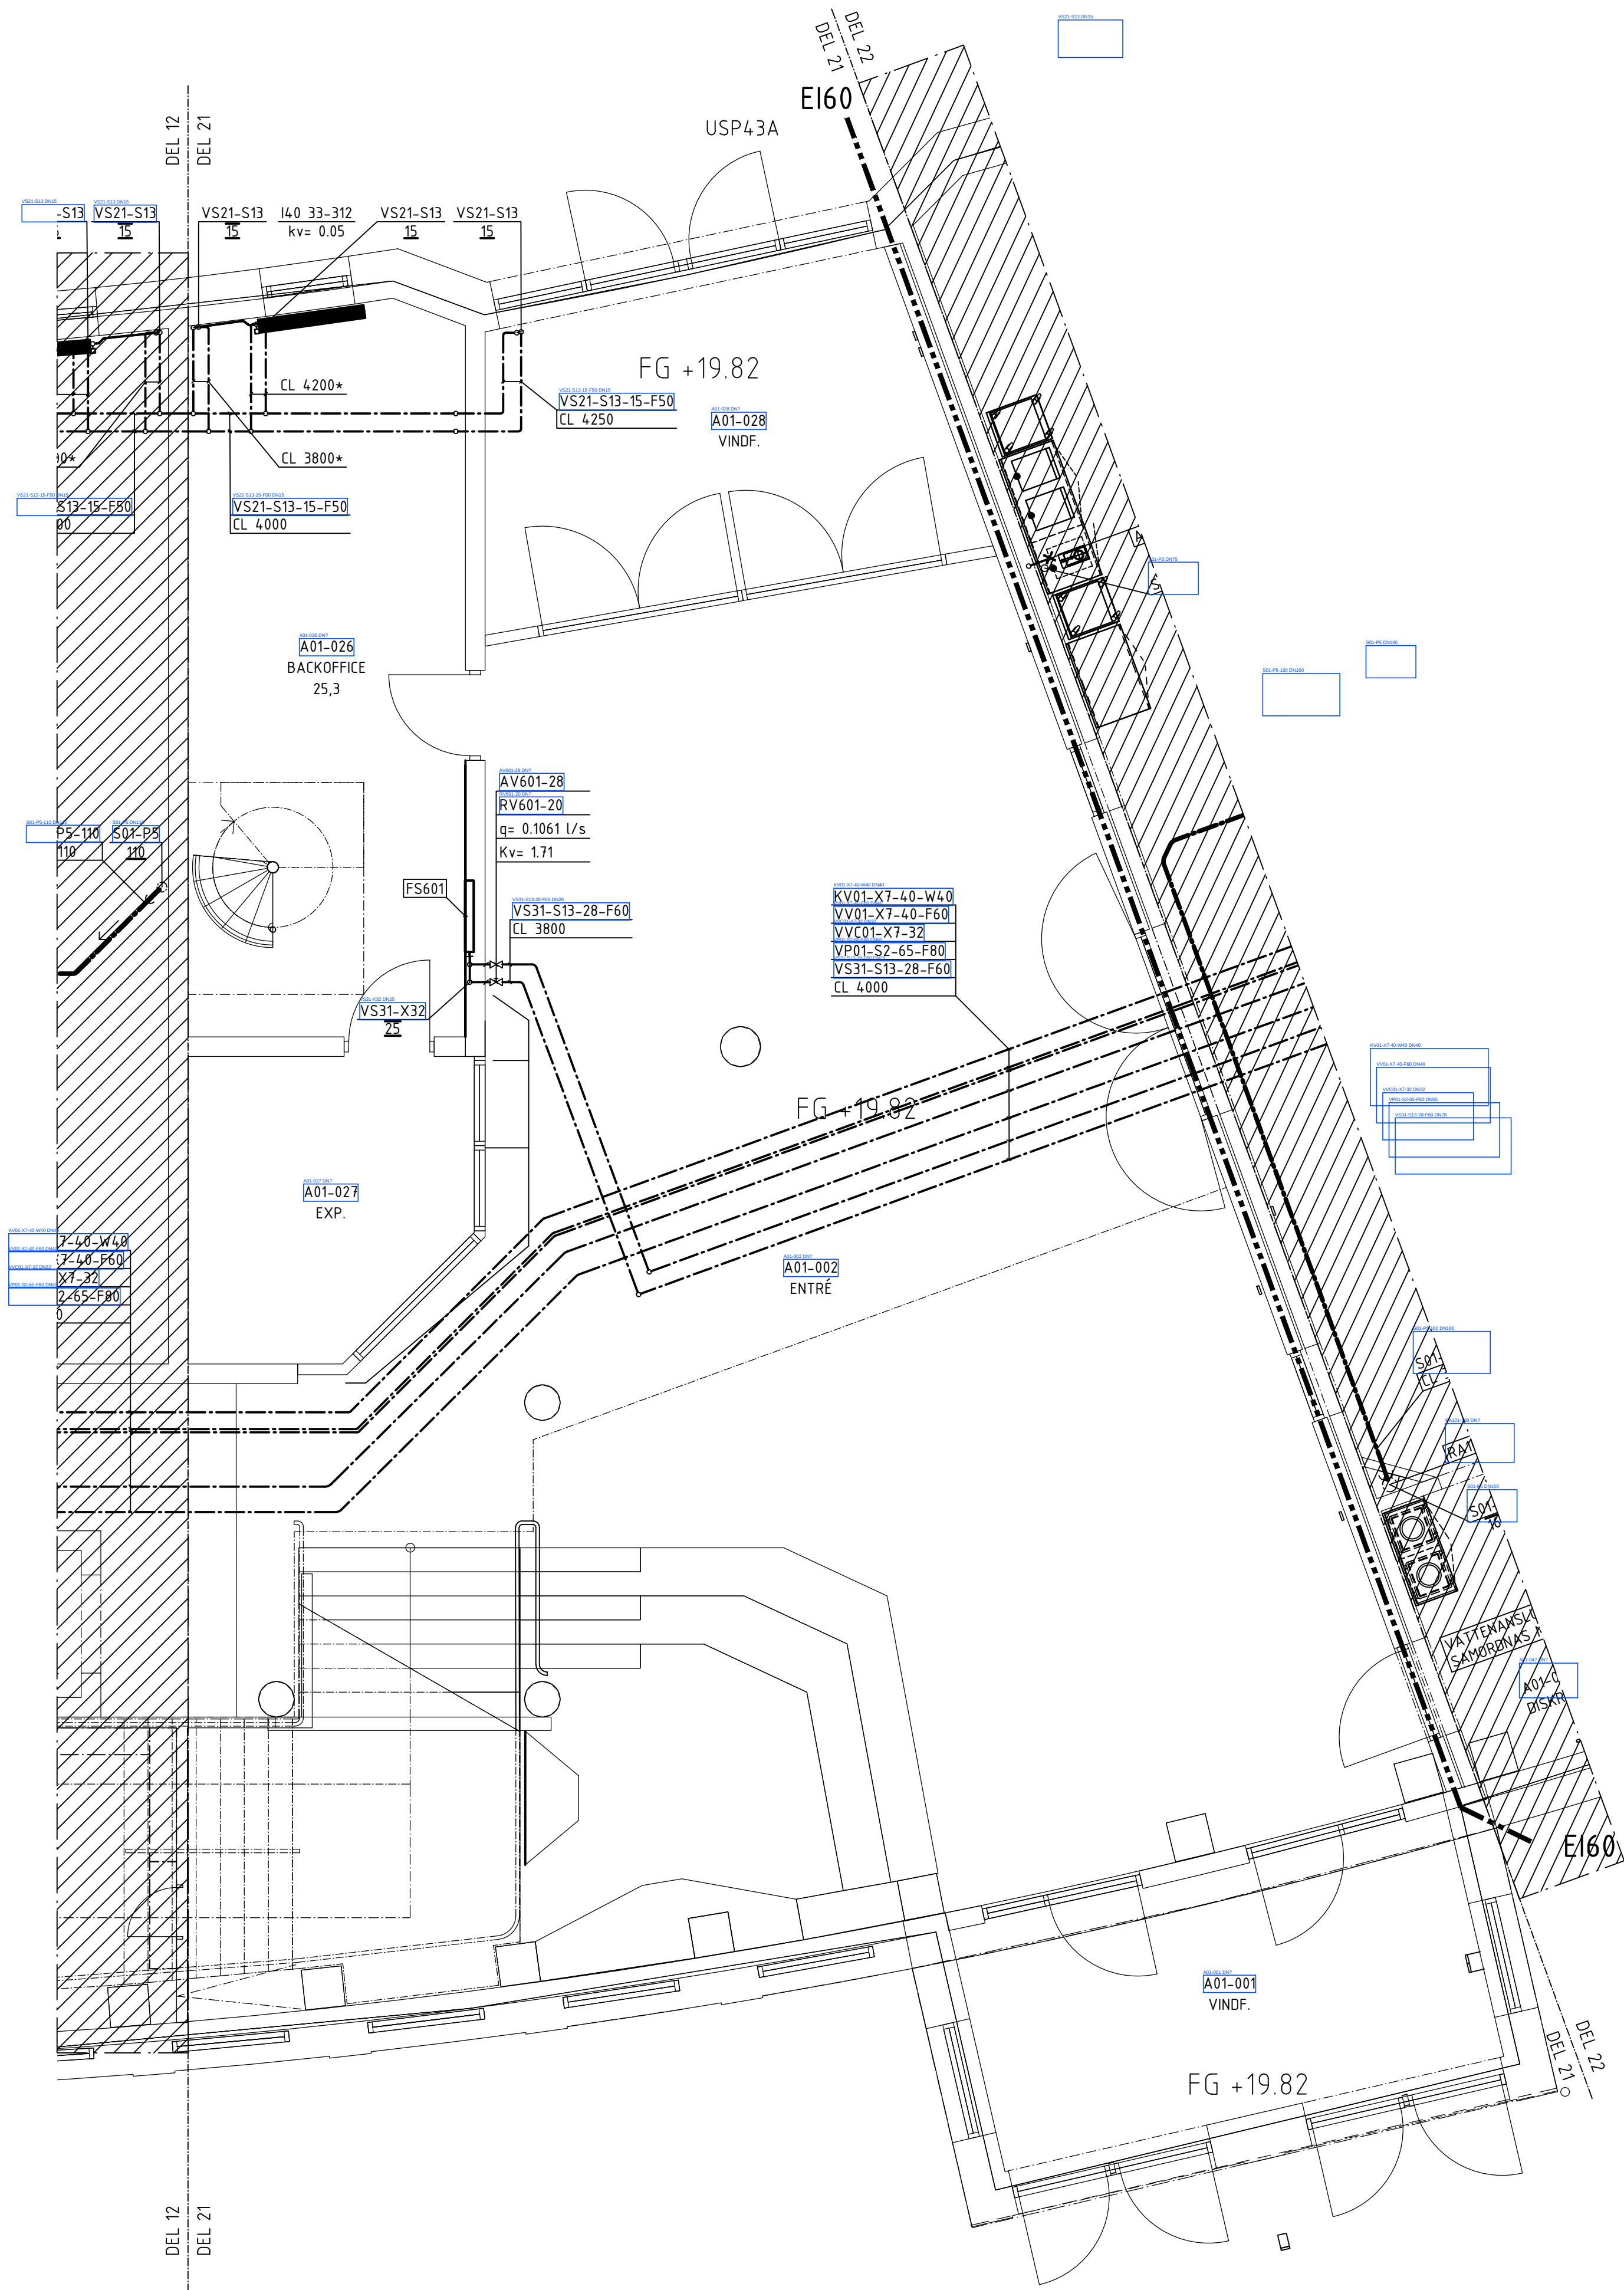

SKALA 1:50 (A1) 0 1 2 3 4 5

FÖRKLARINGAR
BETECKNING RÖRSYSTEM
VS11-S13-42-F100 - (100) mm
(L-F) Ev. isolering.
(42) Dimension
(S13) Rörmaterial
(11) Systemnummer
(VS) Systembeteckning

TAPPVATTENSYSTEM
KV01 Tappkallvatten
KV02 Tappkallvatten, kombiugnar
VV01 Tappvarmvatten
VVC01 Varmvattencirkulation

SPILLVATTENSYSTEM
S01 Spillvatten
SF01 Spillvatten, fettavskiljare

S01 Fall min: 1%
SF01 Fall min: 2%

VÄRMEVATTENSYSTEM
FJV01 Fjärrvärme
VP01 Värmebärare, primär
VS11 Värmebärare, sekundär, ventilation
VS21 Värmebärare, sekundär, radiatorer
VS31 Värmebärare, sekundär, golvvärme

RÖRLEDNINGAR
G3 MA-rör
K5 Kopparrör.Frkr
P2 PP markavloppsror
P3 PP-rör (avlopp inomhus)
P5 PP-rör (avlopp inomhus luddämpat)
R2 Ledningar av syrafast stål
R10 Rostfritt avloppsror, muff
S2 Handstubb, stål
S6 Tryckkärlsstål
S13 Presskopplingsrör utv förs
X7 PAL-RÖR
X31 PEX-RIR
X32 PEX-RIR, extraisolerade

ISOLERING AV INSTALLATIONER
-F Mineralull
-W Mineralull, diffusionstät

VV01 & VVC01 SAMISOLERAS

SAKVAROR
Enl. BESKRIVNING AVSEENDE
VÄRME- OCH SANITETSANLÄGGNING
HANDLINGSNUMMER 11.A.2.1


MÄRKNING AV STYRKOMPONENTER
Föregås av 1764-A-

ÖVRIGT
CL xxxx* = Samma rördimension som
stick och isolering F50

KOPPLINGSLEDNINGAR
FRÅN FÖRDELARE TILL
APPARAT ENLIGT TABELL
OM INGET ANNAT ANGES

	VV01-X31	KV01-X31
BL	16	16
TS	16	16
UB	16	16
VK	16	16

A	0	PM1-W	230601	K. PERSSON
BET	ANT	ÄNDRINGEN AVSER	DATUM	SEN
BYGGHANDLING				
 Malmö stad Stadsfastigheter				
HYLLIE NYA HÖGSTADIUM OCH SPORTHALL 3 PROJEKT NR 30025113 NYBYGGNAD AV SKOLA OCH SPORTHALL 5800				
 Sweco Sverige AB - Tele: 08-695 60 00 - www.sweco.se				
FORETAG	SWECO SVERIGE AB	TEL	040 - 16 70 00	
UPPGRADESNUMMER	30025113	RITAD AV	K. PERSSON	HANDLAGARE
DATUM	2023-01-31	REV. DATUM	2023-06-01	ANSVARIG
J. ÅKESSON				
RUNDSTICKAN 1 RÖRINSTALLATIONER HUS A PLAN 1 DEL 21				
OBJEKTSNUMMER	BYGGNAD	PLAN	DEL	UNDERGRUPP
1764	A	01	21	50
SKALA	RITINGSNUMMER	BET		
1:50	V-50-1-A0121	A		

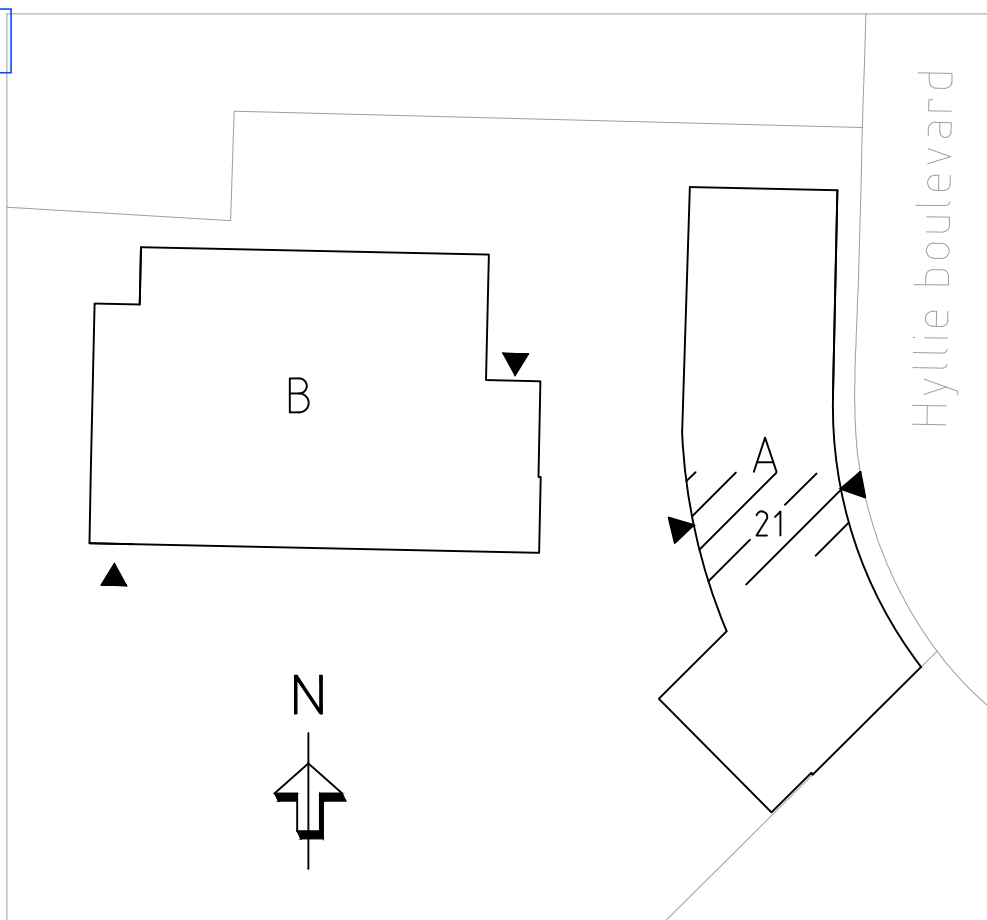

FILE: .\1\SVK\SK-model\SK-46-P-0100-1764-A.dwg PROJECT: 30025113 HYLLIE NYA HÖGSTADIUM OCH SPORTHALL 30025113 FILE: .\1\SVK\SK-model\SK-46-P-0100-1764-A.dwg PROJECT: 30025113