


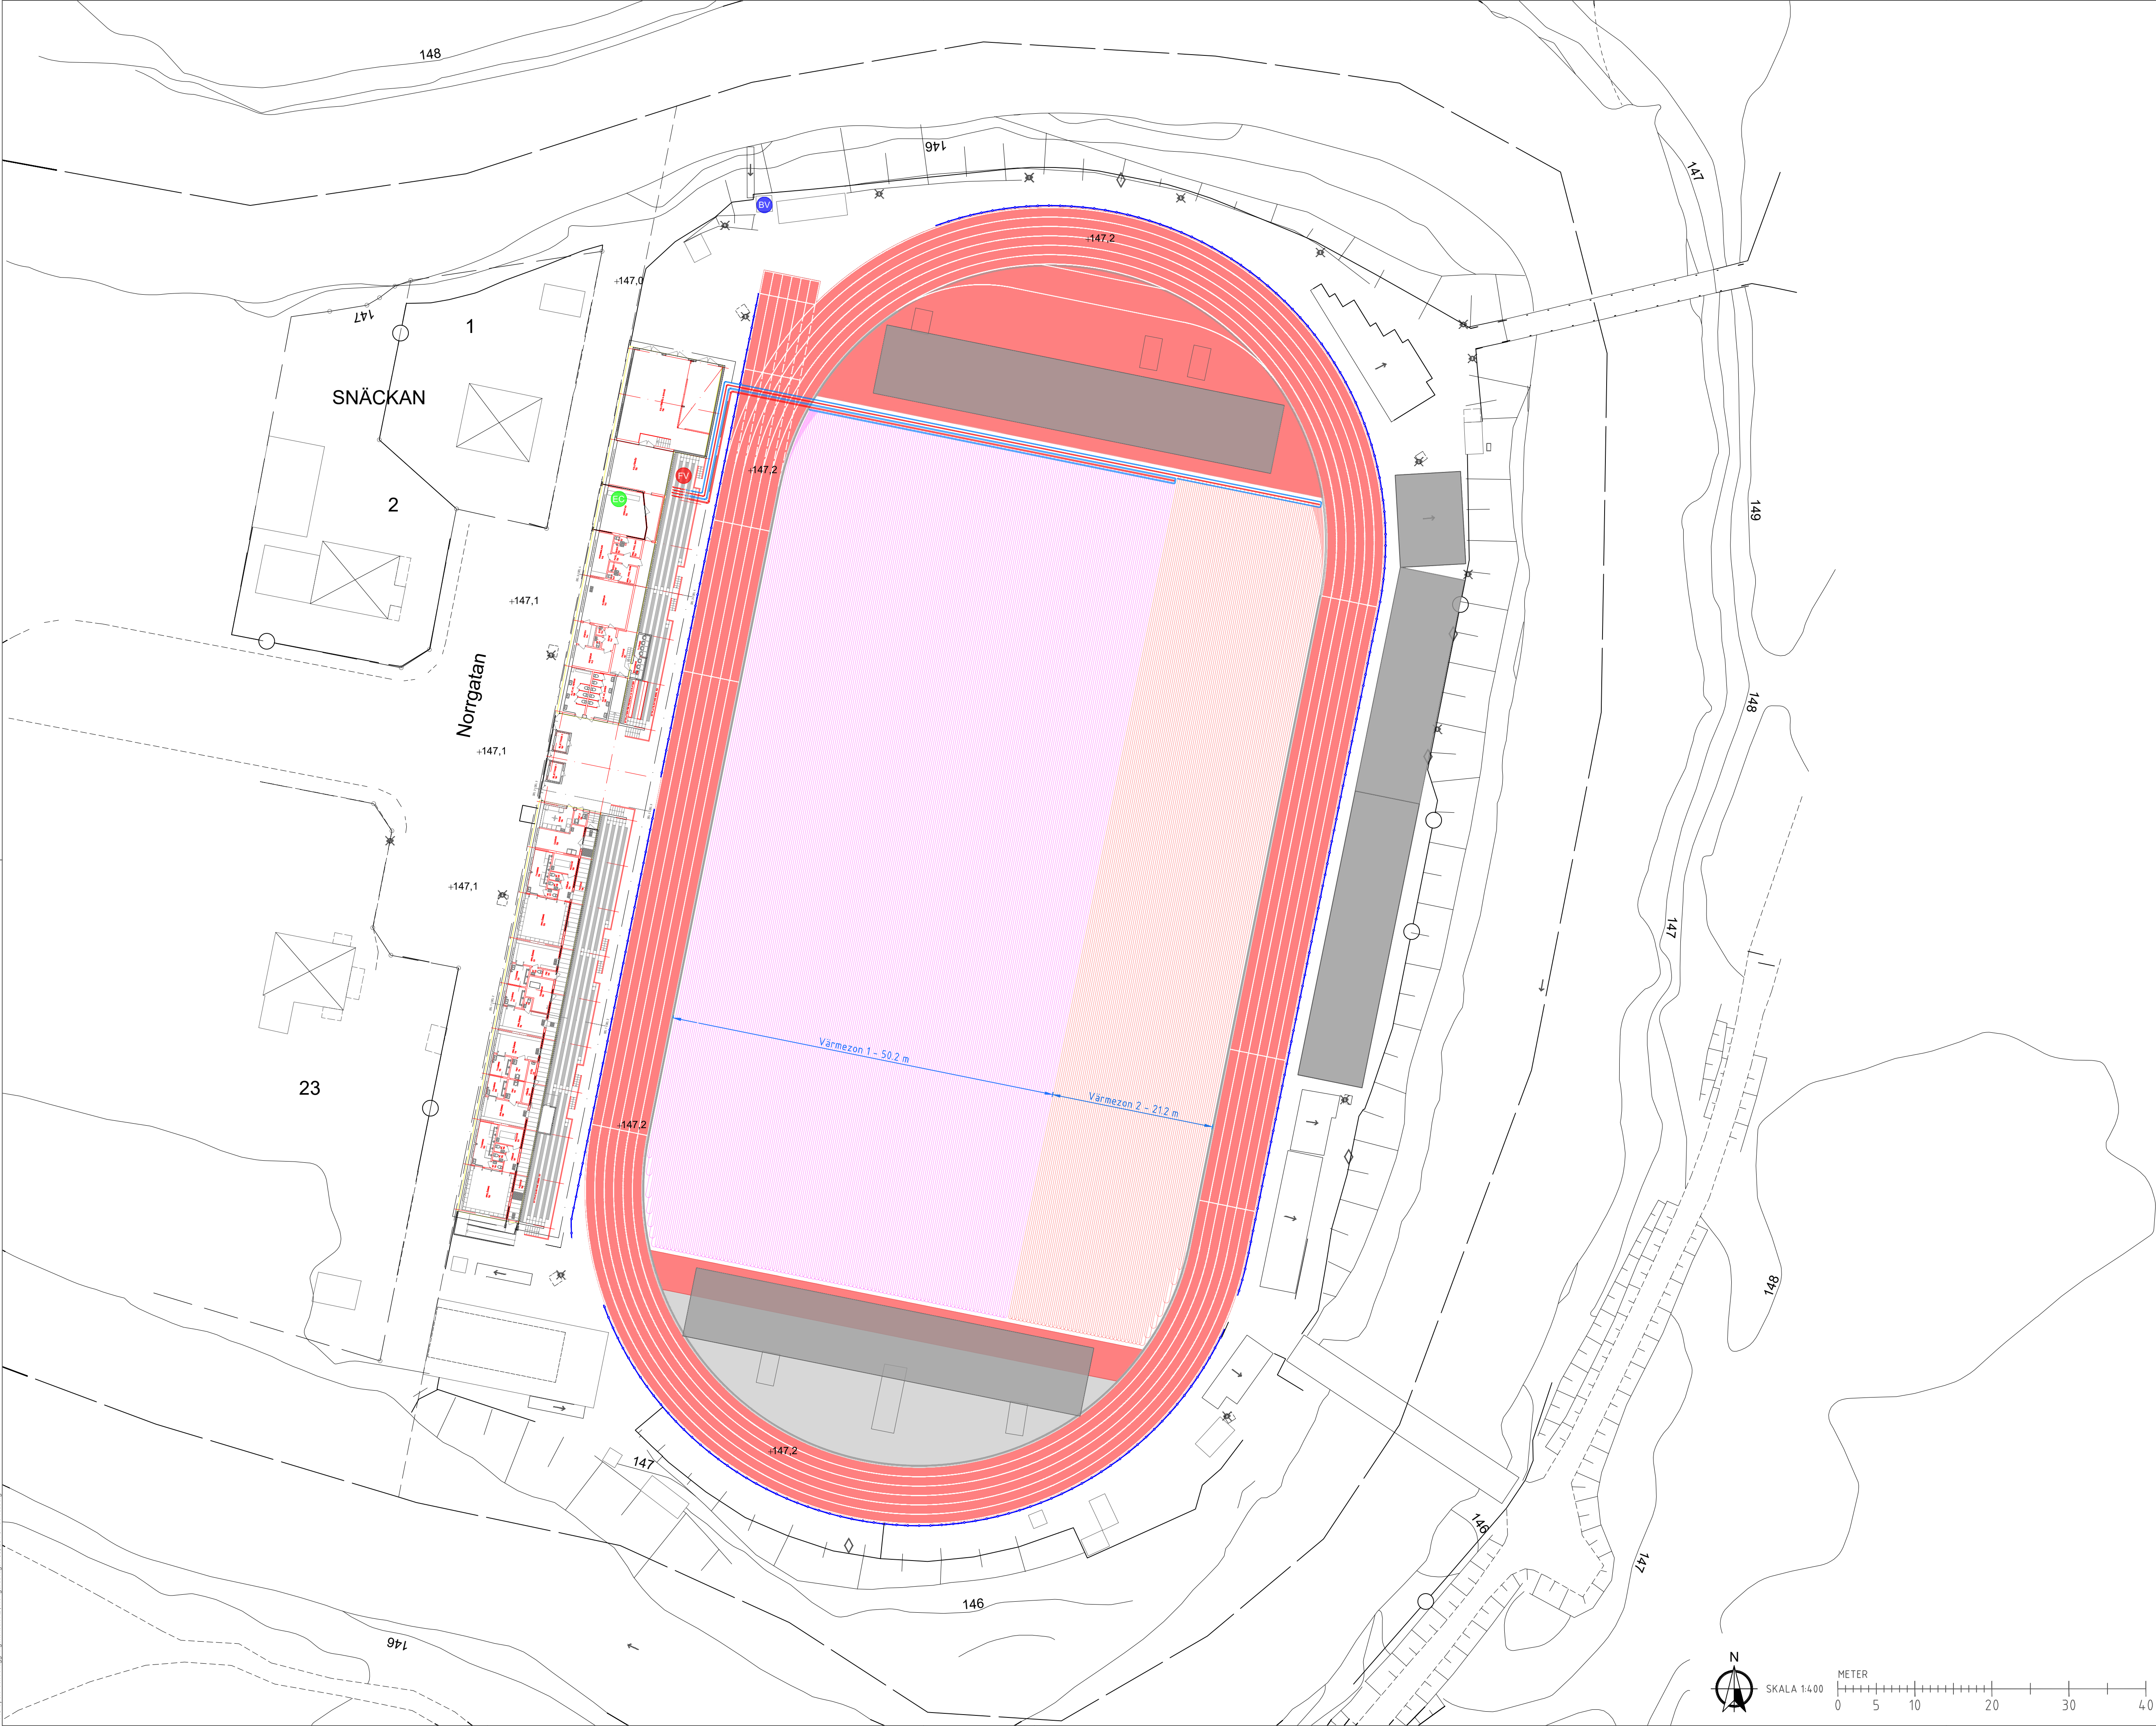

FÖRKLARINGAR

- Arbetsområde
- Räcke
- Nytt skåp med eluttag
- Bevatningspump
- Ny fjärrvärmecentral
- Befintlig elcentral

BET		ANT	ÄNDRINGEN AVSER	DATUM	SIGN
HANDLINGSTYP FÖRFRÅGNINGSUNDERLAG					
PROJEKTENÄMNING MARKVÄRME OCH HYBRIDGRÄSPLAN					
UPPDRAGSGIVARE  VÄRNAMO KOMMUN					
A0 Sport- och Anläggningskonsult AB Mob. 070-376 17 45 E-post: anders@sportanlaggning.se				• Projektleddning • Alliansledning • Offentlig upphandling • Rättshänsyn • Beskrivningar • Bygghandlingar	
UPPDRAG NR		RITAD/KONSTR AV A0		PROJEKTNUMMER	
DATUM 2026-03-05		ANSVARIG		DISCIPLIN	
MARKVÄRME OCH HYBRIDGRÄSPLAN FINNVEDSVÄLLEN VÄRNAMO					
MARKVÄRMESYSTEM I MARK					
FORMAT	SKALA	RITNINGSNR			REV
A1	1:400	M-10-1-002			