


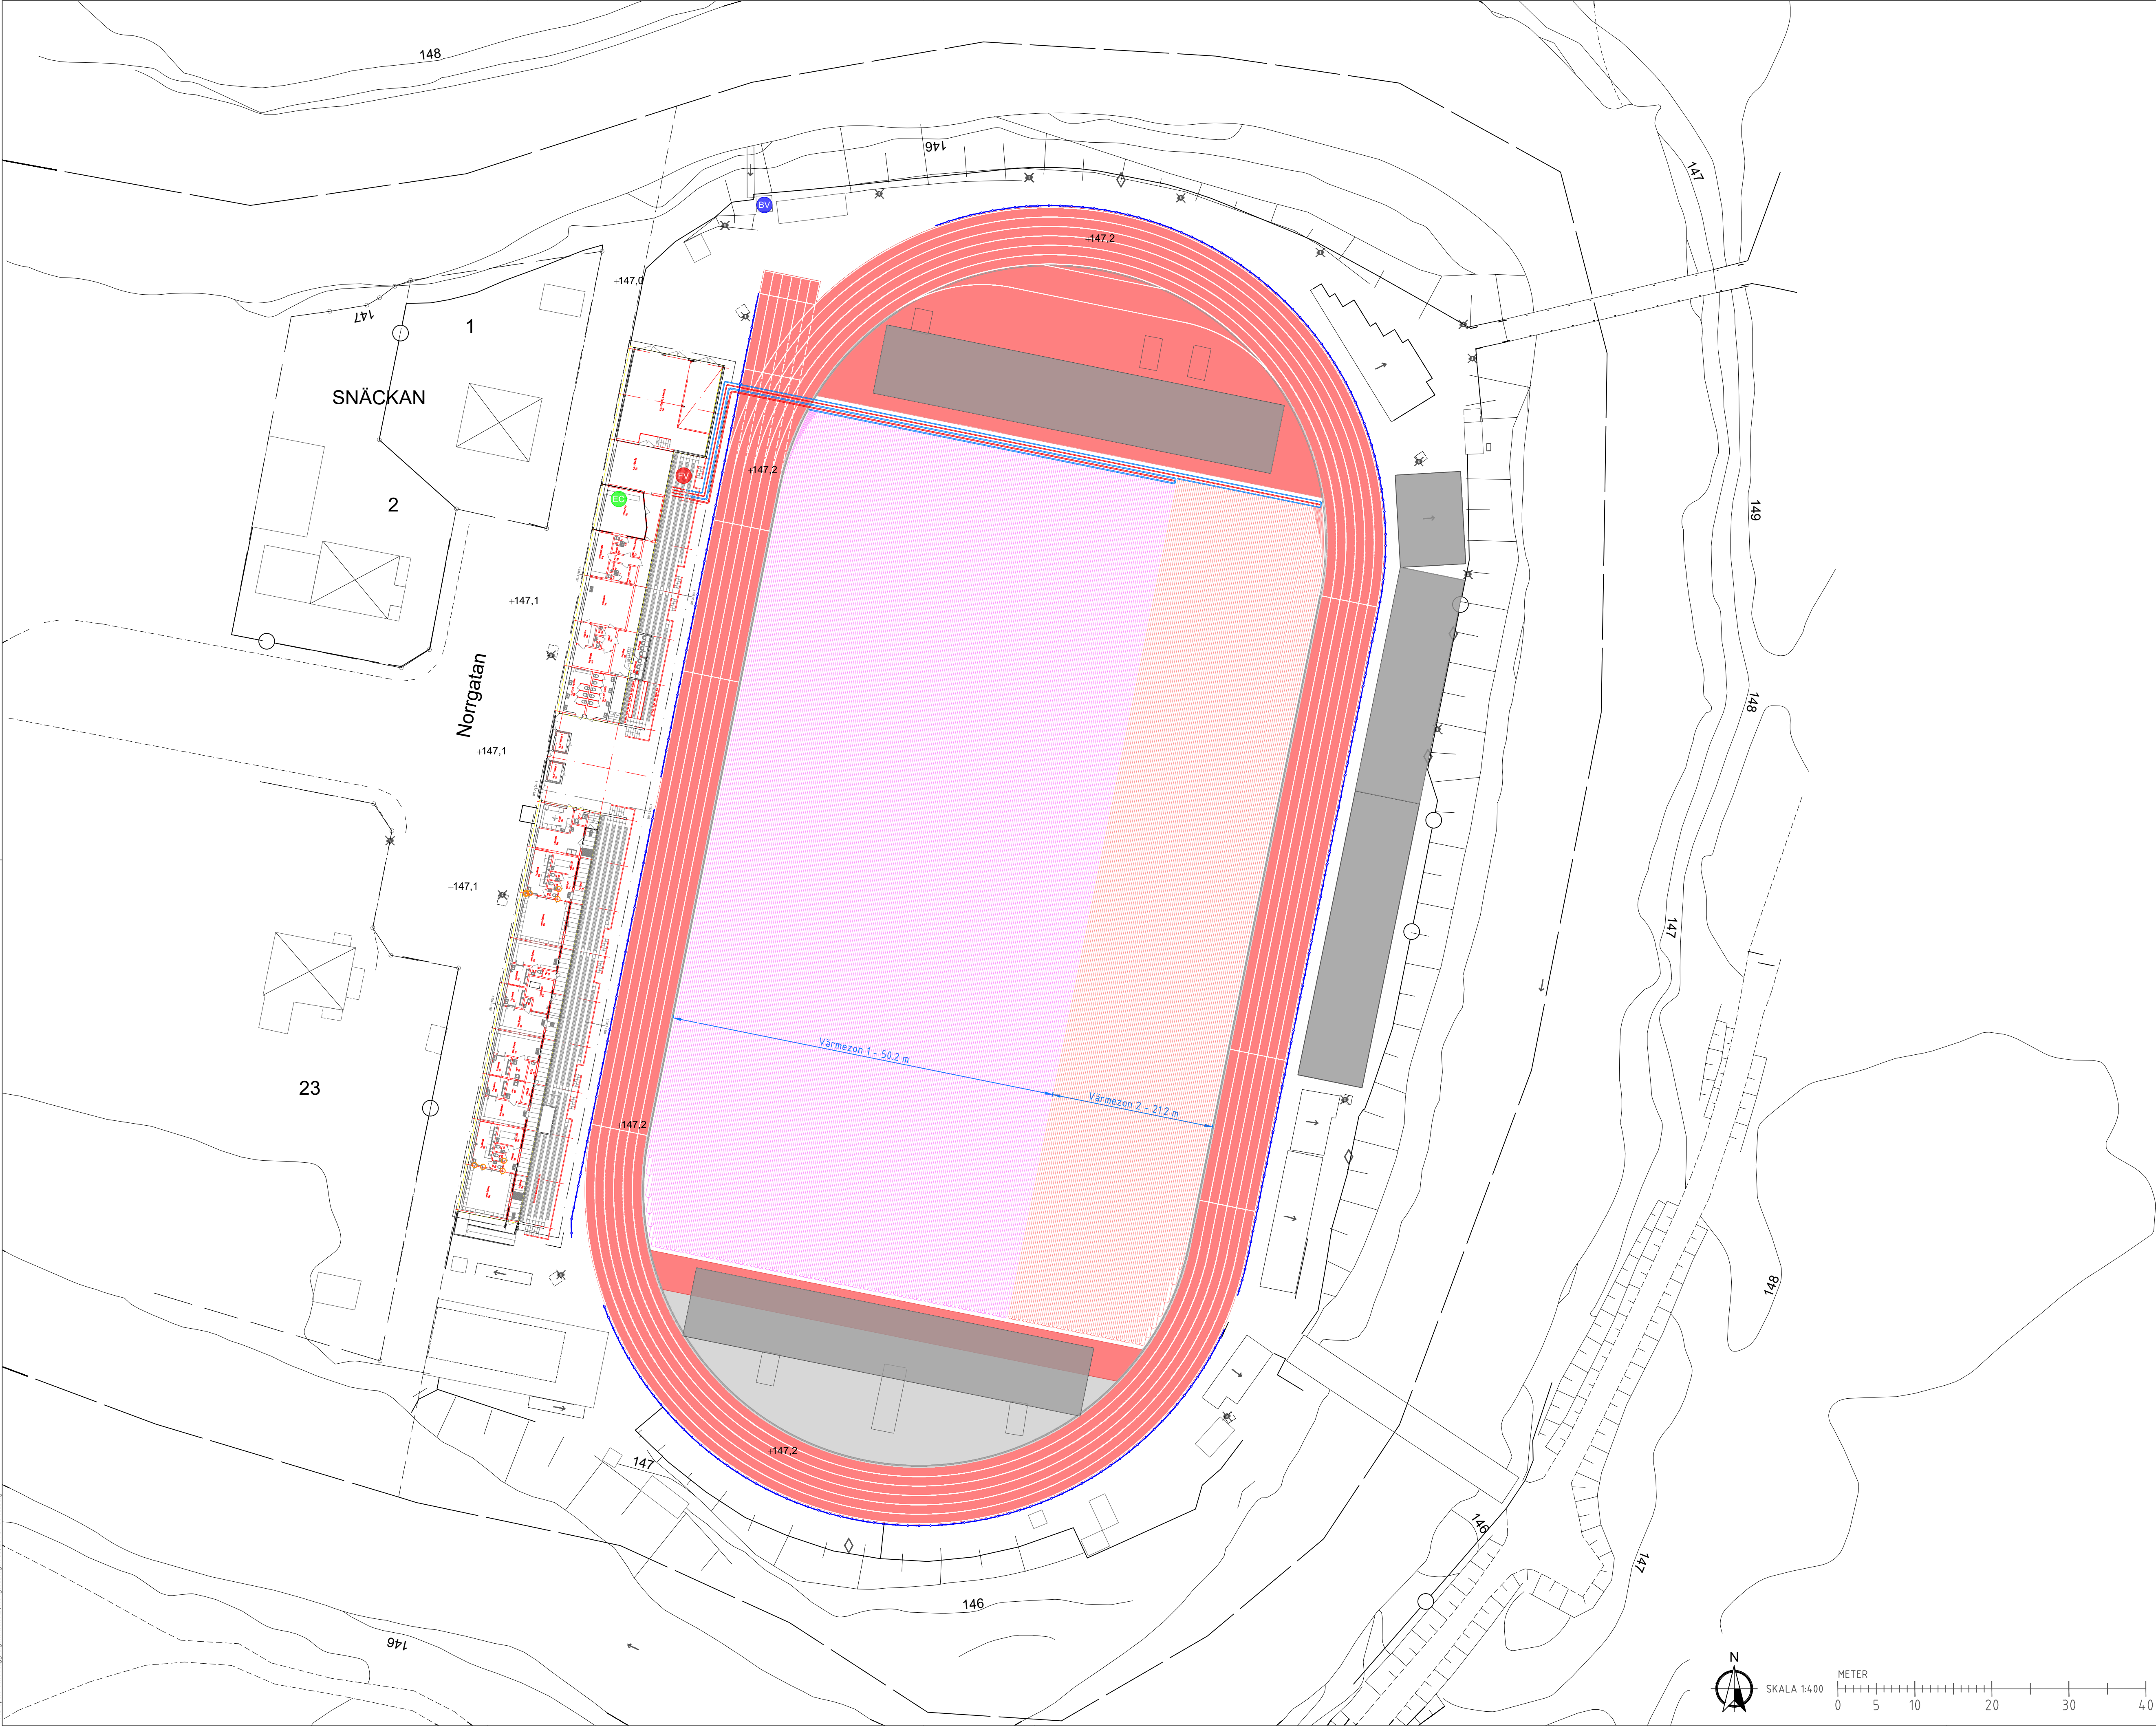

FÖRKLARINGAR

- Arbetsområde
- Räcke
- Nytt skåp med eluttag
- Bevatningspump
- Ny fjärrvärmecentral
- Befintlig elcentral

BET		ANT	ÄNDRINGEN AVSER	DATUM	SIGN
HANDLINGSTYP					
FÖRFRÅGNINGSUNDERLAG					
PROJEKTENÄMNING					
MARKVÄRME OCH HYBRIDGRÄSPLAN					
UPPDRAGSGIVARE					
			VÄRNAMO KOMMUN		
A0 Sport- och Anläggningskonsult AB Mob. 070-376 17 45 E-post: anders@sportanlaggning.se			• Projektleddning • Alliansledning • Offentlig upphandling • Rättshandling • Besiktningar • Bygghandlingar		
UPPDRAG NR		RITAD/KONSTR AV		PROJEKTNUMMER	
2026-03-05		A0			
DATUM		ANSVARIG		DISCIPLIN	
2026-03-05					
MARKVÄRME OCH HYBRIDGRÄSPLAN FINNVEDSVÄLLEN VÄRNAMO					
MARKVÄRMESYSTEM I MARK					
FORMAT SKALA		RITNINGSR		REV	
A1 1:400		M-10-1-002			