


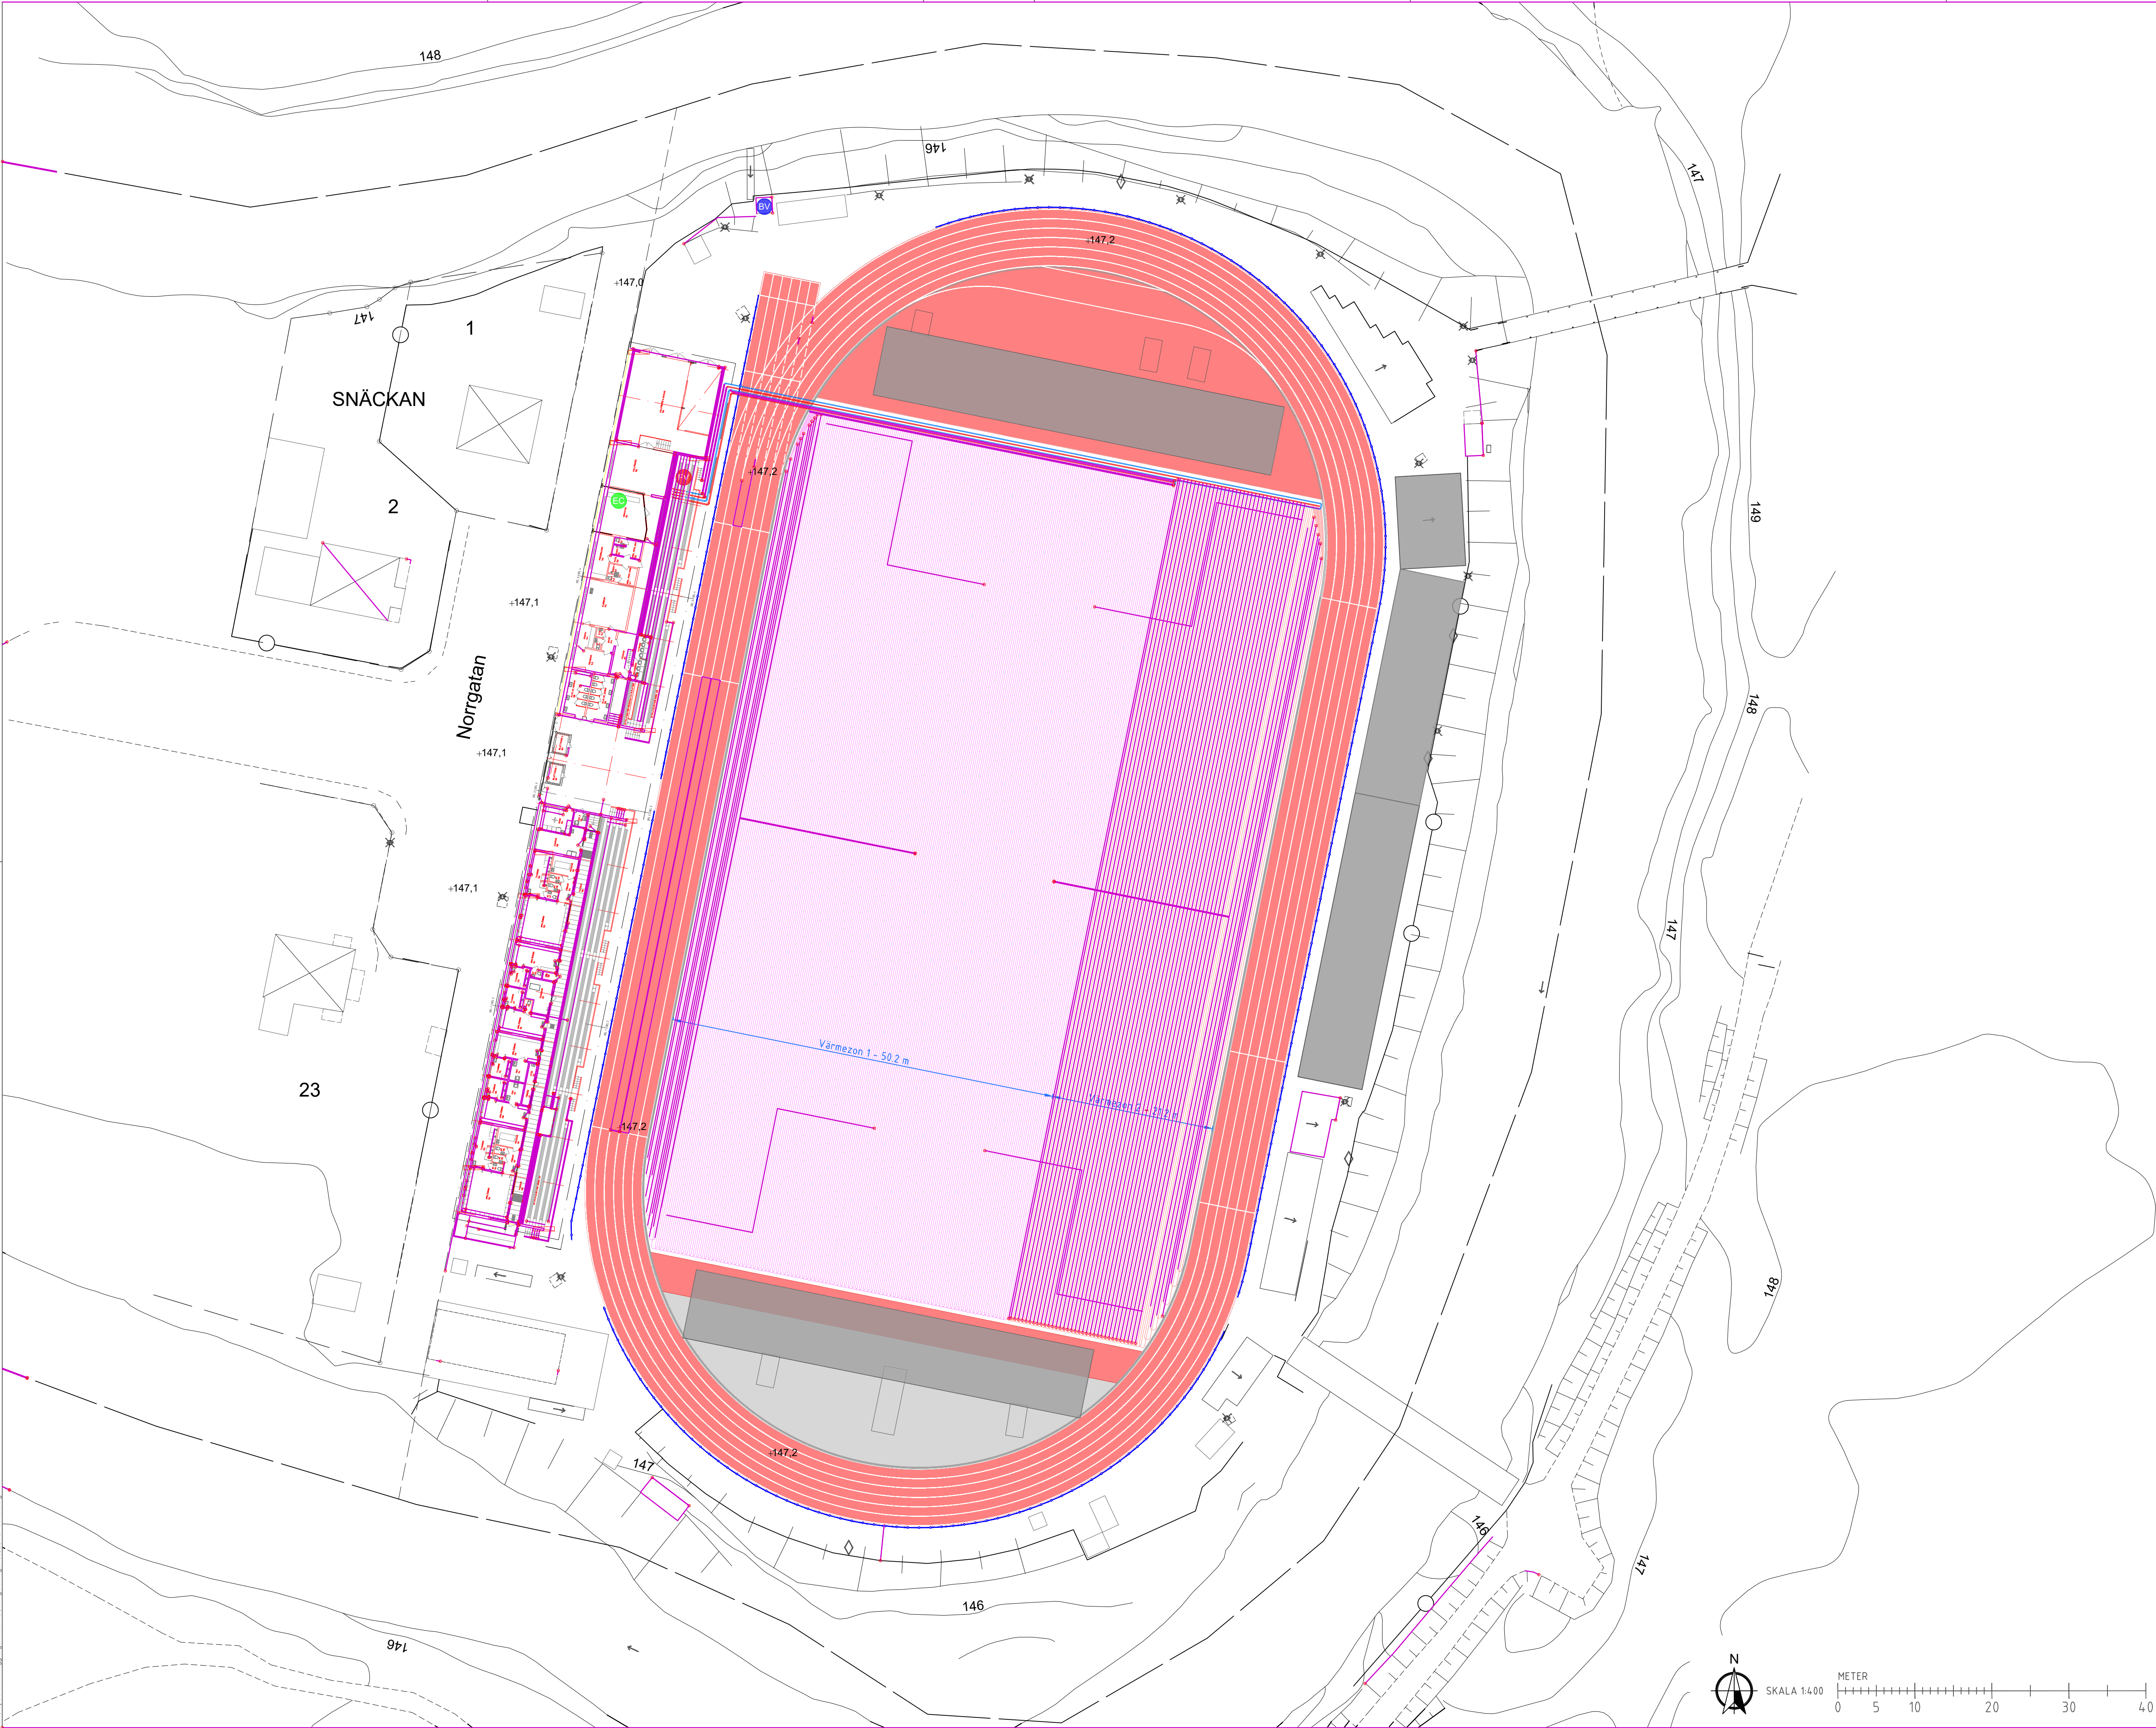

FÖRKLARINGAR

- Arbetsområde
- Räcke
- Nytt skåp med eluttag
- Bevakningspump
- Ny fjärrvärmecentral
- Befintlig elcentral

BET	ANT	ÄNDRINGEN AVSER	DATUM	SIGN
HANDLINGSTYP				
FÖRFRÅGNINGSUNDERLAG				
PROJEKTENAMNING				
MARKVÄRME OCH HYBRIDGRÄSPLAN				
UPPDRAGSGIVARE				
 VÄRNAMO KOMMUN			• Projektleddning • Alliansledning • Offentlig upphandling • Rättshänsyn • Beskrivningar • Bygghandlingar	
A0 Sport- och Anläggningskonsult AB Mob. 070-376 17 45 E-post: anders@sportanlaggning.se			UPPDRAG NR	
DATUM			RITAD/KONSTR AV	
2026-03-05			A0	
ANSVARIG			PROJEKTNUMMER	
DISCIPLIN				
MARKVÄRME OCH HYBRIDGRÄSPLAN FINNVEDSVÄLLEN VÄRNAMO				
MARKVÄRMESYSTEM I MARK				
FORMAT	SKALA	RITNINGSNR		REV
A1	1:400	M-10-1-002		