


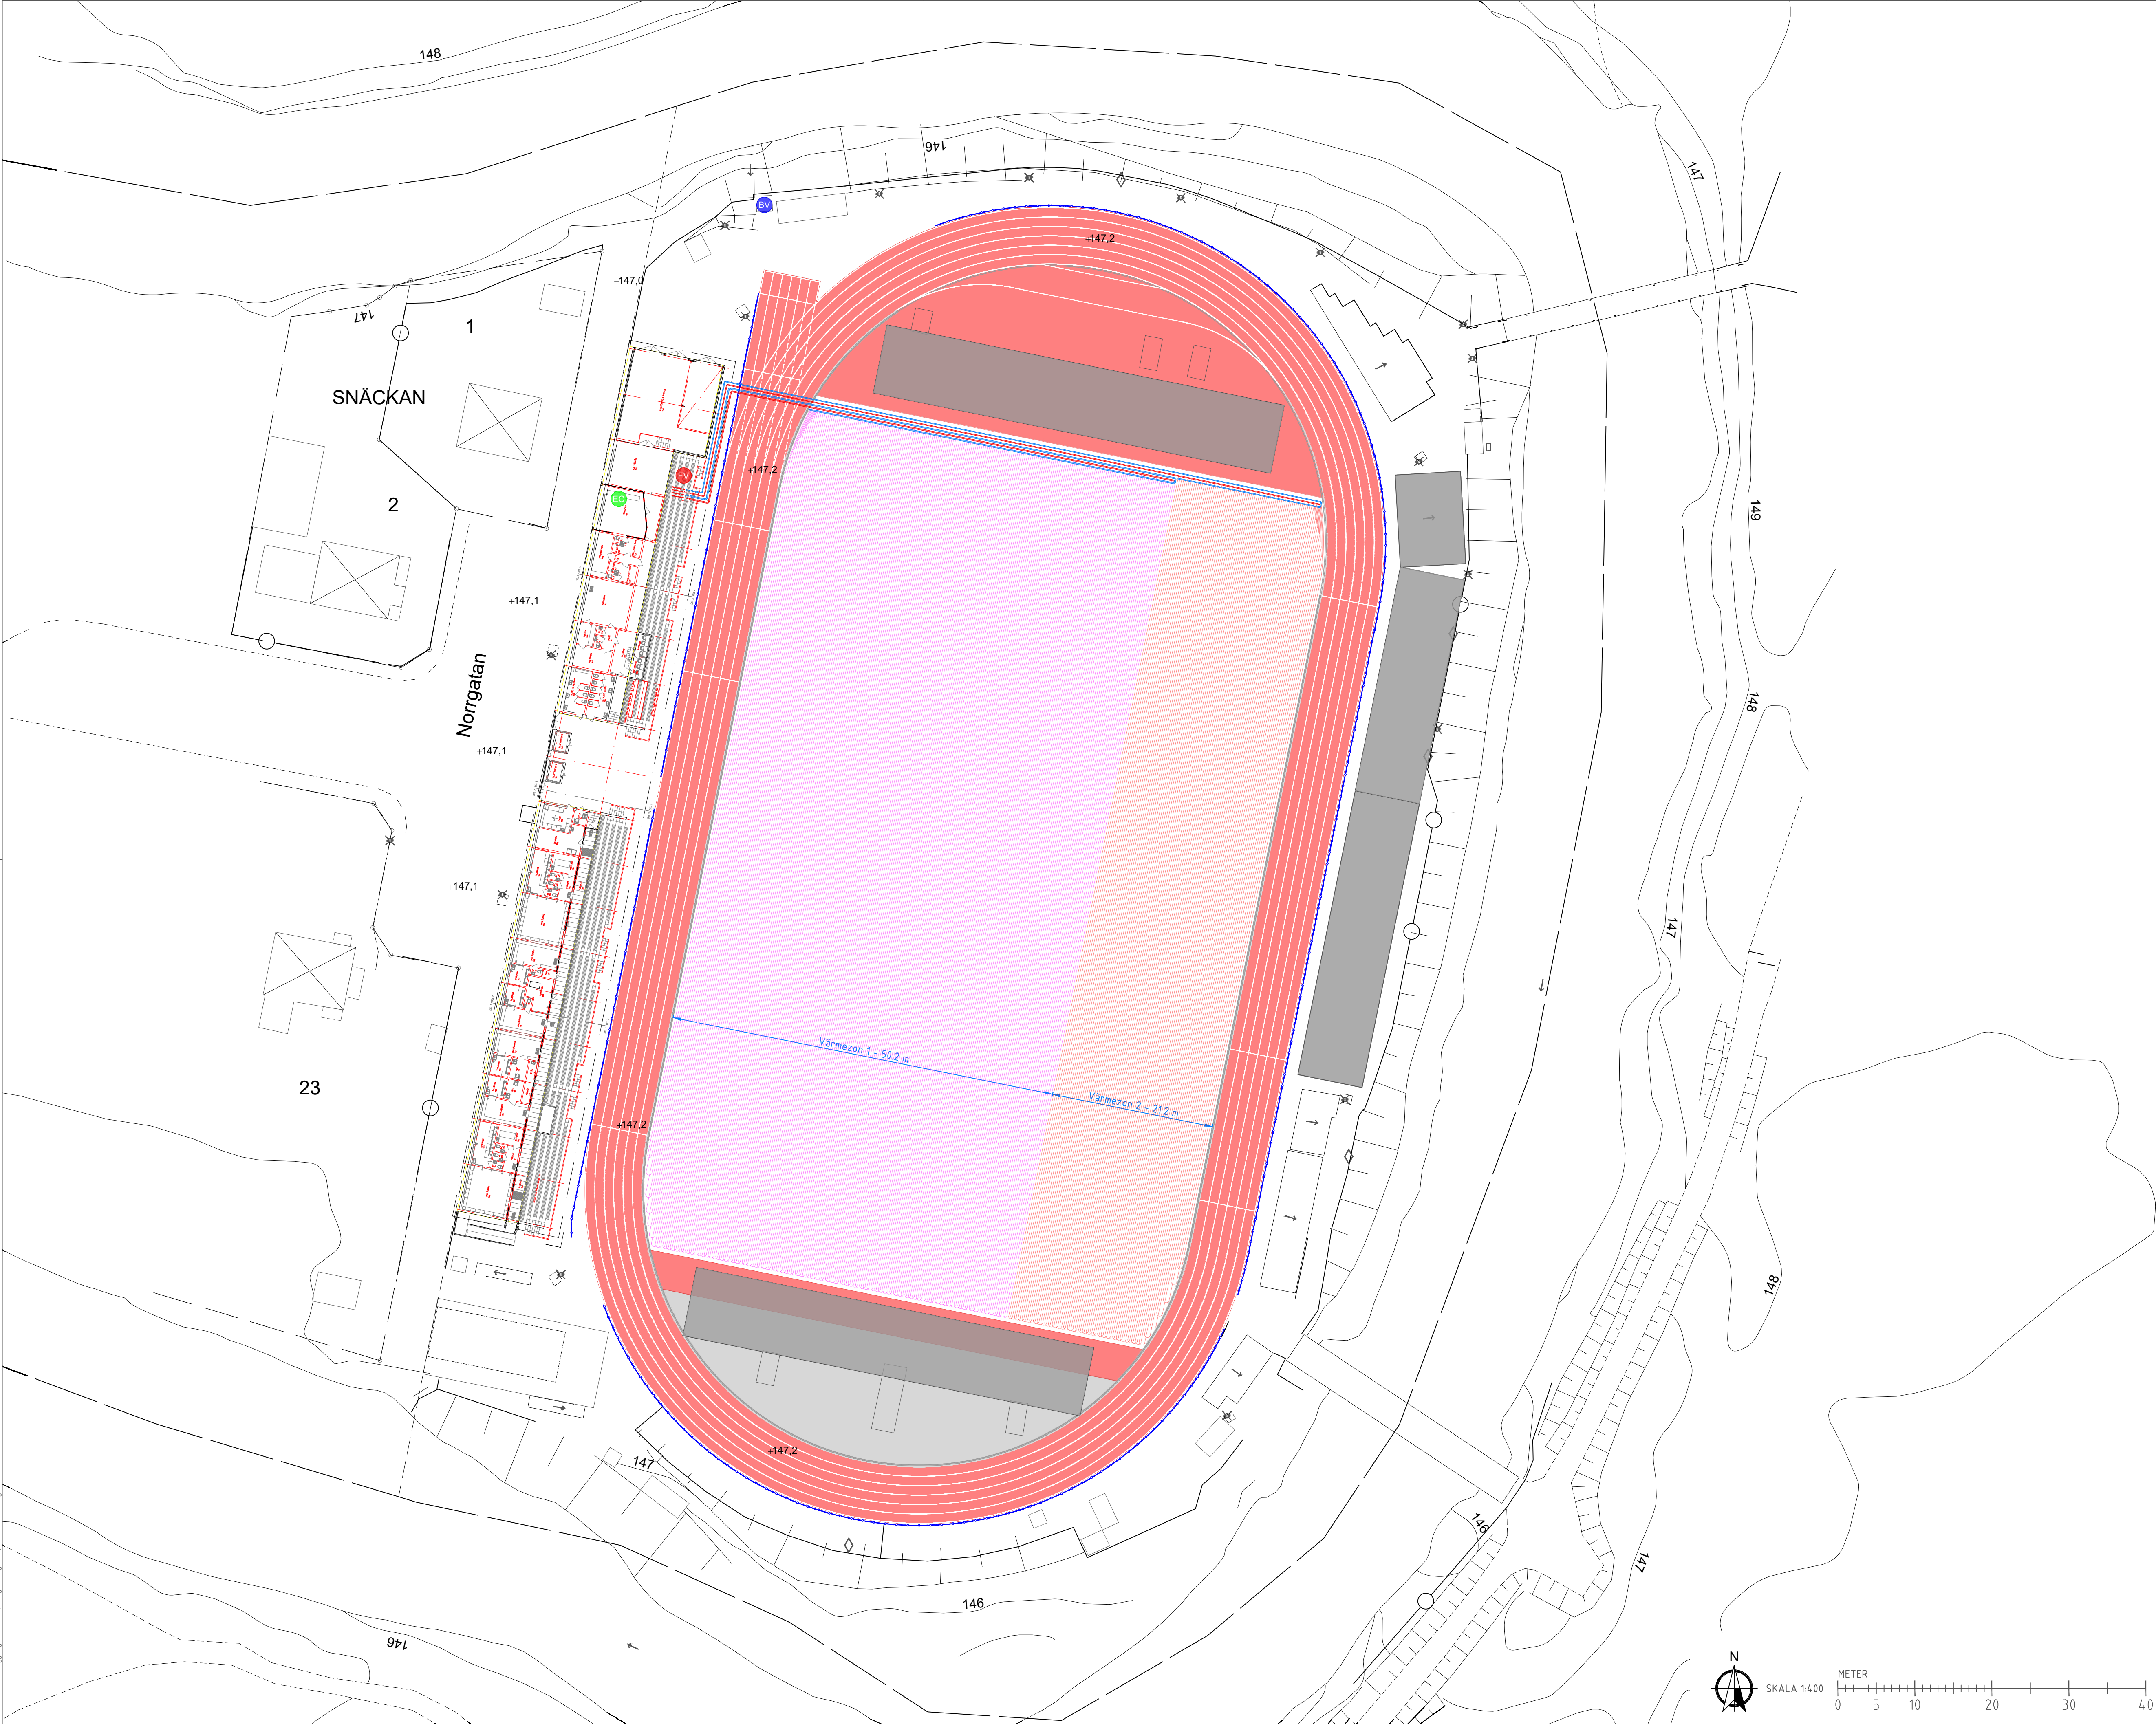

FÖRKLARINGAR

- Arbetsområde
- Räcke
- Nytt skåp med eluttag
- Bevattningspump
- Ny fjärrvärmecentral
- Befintlig elcentral

BET		ANT	ÄNDRINGEN AVSER	DATUM	SIGN	
HANDLUSTYP FÖRFRÅGNINGSUNDERLAG PROJEKTENÄMNING MARKVÄRME OCH HYBRIDGRÄSPLAN UPPDRAGSGIVARE  VÄRNAMO KOMMUN AO Sport- och Anläggningskonsult AB Mod. 070-376 17 45 E-post: anders@sporthandtagning.se • Projektledning • Alliansutveckling • Offentlig upphandling • Riksdagning • Besiktningar • Bygglösningar <tr><td colspan="2">UPPDRAG NR</td><td colspan="2">RITAD/KONSTR AV</td><td colspan="2">PROJEKTNUMMER</td></tr> <tr><td colspan="2">DATUM</td><td colspan="2">ANSVARIG</td><td colspan="2">DISCIPLIN</td></tr> <tr><td colspan="2">2026-03-05</td><td colspan="2"></td><td colspan="2"></td></tr> <tr><td colspan="6">MARKVÄRME OCH HYBRIDGRÄSPLAN</td></tr> <tr><td colspan="6">FINNVEDSVÄLLEN VÄRNAMO</td></tr> <tr><td colspan="6">MARKVÄRMESYSTEM I MARK</td></tr> <tr><td colspan="2">FORMAT</td><td colspan="2">SKALA</td><td colspan="2">RITNINGSNR</td></tr> <tr><td colspan="2">A1</td><td colspan="2">1:400</td><td colspan="2">M-10-1-002</td></tr> <tr><td colspan="4"></td><td colspan="2">REV</td></tr>						UPPDRAG NR		RITAD/KONSTR AV		PROJEKTNUMMER		DATUM		ANSVARIG		DISCIPLIN		2026-03-05						MARKVÄRME OCH HYBRIDGRÄSPLAN						FINNVEDSVÄLLEN VÄRNAMO						MARKVÄRMESYSTEM I MARK						FORMAT		SKALA		RITNINGSNR		A1		1:400		M-10-1-002						REV	
UPPDRAG NR		RITAD/KONSTR AV		PROJEKTNUMMER	
DATUM		ANSVARIG		DISCIPLIN	
2026-03-05	
MARKVÄRME OCH HYBRIDGRÄSPLAN	
FINNVEDSVÄLLEN VÄRNAMO	
MARKVÄRMESYSTEM I MARK	
FORMAT		SKALA		RITNINGSNR	
A1		1:400		M-10-1-002	
				REV	