


XREF: .\\1\\SK\\SK-modell\\SK-46-P-0100-1764-A.dwg
.\\1\\A\\A-modell\\A-40-P-0100-1764-A.dwg
.\\1\\A\\A-modell\\orienteringsfig.dwg
.\\1\\S\\S\\Sips - Skola.dwg

LAGER: SB11

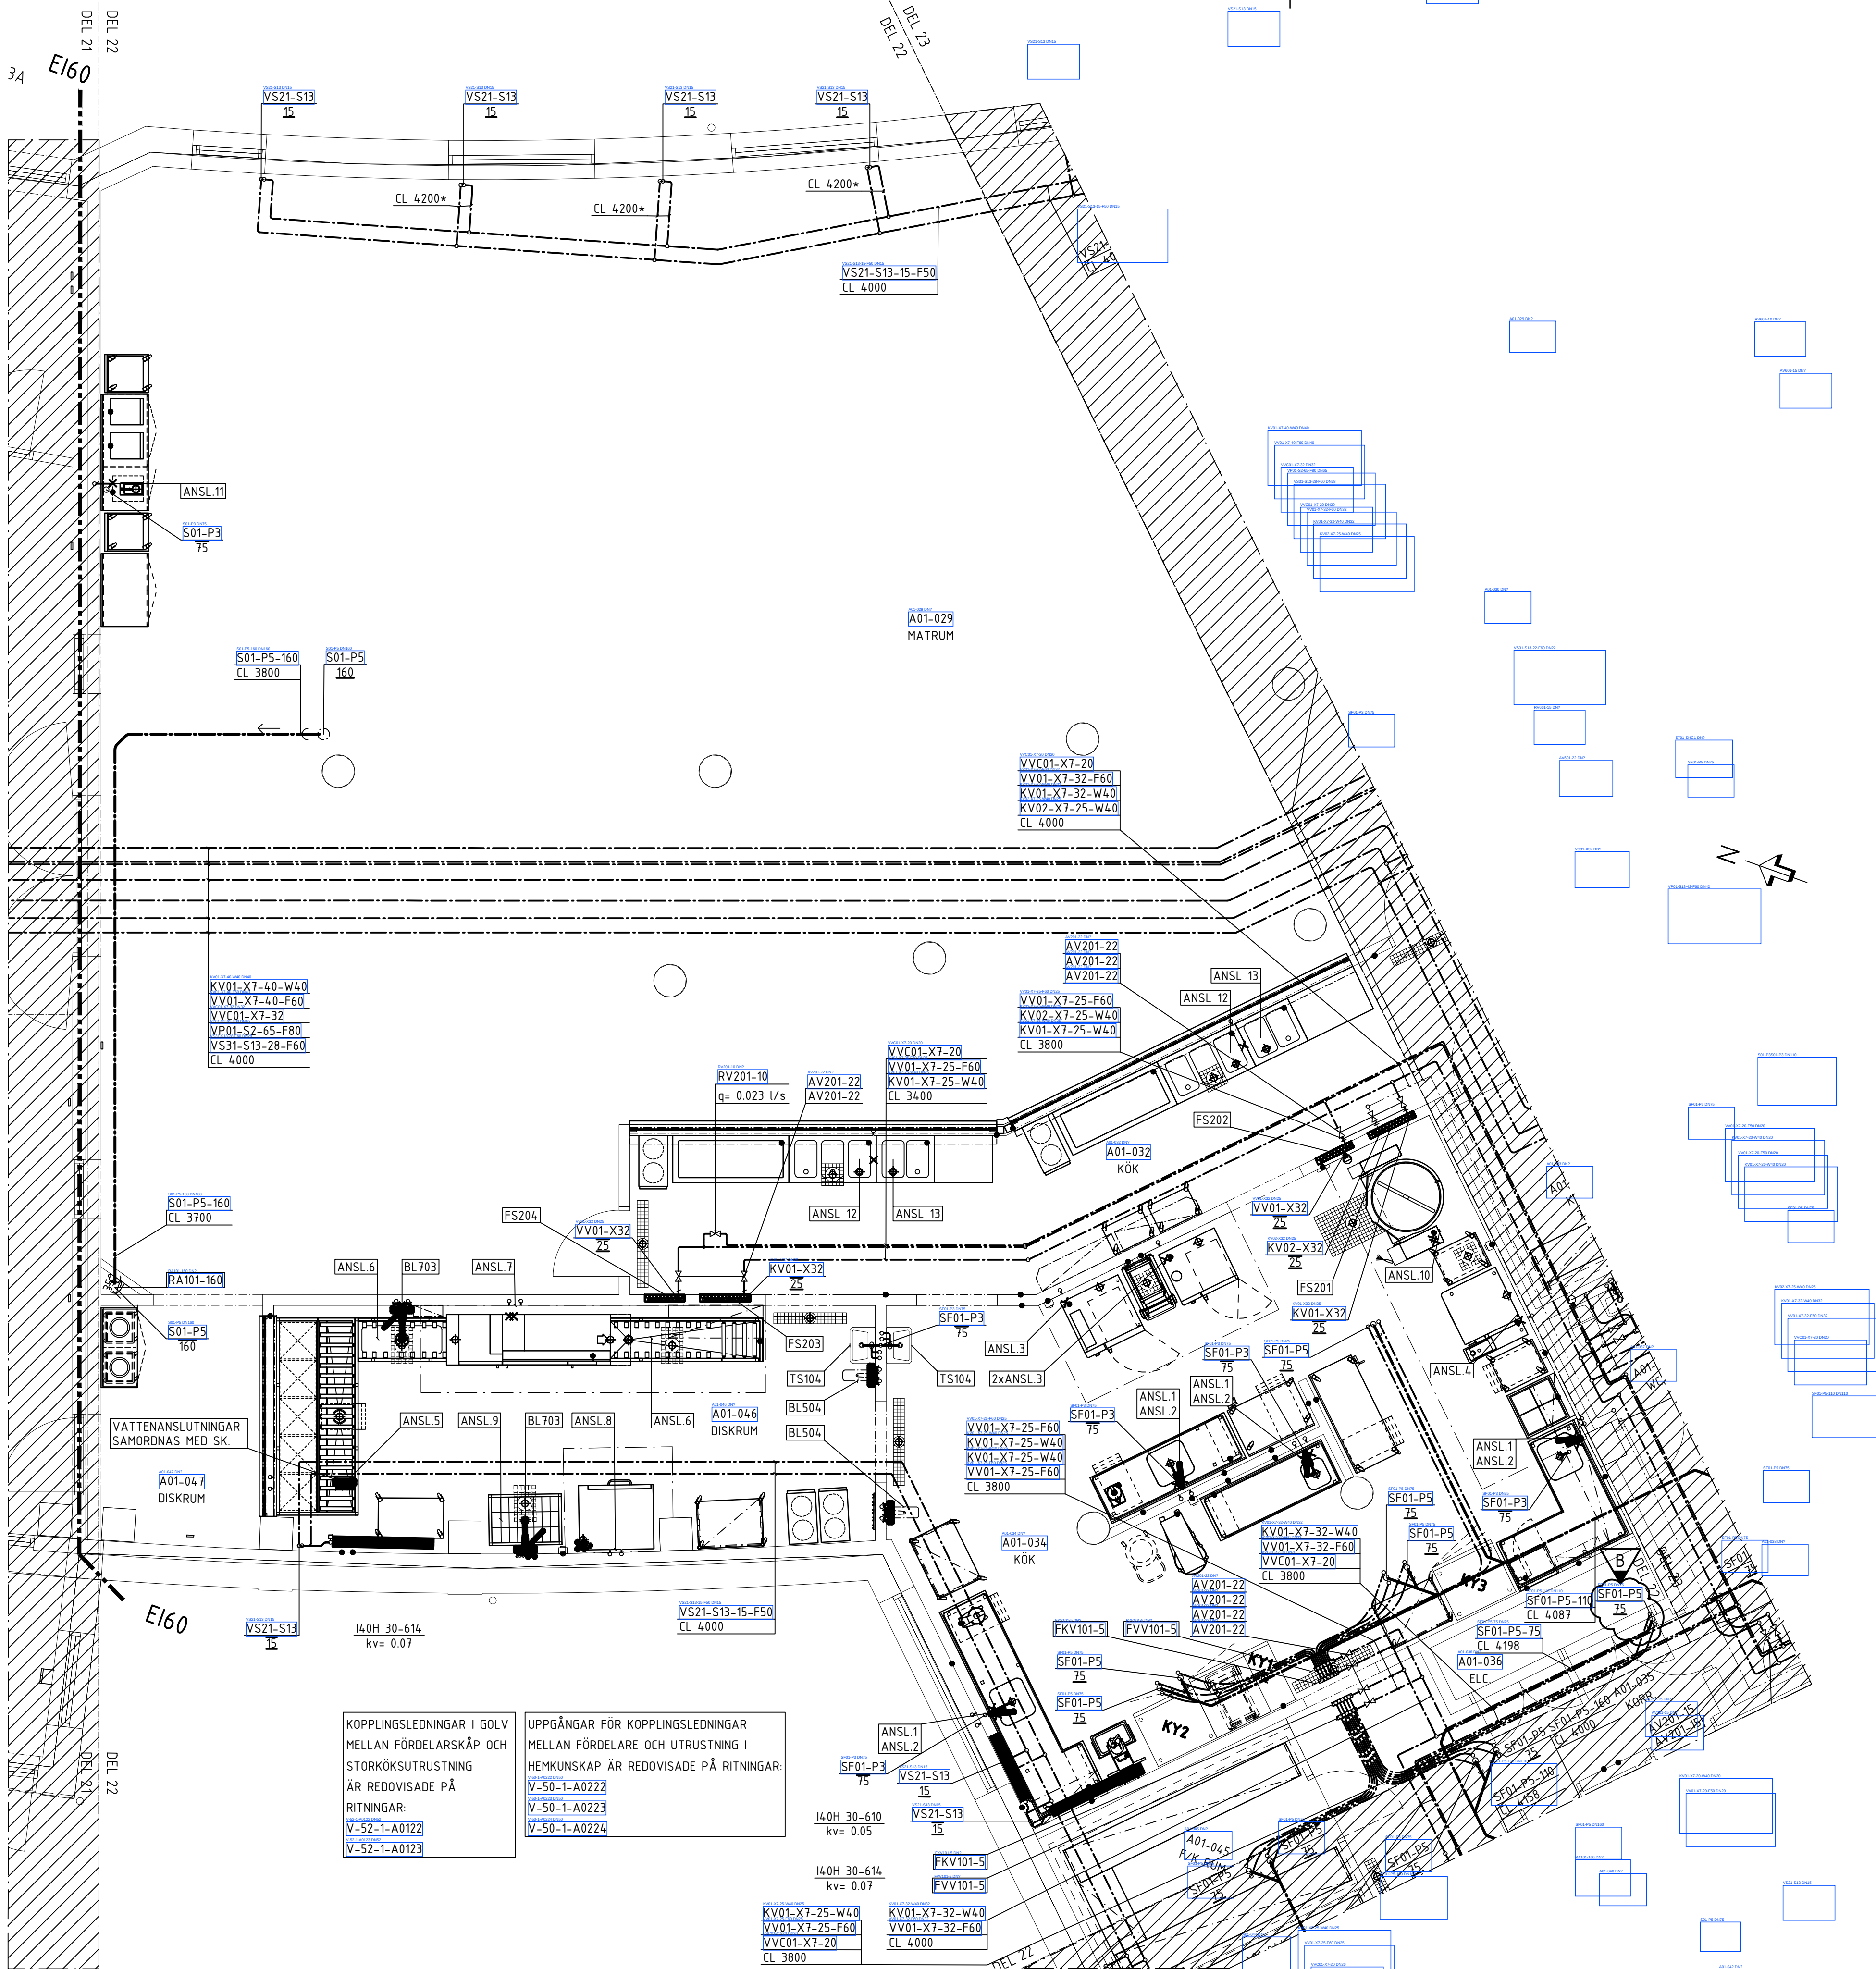

FÖRKLARINGAR
BETECKNING RÖRSYSTEM
VS11-S13-42-F100 - (100) mm
(L-F) Ev. isolering.
(42) Dimension
(S13) Rörmaterial
(11) Systemnummer
(VS) Systembeteckning

TAPPVATTENSYSTEM
KV01 Tappkallvatten
KV02 Tappkallvatten, kombiugn
VV01 Tappvarmvatten
VVC01 Varmvattencirkulation

SPILLVATTENSYSTEM
S01 Spillvatten
SF01 Spillvatten, fettavskiljare

S01 Fall min: 1%
SF01 Fall min: 2%

VÄRMEVATTENSYSTEM
FJ01 Fjärrvärme
VP01 Värmebärare, primär
VS11 Värmebärare, sekundär, ventilation
VS21 Värmebärare, sekundär, radiatorer
VS31 Värmebärare, sekundär, golvvärme

RÖRLEDNINGAR
G3 MA-rör
K5 Kopparrör.Frkr
P2 PP markavloppsror
P3 PP-rör (avlopp inomhus)
P5 PP-rör (avlopp inomhus (juddämpat))
R2 Ledningar av syrafast stål
R10 Rostfritt avloppsror, muff
S2 Handstubb, stål
S6 Tryckkärlsstål
S13 Presskopplingsrör utv förs
X7 PAL-RÖR
X31 PEX-RIR
X32 PEX-RIR, extraisolerade

ISOLERING AV INSTALLATIONER
-F Mineralull
-W Mineralull, diffusionstät

VV01 & VVC01 SAMISOLERAS

SAKVAROR
Enl. BESKRIVNING AVSEENDE
VÄRME- OCH SANITÄTSANLÄGGNING
HANDLINGSNUMMER 11.A.2.1

MÄRKNING AV STYRKOMPONENTER
Föregås av 1764-A-

ÖVRIGT
CL xxxx* = Samma rördimension som
stick och isolering F50

KOPPLINGSLEDNINGAR FRÅN FÖRDELARE TILL APPARAT ENLIGT TABELL OM INGET ANNAT ANGES	
BL	VV01-X31
TS	KV01-X31
UB	
VK	

B	1	PM5-W	231113	K. PERSSON
A	0	PM1-W	230601	K. PERSSON
BET	ANT	ÄNDRINGEN AVSER	DATUM	SEN

BYGGHANDLING



HYLLIE NYA HÖGSTADIUM OCH SPORTHALL 3
NYBYGGNAD AV SKOLA OCH SPORTHALL 5800



FÖRETAG SWECO SVERIGE AB	TEL 040 - 16 70 00
UPPGÄV 30025113	RITAD AV K. PERSSON
DATUM 2023-01-31	REVISOR D. HAGSTRÖM
ANSVARIG J. ÅKESSON	

RUNDSTICKAN 1
RÖRINSTALLATIONER
HUS A PLAN 1 DEL 22

OBJEKTSNUMMER	BYGGNAD	PLAN	DEL	UNDERGRUPP	DISCIPLIN
1764	A	01	22	50	W
SKALA	RITINGSNUMMER	BET			
1:50	V-50-1-A0122	B			

\\SELUP\\5002\\PROJEKT\\21332\\30025113\\HYLLIE_NYA_HÖGSTADIUM\\1764-A.dwg PERSSON, KRISTOFFER