


XREF: .\1\SVK\SK-modell\SK-16-P-0100-1764-A.dwg
.\1\A.A-modell\A-10-P-0100-1764-A.dwg
.\1\A.A-modell\orienteringsfig.dwg
.\1\slips\Slips - Skola.dwg

LAGER: SB11

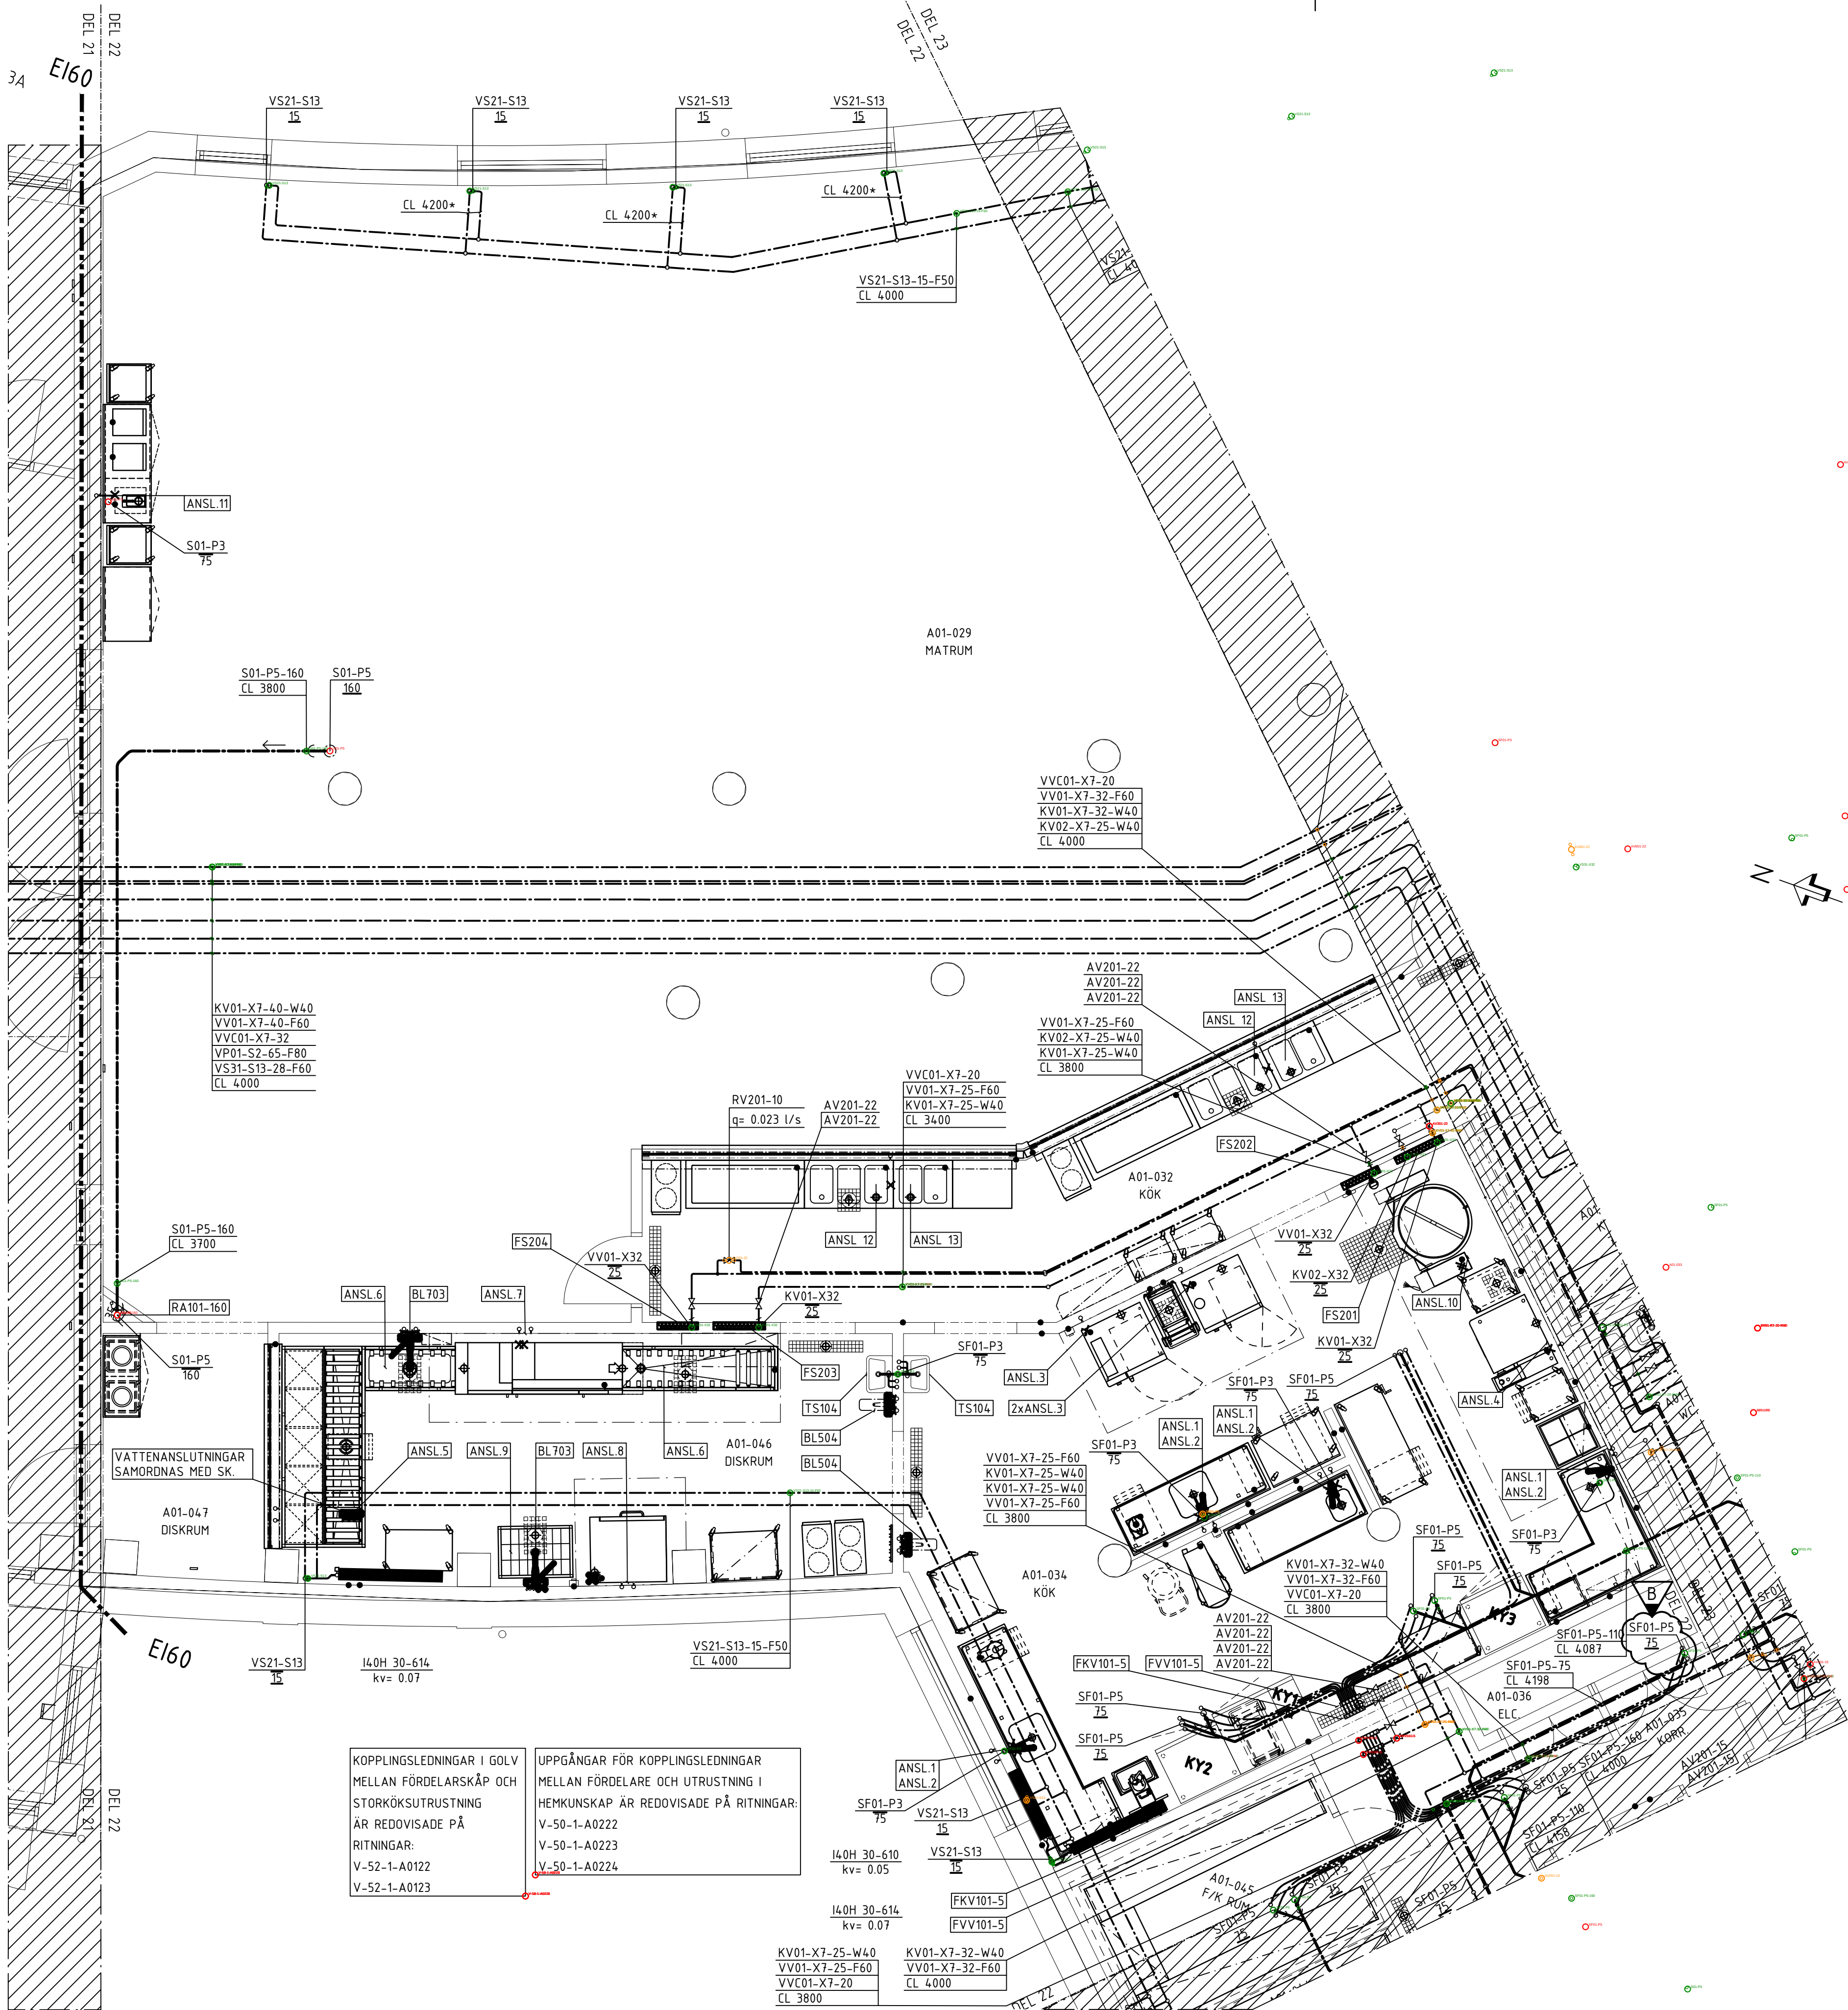

FÖRKLARINGAR
BETECKNING RÖRSYSTEM
VS11-S13-42-F100 - (100) mm
(L-F) Ev. isolering.
(42) Dimension
(S13) Rörmaterial
(11) Systemnummer
(VS) Systembeteckning

TAPPVATTENSYSTEM
KV01 Tappkallvatten
KV02 Tappkallvatten, kombiugn
VV01 Tappvarmvatten
VVC01 Varmvattencirkulation

SPILLVATTENSYSTEM
S01 Spillvatten
SF01 Spillvatten, fettavskiljare

S01 Fall min: 1‰
SF01 Fall min: 2‰

VÄRMEVATTENSYSTEM
FJ01 Fjärrvärme
VP01 Värmebärare, primär
VS11 Värmebärare, sekundär, ventilation
VS21 Värmebärare, sekundär, radiatorer
VS31 Värmebärare, sekundär, golvvärme

RÖRLEDNINGAR
G3 MA-rör
K5 Kopparrör Frkr
P2 PP markavlopps rör
P3 PP-rör (avlopp inomhus)
P5 PP-rör (avlopp inomhus luddämpat)
R2 Ledningar av syrefast stål
R10 Rostfritt avloppsrör, muff
S2 Handstubb, stål tub
S6 Tryckkärlsstål
S13 Presskopplingsrör utv förs
X7 PAL-RÖR
X31 PEX-RIR
X32 PEX-RIR, extraisolerade

ISOLERING AV INSTALLATIONER
-F Mineralull
-W Mineralull, diffusionstät

VV01 & VVC01 SAMISOLERAS

SAKVAROR
Enl. BESKRIVNING AVSEENDE
VÄRME- OCH SANTITETSANLÄGGNING
HANDLINGSNUMMER 11.A.2.1

MÄRKNING AV STYRKOMPONENTER
Föregås av 1764-A-

ÖVRIGT
CL xxxx* = Samma rördimension som
stick och isolering F50

KOPPLINGSLEDNINGAR
FRÅN FÖRDELARE TILL
APPARAT ENLIGT TABELL
OM INGET ANNAT ANGES

VV01-X31	KV01-X31
BL	TS
TS	UB
UB	VK
VK	

B	1	PM5-W	231113	K. PERSSON
A	0	PM1-W	230601	K. PERSSON
BET	ANT	ÄNDRINGEN AVSER	DATUM	SEN

BYGGHANDLING



HYLLIE NYA HÖGSTADIUM OCH SPORTHALL 3
NYBYGGNAD AV SKOLA OCH SPORTHALL 5800



FÖRETAG	SWECO SVERIGE AB	TEL	040 - 16 70 00
UPPDRAGSNUMMER	30025113	RITAD AV	K. PERSSON
DATUM	2023-01-31	HANDLAGARE	D. HAGSTRÖM
		REVISOR	J. ÅKESSON

OBJEKTSNUMMER	BYGGNAD	PLAN	DEL	UNDERGRUPP	DISCIPLIN
1764	A	01	22	50	W
SKALA	RITINGSNUMMER	BET			
1:50	V-50-1-A0122	B			

\\SELUP\S002\PROJEKT\21332\30025113_HYLLIE_NYA_HÖGSTADIUM\000\0 CAD\W\W-MODELL\V-50-P-0100-1764-A.DWG PERSSON, KRISTOFFER PLO: 2023-11-13 08:17