


XREF: .\1\SV\SK-model\SK-46-P-0100-1764-A.dwg
.\1\A\A-model\A-40-P-0100-1764-A.dwg
.\1\A\A-model\orient\enrigsfig.dwg
.\1\A\A-model\orient\enrigsfig.dwg
.\1\A\A-model\orient\enrigsfig.dwg

LAGER: SB11

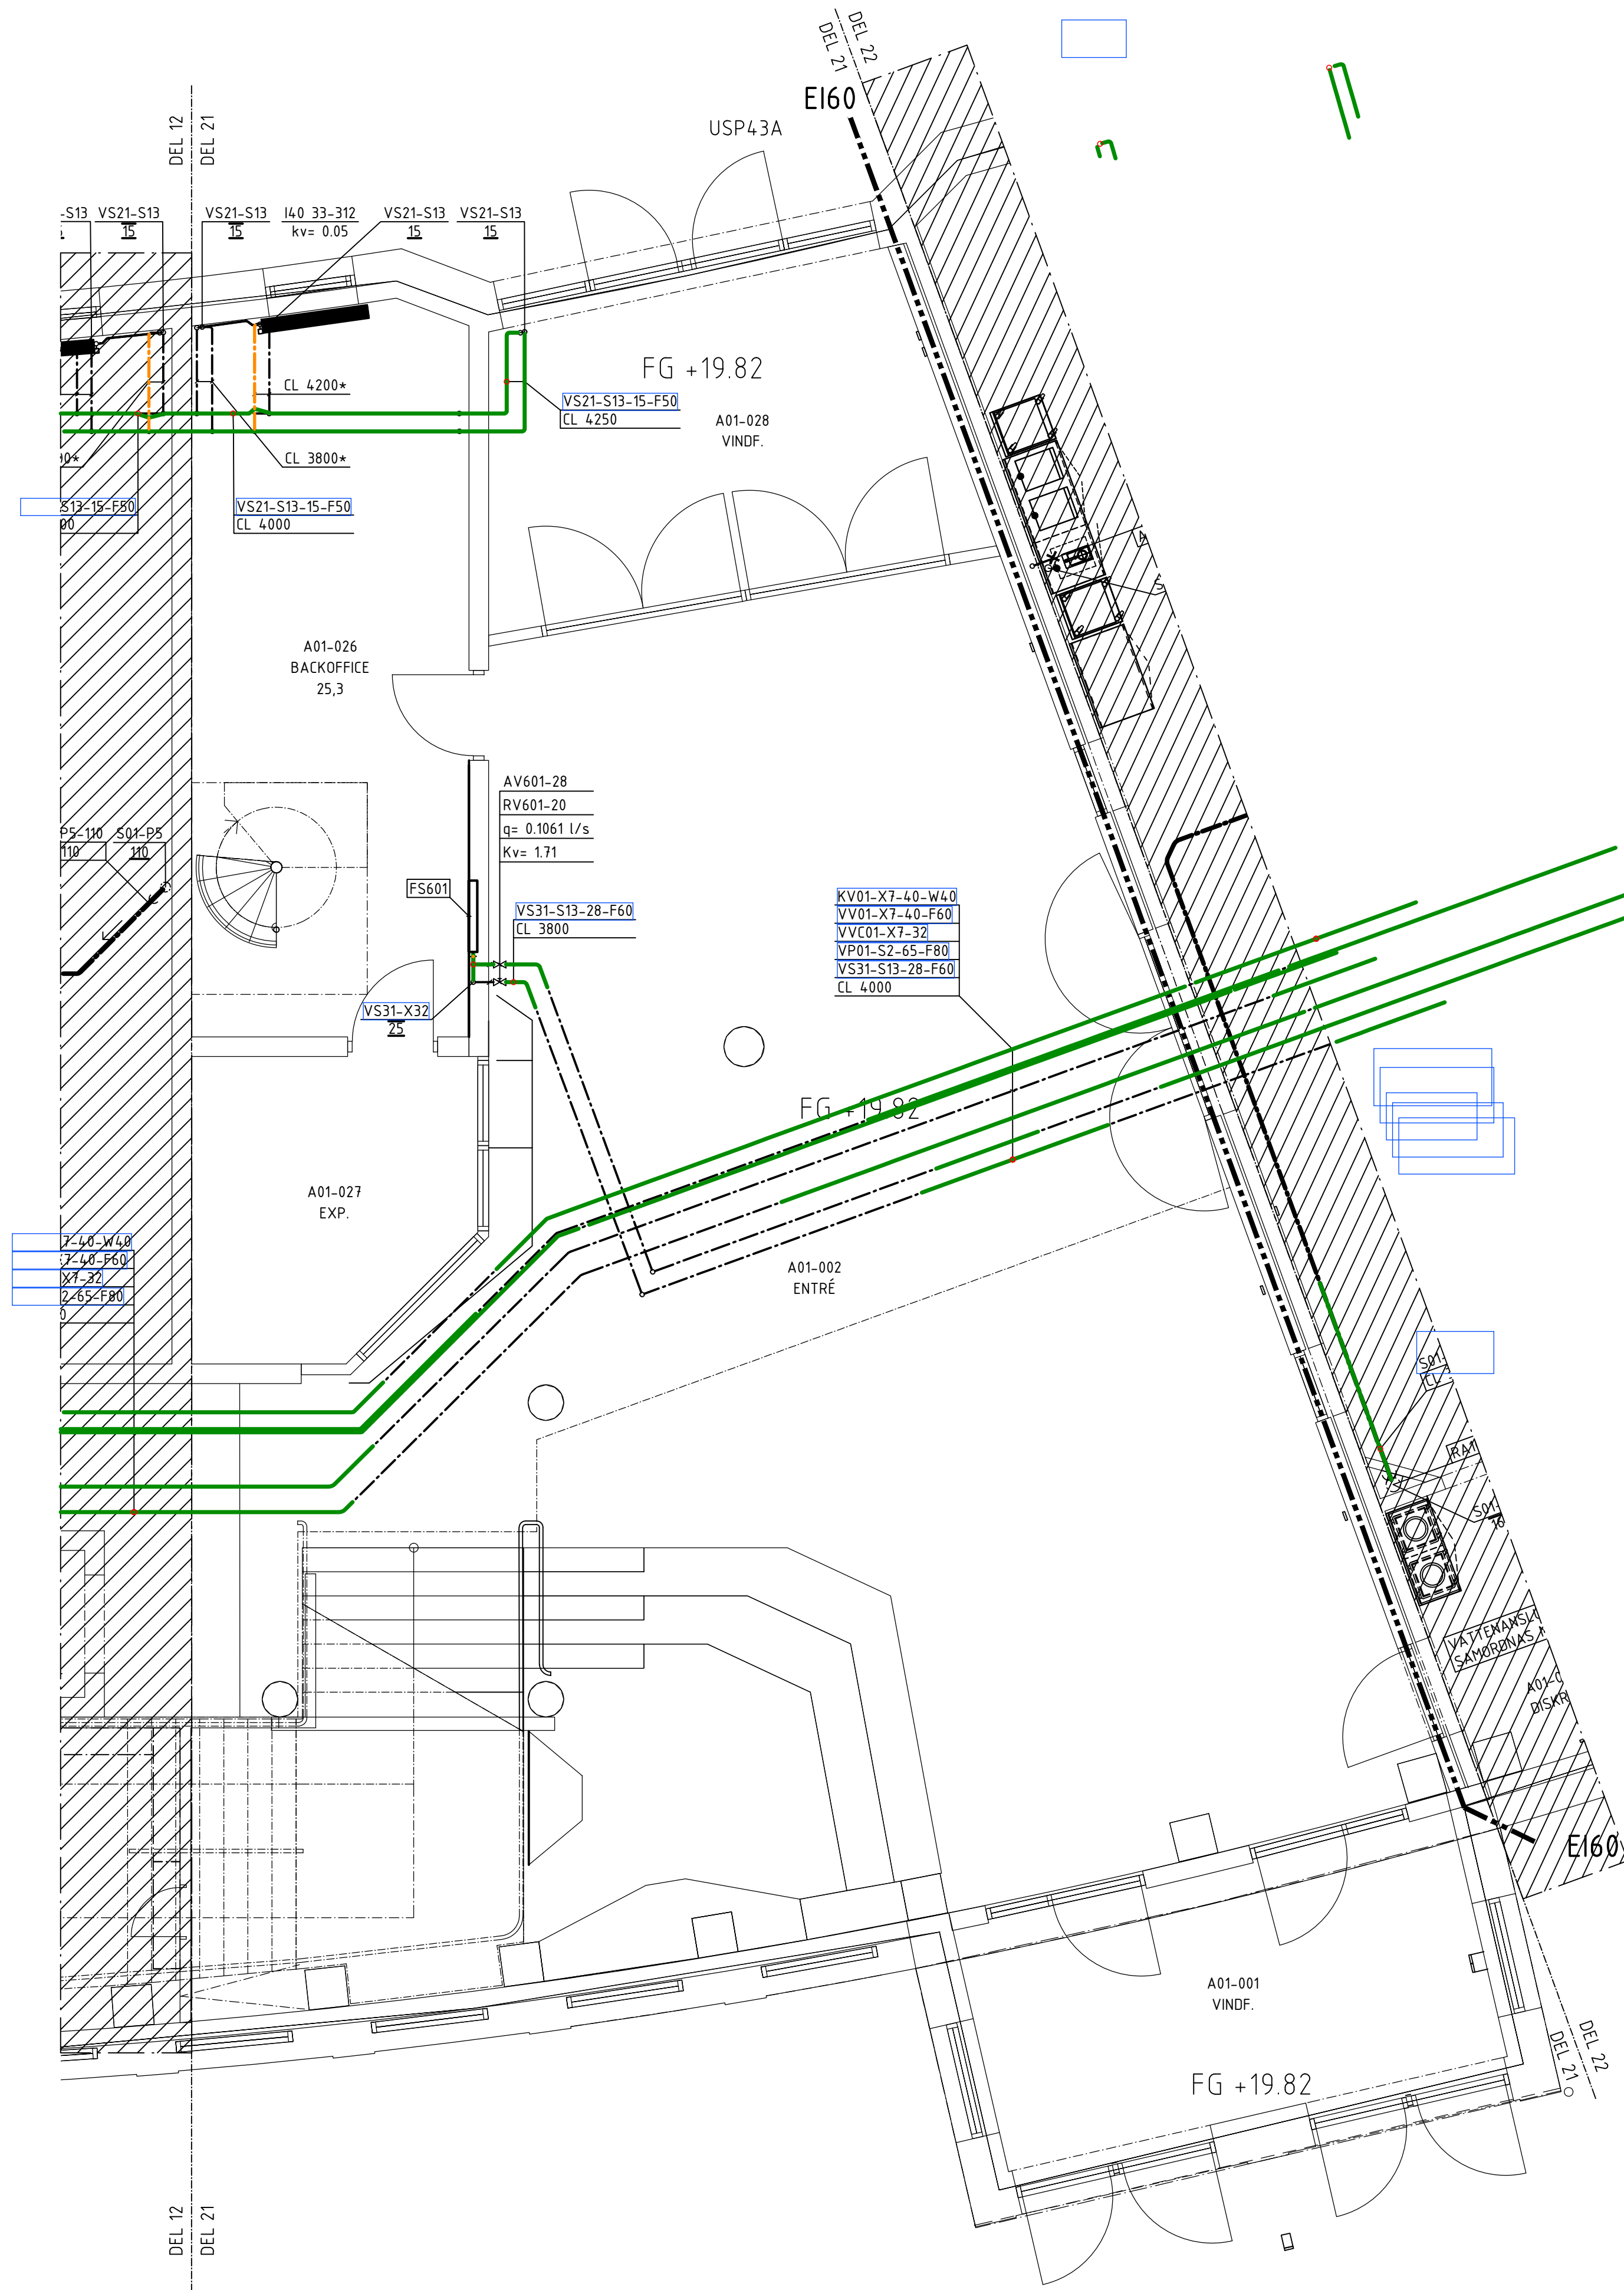

SKALA 1:50 (A1) 0 1 2 3 4 5

FÖRKLARINGAR

BETECKNING RÖRSYSTEM

VS11-S13-42-F100 - (100) mm

(L-F) Ev. isolering.

(42) Dimension

(S13) Rörmaterial

(11) Systemnummer

(VS) Systembeteckning

TAPPVATTENSYSTEM

KV01 Tappkallvatten

KV02 Tappkallvatten, kombiugnar

VV01 Tappvarmvatten

VVC01 Varmvattencirkulation

SPILLVATTENSYSTEM

S01 Spillvatten

SF01 Spillvatten, fettavskiljare

S01 Fall min: 1%

SF01 Fall min: 2%

VÄRMEVATTENSYSTEM

FJV01 Fjärrvärme

VP01 Värmebärare, primär

VS11 Värmebärare, sekundär, ventilation

VS21 Värmebärare, sekundär, radiatorer

VS31 Värmebärare, sekundär, golvvärme

RÖRLEDNINGAR

G3 MA-rör

K5 Kopparrör.Frkr

P2 PP markavloppsror

P3 PP-rör (avlopp inomhus)

P5 PP-rör (avlopp inomhus luddämpat)

R2 Ledningar av syrafäst stål

R10 Rostfritt avloppsror, muff

S2 Handelsstub, stål

S6 Tryckkärlsstål

S13 Presskopplingsrör utv förs

X7 PAL-RÖR

X31 PEX-RIR

X32 PEX-RIR, extraisolerade

ISOLERING AV INSTALLATIONER

-F Mineralull

-W Mineralull, diffusionstät

VV01 & VVC01 SAMISOLERAS

SAKVAROR

Enl. BESKRIVNING AVSEENDE

VÄRME- OCH SANITETSANLÄGGNING

HANDLINGSNUMMER 11.A.2.1

MÄRKNING AV STYRKOMPONENTER

Föregås av 1764-A-

ÖVRIGT

CL xxxx* = Samma rördimension som
stick och isolering F50

KOPPLINGSLEDNINGAR


FRÅN FÖRDELARE TILL

APPARAT ENLIGT TABELL

OM INGET ANNAT ANGES

VV01-X31	KV01-X31
BL	TS
TS	UB
UB	VK

A	O	PM1-W	230601	K. PERSSON	
BET	ANT	ÄNDRINGEN AVSER	DATUM	SEN	
BYGGHANDLING					
 Malmö stad Stadsfastigheter					
HYLLIE NYA HÖGSTADIUM OCH SPORTHALL 3 PROJEKT NR					
NYBYGGNAD AV SKOLA OCH SPORTHALL 5800					
SWECO Sweco Sverige AB - Tele: 08-695 60 00 - www.sweco.se					
FÖRETAG SWECO SVERIGE AB			TEL	040 - 16 70 00	
UPPDRAGSNUMMER 30025113		RITAD AV K. PERSSON	HANDLAGGARE D. HAGSTRÖM		
DATUM 2023-01-31		REV. DATUM 2023-06-01			
ANSVÄRIG J. ÅKESSON					
RUNDSTICKAN 1 RÖRINSTALLATIONER HUS A PLAN 1 DEL 21					
OBJEKTSNUMMER	BYGGNAD	PLAN	DEL	UNDERGRUPP	DISCIPLIN
1764	A	01	21	50	W
SKALA	RITINGSNUMMER				BET
1:50	V-50-1-A0121				A

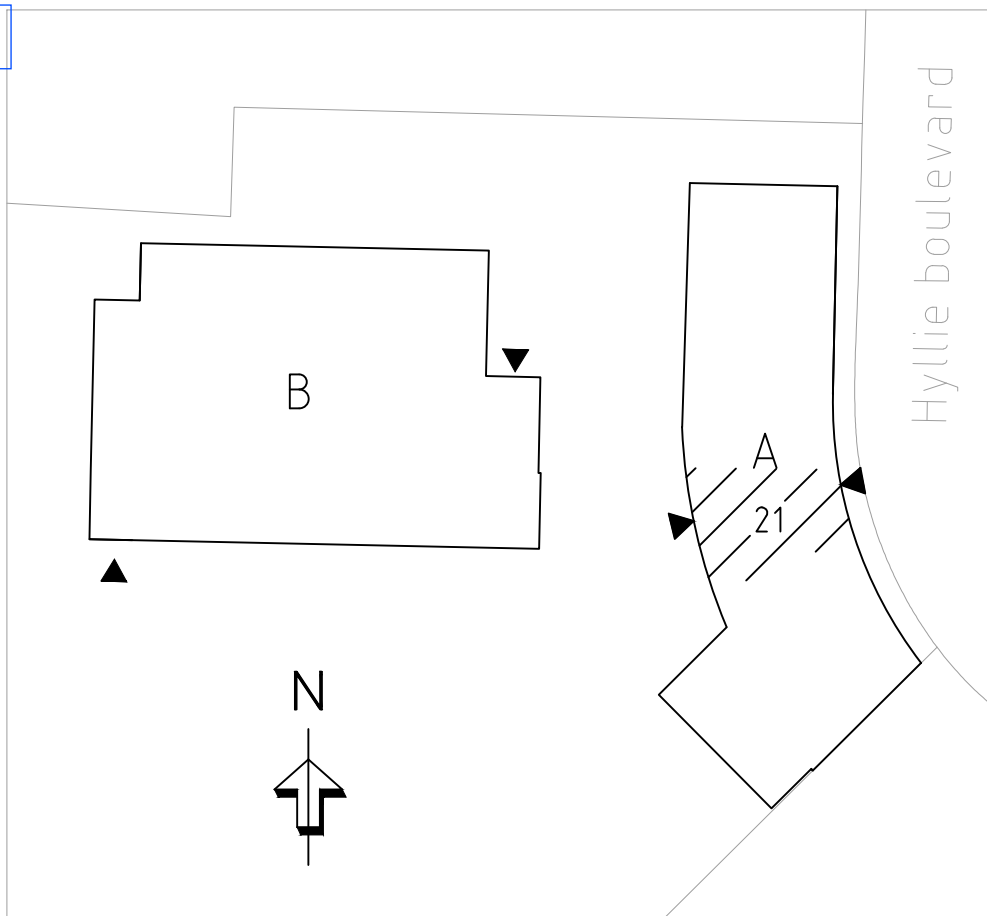

\\SELOF5002\PROJEKT\23332\30025113_HYLLIE_NYA_HÖGSTADIUMSKOLA\000\0 CAD\WMV-MODELLV-50-P-0100-1764-A.DWG PERSSON, KRISTOFFER