


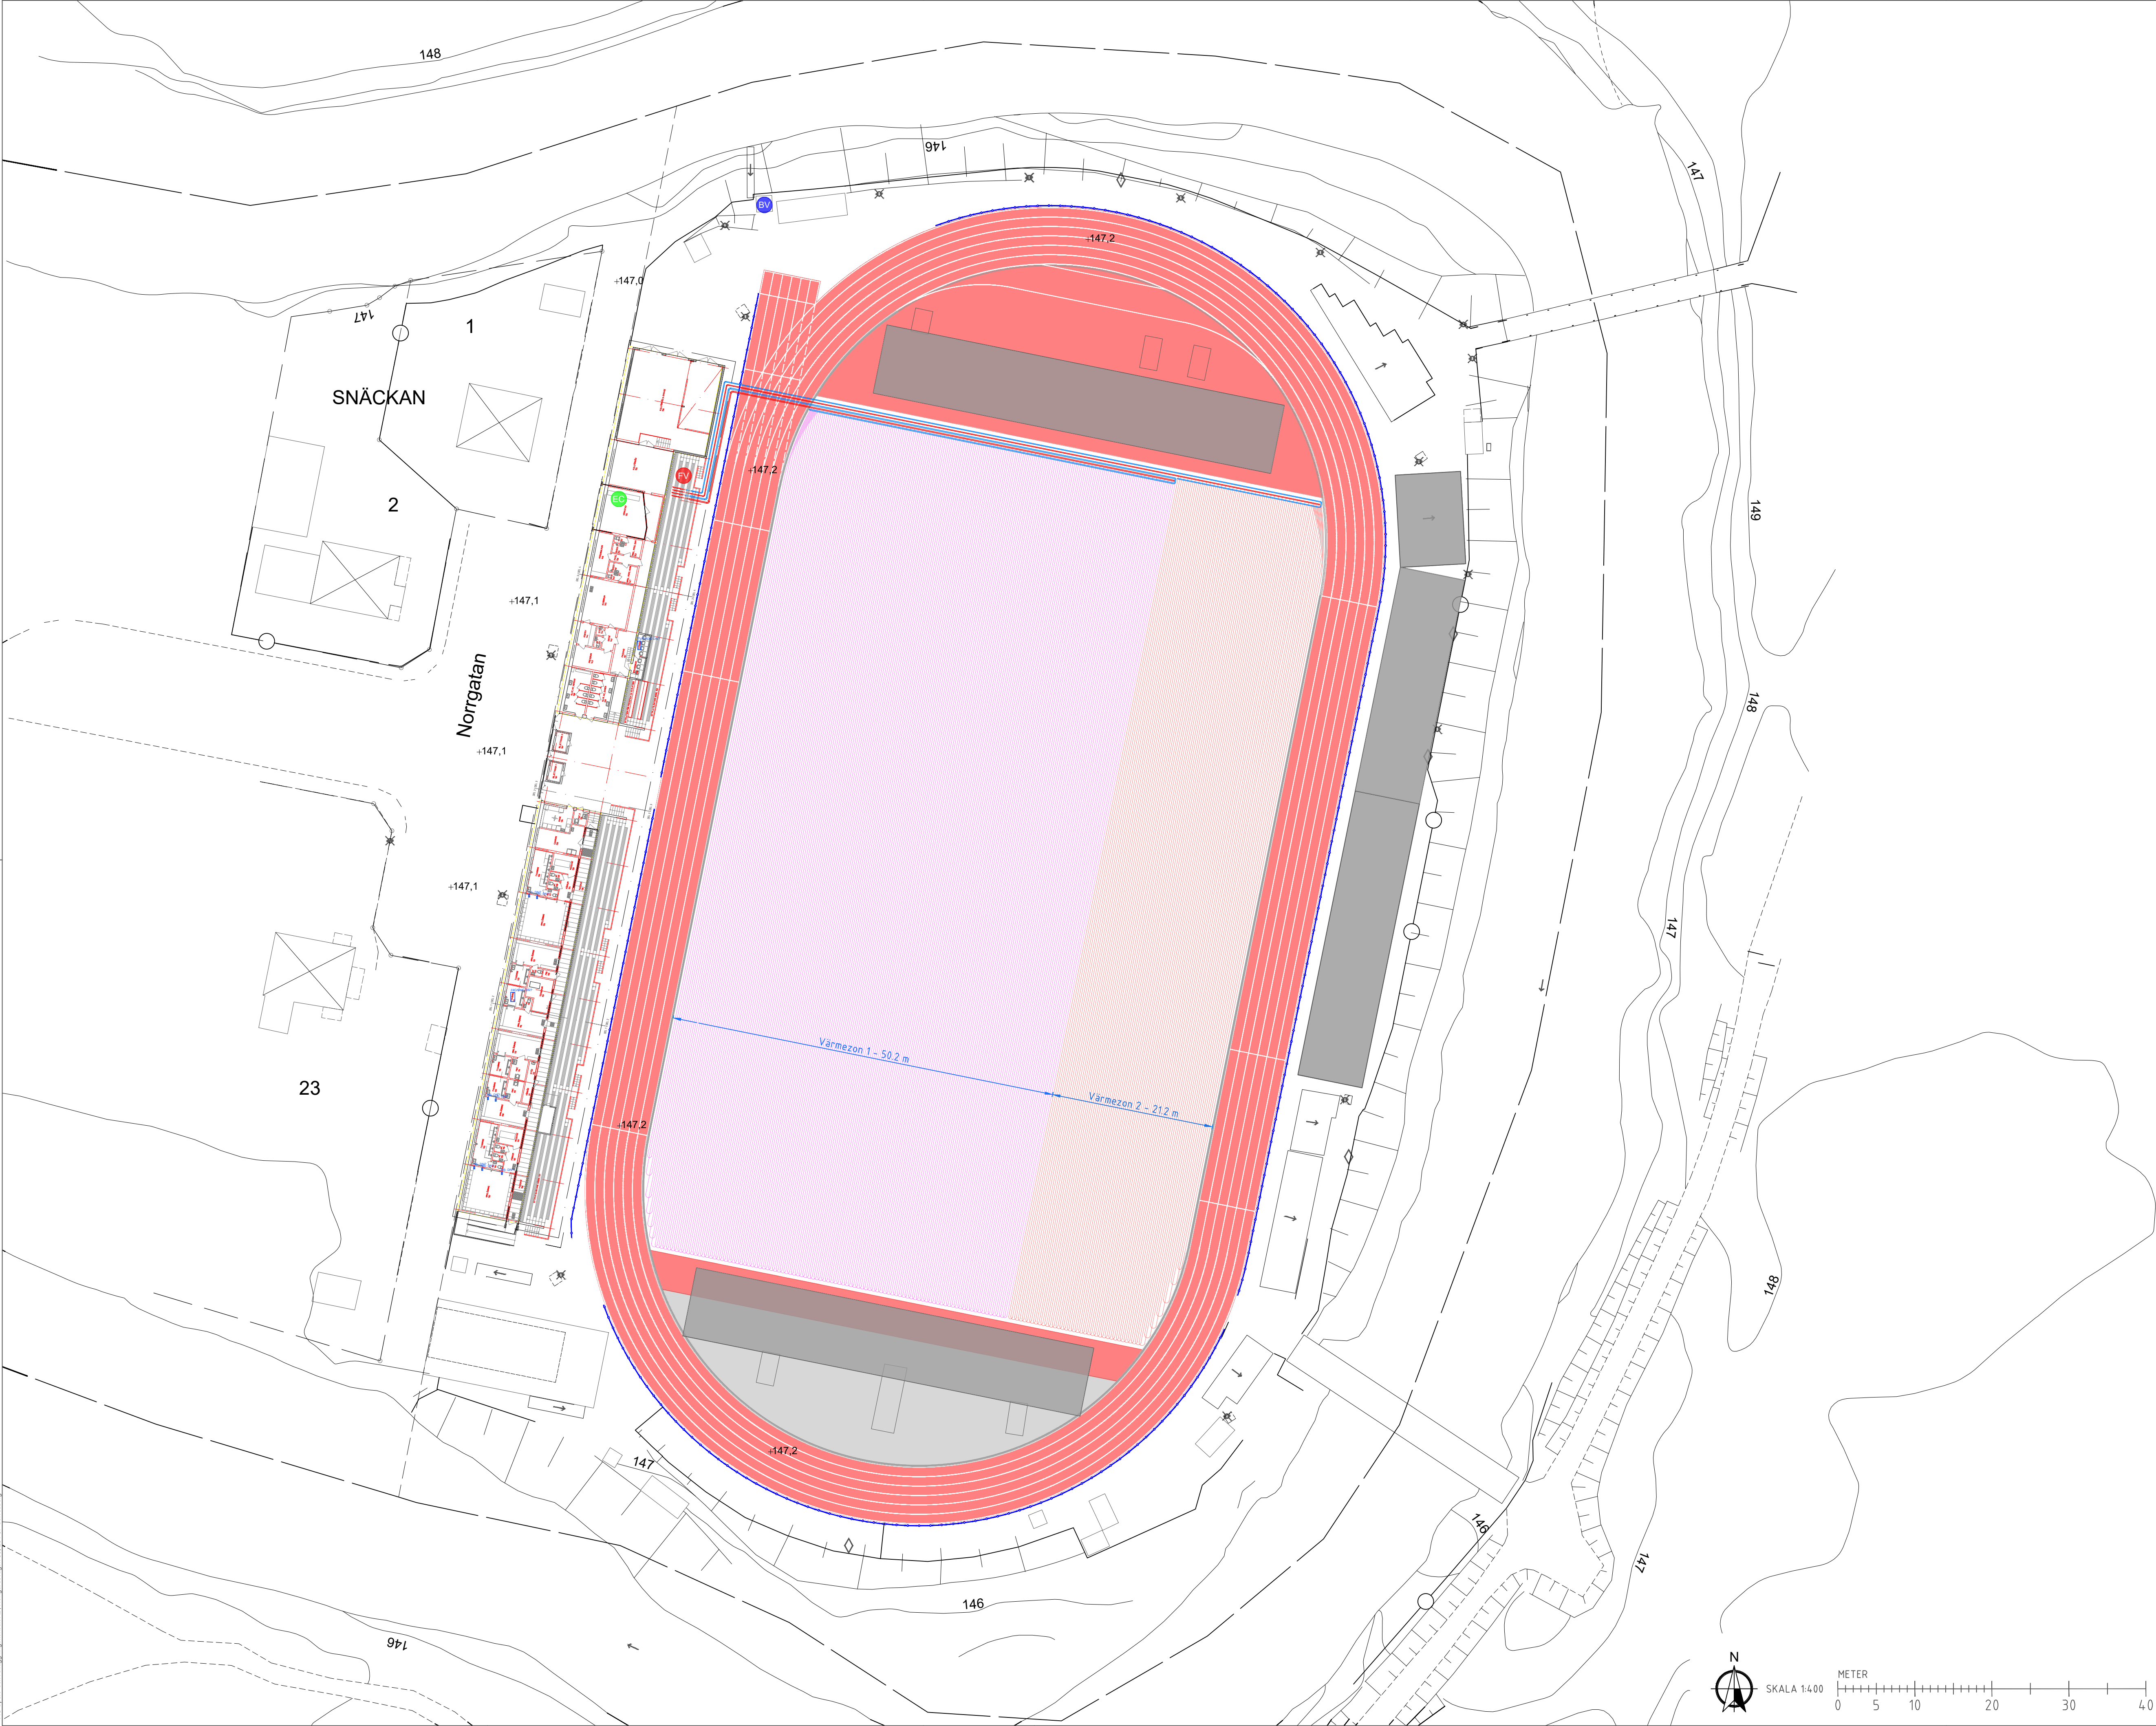

FÖRKLARINGAR

- Arbetsområde
- Räcke
- Nytt skåp med eluttag
- Bevatningspump
- Ny fjärrvärmecentral
- Befintlig elcentral

BET	ANT	ÄNDRINGEN AVSER	DATUM	SIGN
-----	-----	-----------------	-------	------

HANDLUSTYP
FORFRÅGNINGSUNDERLAG
PROJEKTENAMNING
MARKVÄRME OCH HYBRIDGRÄSPLAN
UPPDRAGSGIVARE



UPPDRAG NR A0		PROJEKTNUMMER	
DATUM 2026-03-05		DISCIPLIN	
MARKVÄRME OCH HYBRIDGRÄSPLAN FINNVEDSVÄLLEN VÄRNAMO		REV	
MARKVÄRMESYSTEM I MARK		RITNINGSR	
FORMAT A1	SKALA 1:400	RITNINGSR M-10-1-002	