


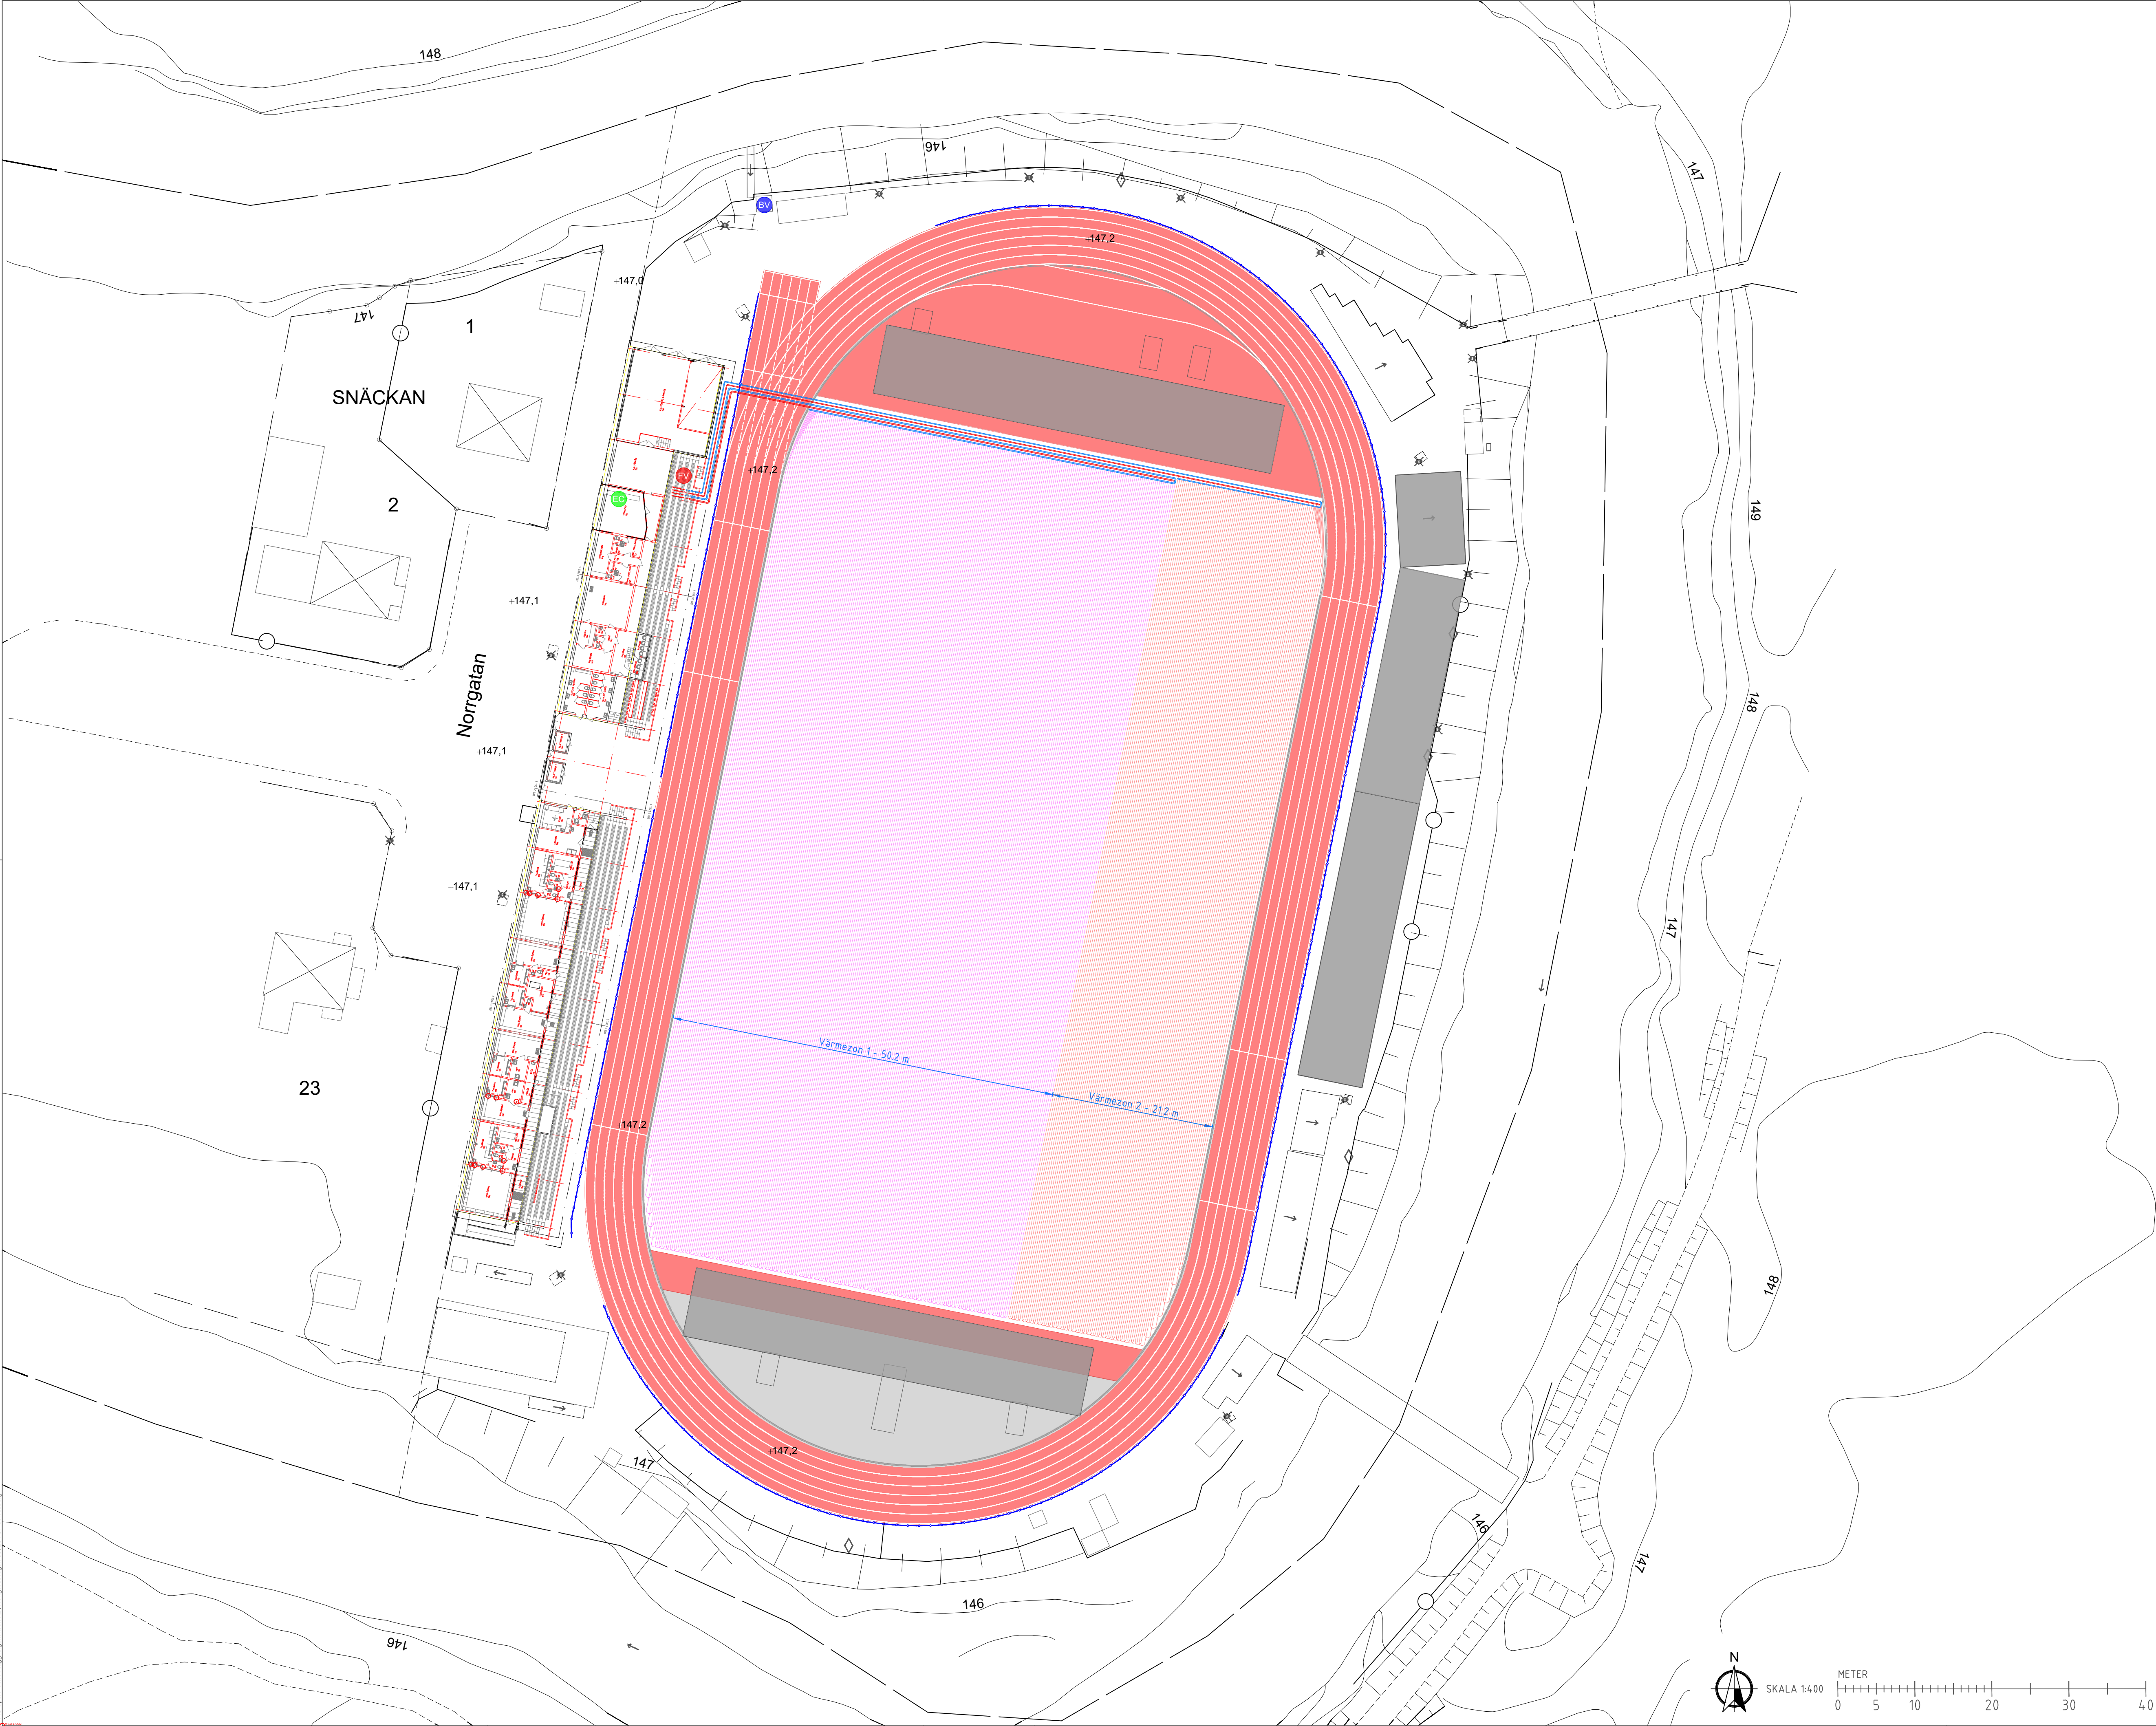

FÖRKLARINGAR

- Arbetsområde
- Räcke
- Nytt skåp med eluttag
- Bevatningspump
- Ny fjärrvärmecentral
- Befintlig elcentral

BET	ANT	ÄNDRINGEN AVSER	DATUM	SIGN
-----	-----	-----------------	-------	------

HANDLUSTYPT
FÖRFRÅGNINGSUNDERLAG
PROJEKTENAMNING
MARKVÄRME OCH HYBRIDGRÄSPLAN
UPPDRAGSGIVARE



A0 Sport- och Anläggningskonsult AB Mob. 070-376 17 45 E-post: anders@sportanlaggning.se		• Projektleddning • Alliansledning • Offentlig upphandling • Rådgivning • Besiktningar • Bygglösningar
UPPDRAG NR	RITAD/KONSTR AV A0	PROJEKTNUMMER
DATUM 2026-03-05	ANSVARIG	DISCIPLIN
MARKVÄRME OCH HYBRIDGRÄSPLAN FINNVEDSVÄLLEN VÄRNAMO		
MARKVÄRMESYSTEM I MARK		
FORMAT A1	SKALA 1:400	REVISION M-10-1-002