


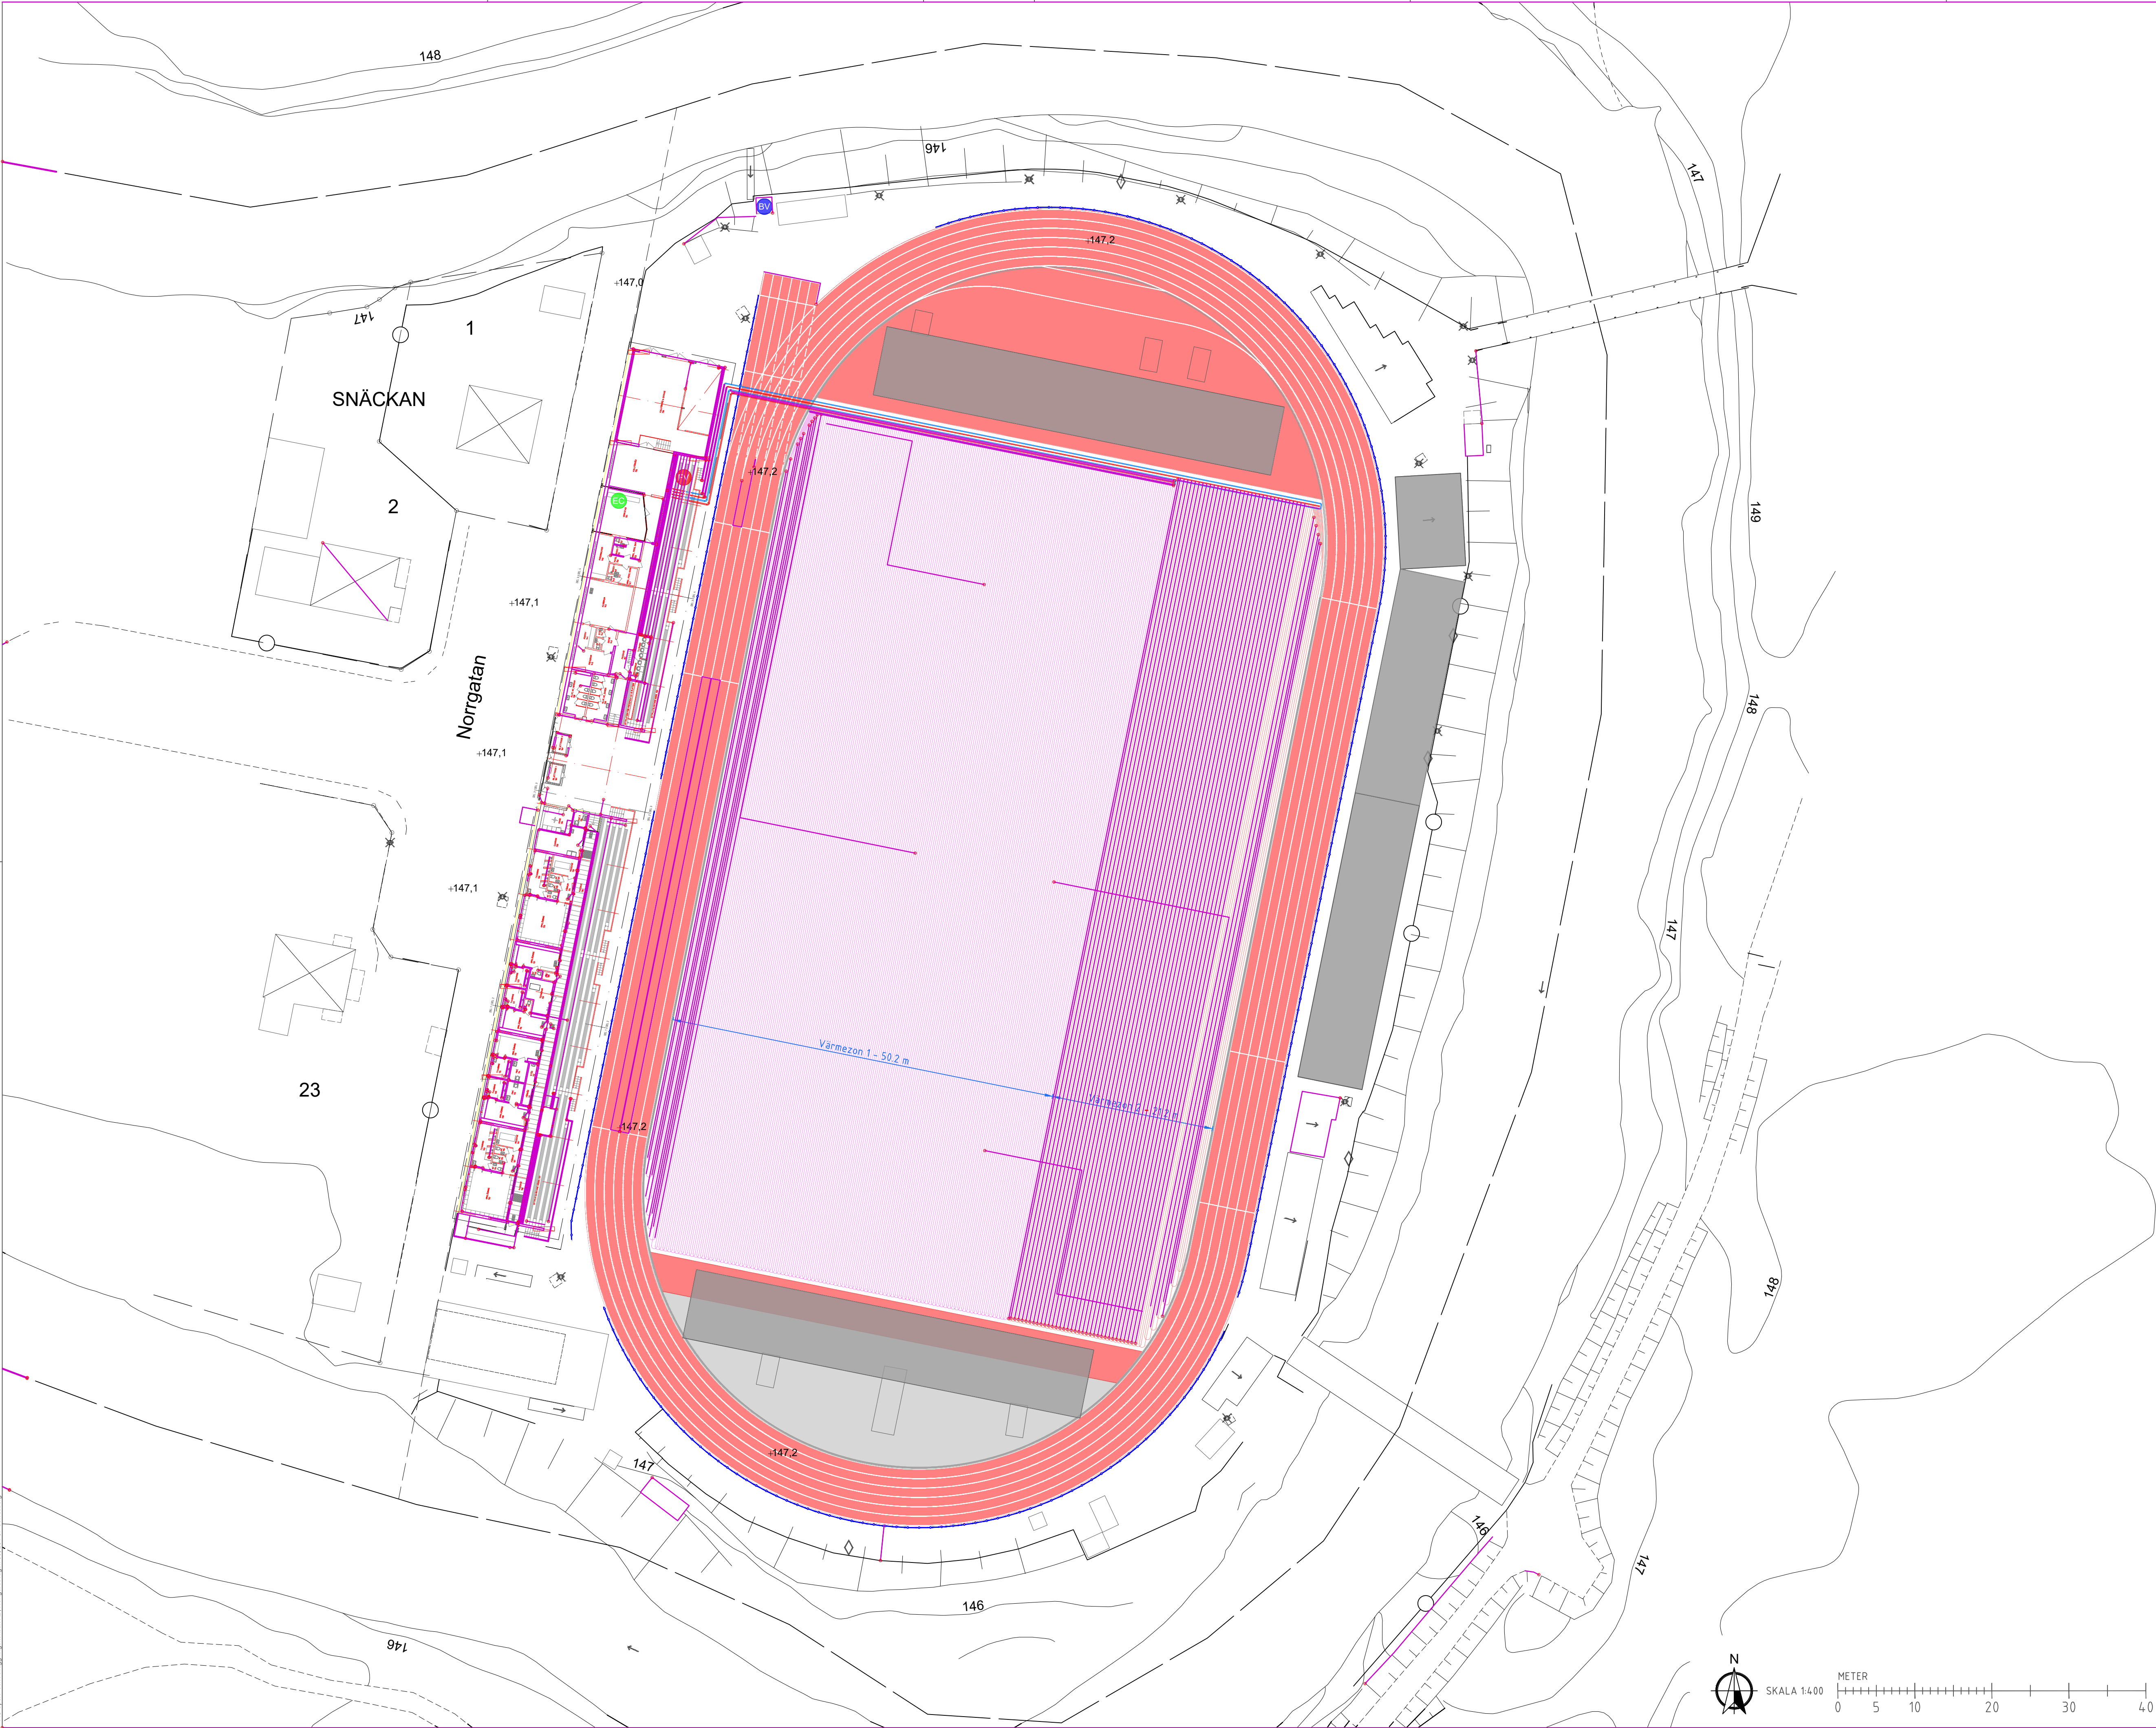

FÖRKLARINGAR

- Arbetsområde
- Räcke
- Nytt skåp med eluttag
- Bevakningspump
- Ny fjärrvärmecentral
- Befintlig elcentral

BET	ANT	ÄNDRINGEN AVSER	DATUM	SIGN
HANDLINGSTYP				
FÖRFRÅGNINGSUNDERLAG				
PROJEKTENÄMNING				
MARKVÄRME OCH HYBRIDGRÄSPLAN				
UPPDRAAGSGIVARE				
 VÄRNAMO KOMMUN			• Projektleddning • Alliansledning • Offentlig upphandling • Rättshänsyn • Besiktningar • Bygghänsynningar	
A0 Sport- och Anläggningskonsult AB Mob. 070-376 17 45 E-post: anders@sportanlaggning.se				
UPPDRAAG NR	RITAD/KONSTR AV		PROJEKTNUMMER	
	A0			
DATUM	ANSVARIG		DISCIPLIN	
2026-03-05				
MARKVÄRME OCH HYBRIDGRÄSPLAN FINNVEDSVÄLLEN VÄRNAMO				
MARKVÄRMESYSTEM I MARK				
FORMAT	SKALA	RITNINGSNR		REV
A1	1:400	M-10-1-002		