


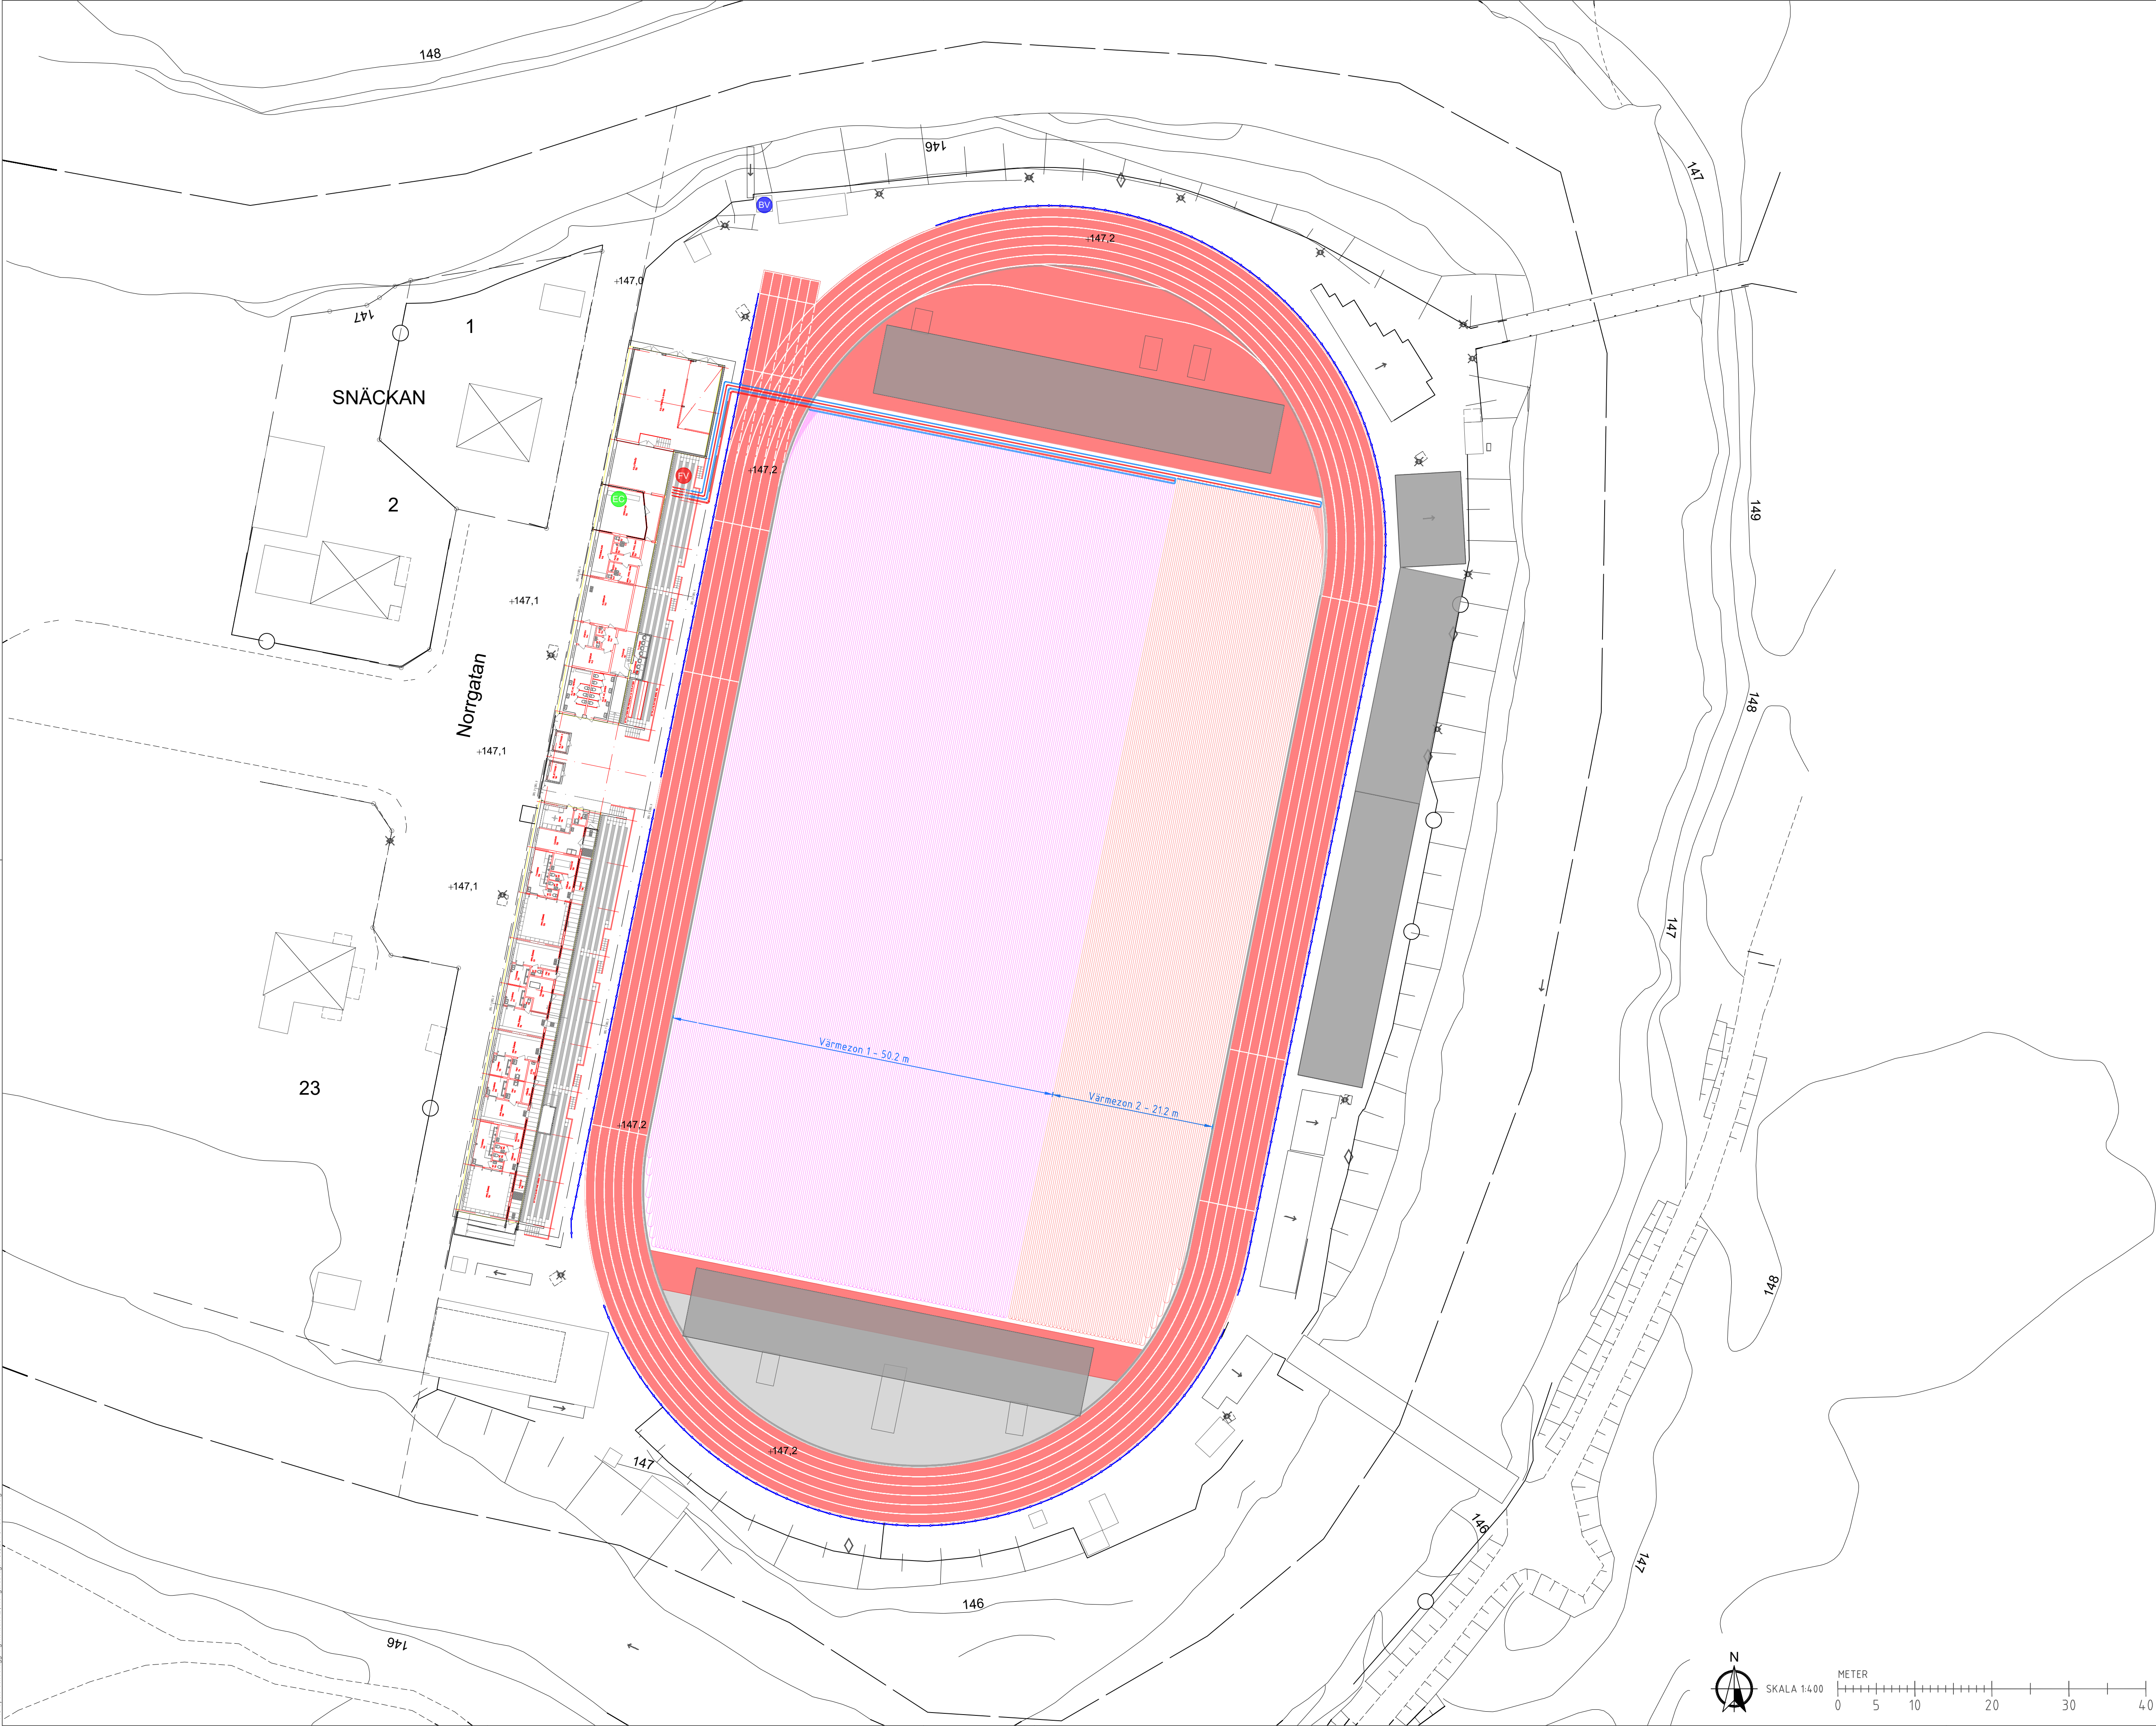

FÖRKLARINGAR

- Arbetsområde
- Räcke
- Nytt skåp med eluttag
- Bevatningspump
- Ny fjärrvärmecentral
- Befintlig elcentral

BET		ANT	ÄNDRINGEN AVSER	DATUM	SIGN	
HANDLUSTYPT FÖRFRÅGNINGSUNDERLAG PROJEKTENÄMNING MARKVÄRME OCH HYBRIDGRÄSPLAN UPPDRAGSGIVARE VÄRNAMO KOMMUN AO Sport- och Anläggningskonsult AB Mod. 070-376 17 45 E-post: anders@sporthandtagning.se • Projektledning • Alliansutveckling • Offentlig upphandling • Riksdagning • Besiktningar • Bygglösningar <tr><td colspan="2">UPPDRAG NR</td><td colspan="2">RITAD/KONSTR AV</td><td colspan="2">PROJEKTNUMMER</td></tr><tr><td colspan="2">DATUM</td><td colspan="2">ANSVARIG</td><td colspan="2">DISCIPLIN</td></tr><tr><td colspan="2">2026-03-05</td><td colspan="2"></td><td colspan="2"></td></tr><tr><td colspan="6">MARKVÄRME OCH HYBRIDGRÄSPLAN FINNVEDSVÄLLEN VÄRNAMO</td></tr><tr><td colspan="6">MARKVÄRMESYSTEM I MARK</td></tr><tr><td>FORMAT</td><td>SKALA</td><td colspan="3">RITNINGSNR</td><td>REV</td></tr><tr><td>A1</td><td>1:400</td><td colspan="3">M-10-1-002</td><td></td></tr>						UPPDRAG NR		RITAD/KONSTR AV		PROJEKTNUMMER		DATUM		ANSVARIG		DISCIPLIN		2026-03-05						MARKVÄRME OCH HYBRIDGRÄSPLAN FINNVEDSVÄLLEN VÄRNAMO						MARKVÄRMESYSTEM I MARK						FORMAT	SKALA	RITNINGSNR			REV	A1	1:400	M-10-1-002			
UPPDRAG NR		RITAD/KONSTR AV		PROJEKTNUMMER	
DATUM		ANSVARIG		DISCIPLIN	
2026-03-05	
MARKVÄRME OCH HYBRIDGRÄSPLAN FINNVEDSVÄLLEN VÄRNAMO	
MARKVÄRMESYSTEM I MARK	
FORMAT	SKALA	RITNINGSNR			REV	
A1	1:400	M-10-1-002	