
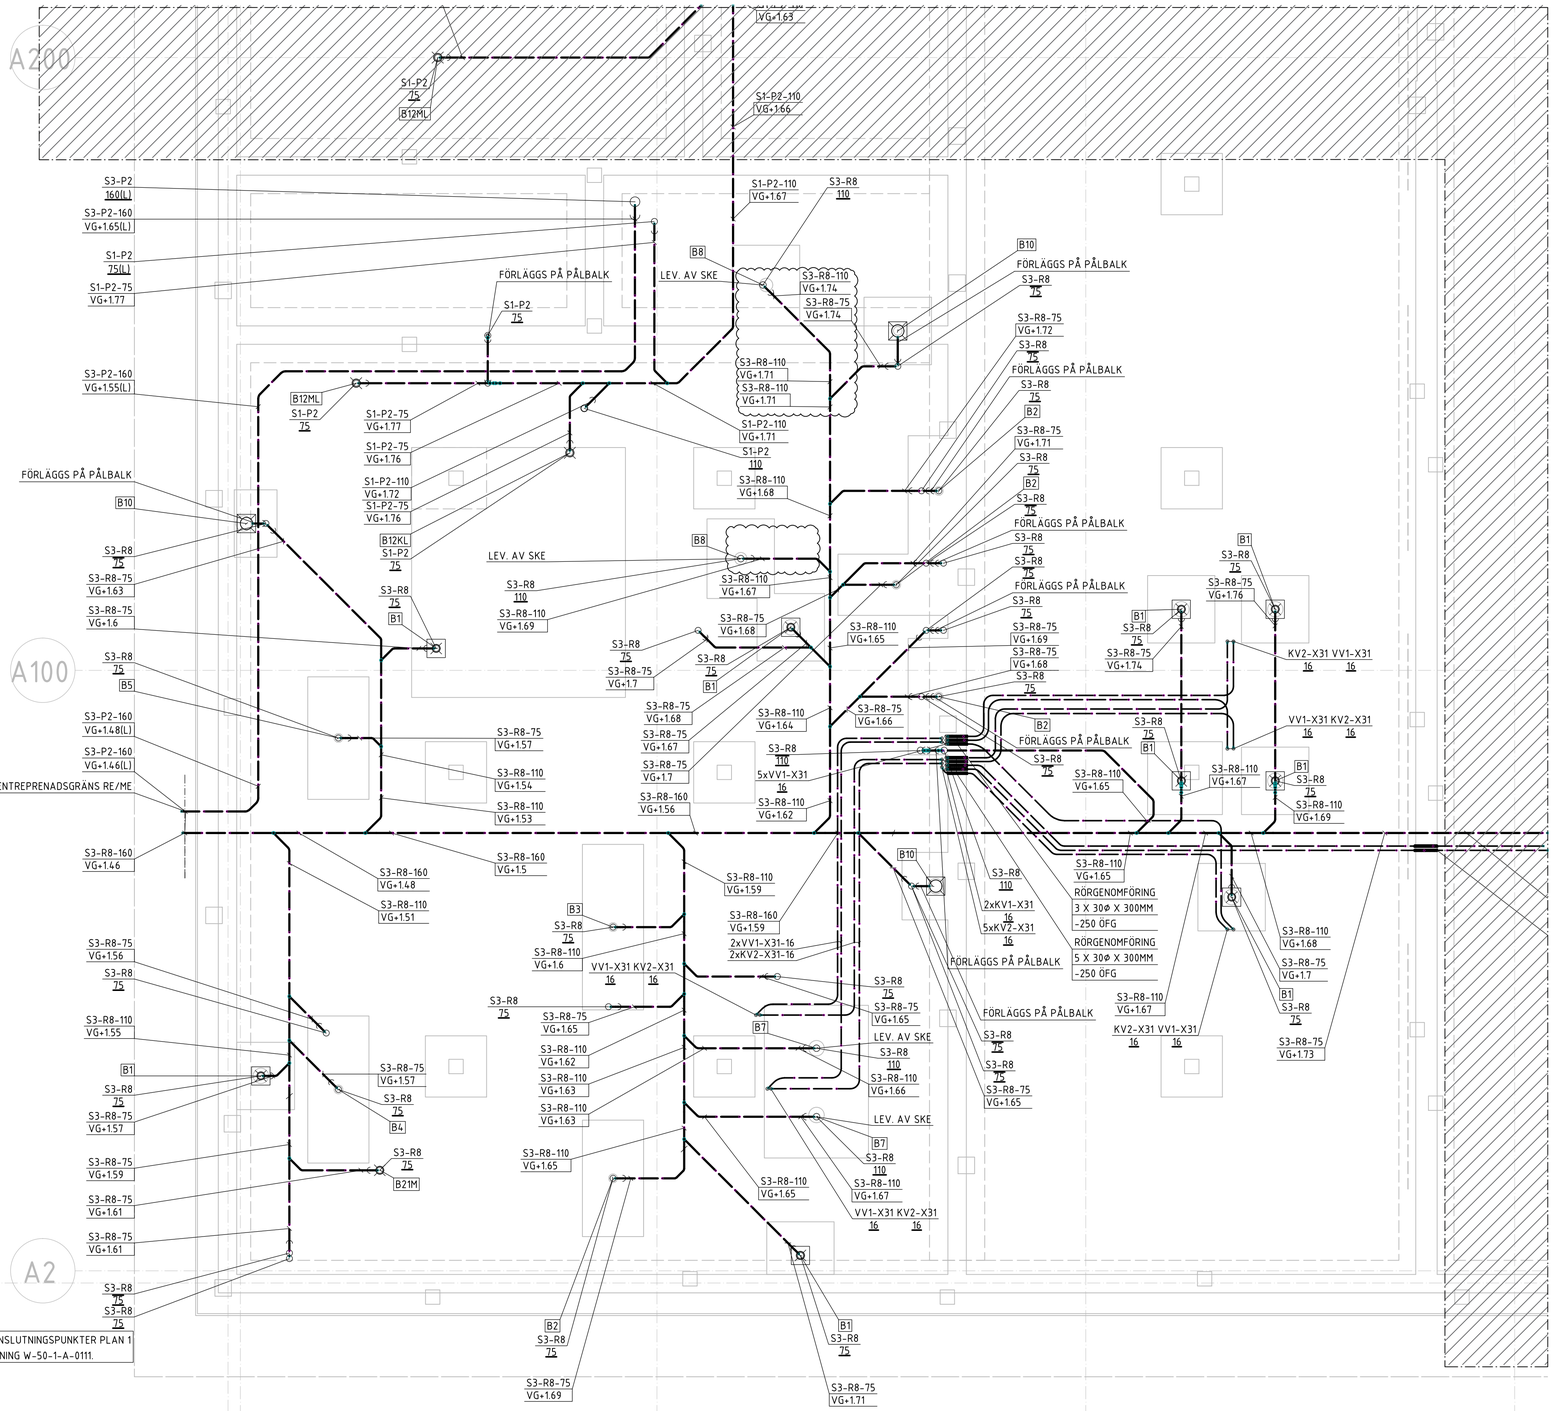


INGÅR I VS
B1-GOLVBRUNN 300x300 (8st)
B2-GOLVRÄNNA 1000x150 (4st)
B3-GOLVRÄNNA 1900x150 (1st)
B4-GOLVRÄNNA 1600x150 (1st)
B5-GOLVRÄNNA 1200x150 (1st)
B10-GOLVBRUNN 300x300 (3st)

INGÅR I SKE
B7-GOLVBRUNN 900x600 (2st)
B8-GOLVRÄNNA 500x300 (2st)

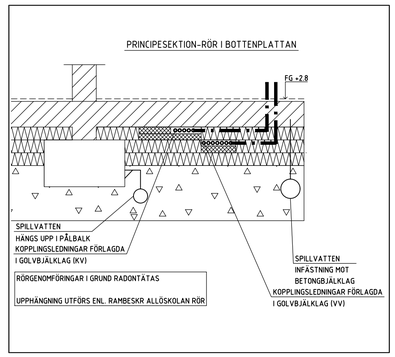

FÖRKLARINGAR

XX00-X00-000/X00
- SYSTEM + LÖPNUMMER
- MATERIAL + VARIANTNR
- DIMENSION
- ISOLERINGTYP

SYSTEM VÄRME

FJV1	FJÄRRVÄRME

SYSTEM TAPPVATTEN

KV1	KALLVATTEN, OAVHÄRDAT, 5 °C
KV2	KALLVATTEN, AVHÄRDAT, 5 °C
VV1	VARMVATTEN, 55°C
VVC1	VARMVATTENCIRKULATION, 50°C

SYSTEM SPILLVATTEN

D1	DAGVATTEN, ALLMÄNT I MARK
S1	SPILLVATTEN, ALLMÄNT I MARK
S2	SPILLVATTEN, ALLMÄNT INOMHUS
S3	SPILLVATTEN FRÅN STORKÖK

MATERIAL, RÖR

E13	PEM, TRYCKRÖR
S6	STÅLRÖR, TUBRÖR TRYCKKÄRLSKVALITET, SVETSFOG
X31	LEDNINGAR AV PEX (PE-XA) MED RIR

MATERIAL, SPILLVATTEN

E4	PE-RÖR, TRYCKRÖR, PN16
P2	LEDNINGAR AV PP-RÖR, SLÄTA MARKAVLOPPSRÖR I BYGGNAD
R8	LEDNINGAR AV ROSTFRIA RÖR

ISOLERING

W	MINERALULL FABRIKSMONTERAD ALU-PLÅT
V	CELLGUMMISLANG

YTBEKLÄDNAD

B	PLASTPLÅT
C	MÖNSTERPRÄGLAD ALU-PLÅT

KOMPONENTER

ALxxx	AVLUFTARE
Bxxx	GOLVBRUNN
BLxxx	BLANDARE
DBxxx	DISKBÄNKAR
DM	DISKMASKIN
IL	INSPEKTIONSLUCKA (UTFÖRS AV BE)
KM	KOMBI-MASKIN
RLx	RENSRÖR, MED LOCK
SL1	SERVICELUCKA, 150x150, INGÅR I BE
TM	TVÄTTMASKIN
TSxxx	TVÄTTSTÄLL
VL0xxx	VATTENLÅS
VKxxx	VATTENKLOSETT


ÖVRIGT

ANSL	ANSLUTNING
CL	CENTRUMLINJE
FG	FÄRDIGT GOLV
ÖFG	ÖVER (FÄRDIGT) GOLV
INK	INKOPPLING
UK	UNDERKANT
VG	VATTENGÅNG
(L)	AVLOPPSLUFTARE

KOPPLINGSLEDNINGAR

FÖLJANDE GÄLLER OM EJ ANNAT ANGES:
DOLDA KV/VV(1-2)-X31

ANSL	KV	VV	S
B	-	-	75
BL	16(15)	16(15)	-
TS	16(12)	16(12)	75
UB	16(12)	16(12)	75
VK	16(12)	-	110

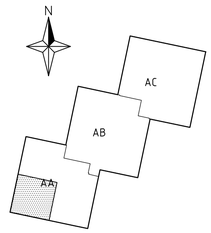

ORIENTERINGSPLAN

REV	ANT	ÄNDRINGEN AVSER	DATUM	SIGN
B		ENL. PM-2	2024-05-07	A.B.
A		ENL. PM-1	2024-04-19	A.B.

BYGGHANDLING

FASTIGHETSBETECKNING
OSTRA KASERN 3

Kristianstads kommun

Västra Storgatan 12
291 80 KRISTIANSTAD
Telefon: 044-13 50 00

	A	
	K	
	V	
	E	
X	L VINNERGI AB	+46 101 02 44 00
	B	
	SK	

ANSVARIG	RITAD/KONSTR AV	HANDLÄGGARE
L.F.	A. B.	L.F.
PROJEKT NR	DATUM	REV.DATUM
2029304	2024-03-01	2024-05-07
OBJEKTKOD	HUS / VÅNING	DISCIPLIN
268140	AA / 01	W

ALLÖSKOLAN - HUS AA
VS-INSTALLATIONER
RÖR UNDER BOTTENPLATTA- DEL 1

FORMAT

SKALA A1 (A3)	RITNINGSNUMMER	BET
1:50 (1:100)	W-50-1-A-0011	B

LAGER

PL0