


XREF: .\1\SVK\SK-model\SK-46-P-0100-1764-A.dwg
.\1\A\A-model\A-40-P-0100-1764-A.dwg
.\1\A\A-model\orient\enrigsfig.dwg
.\Slips\Slips - Skola.dwg

LAGER: SB11

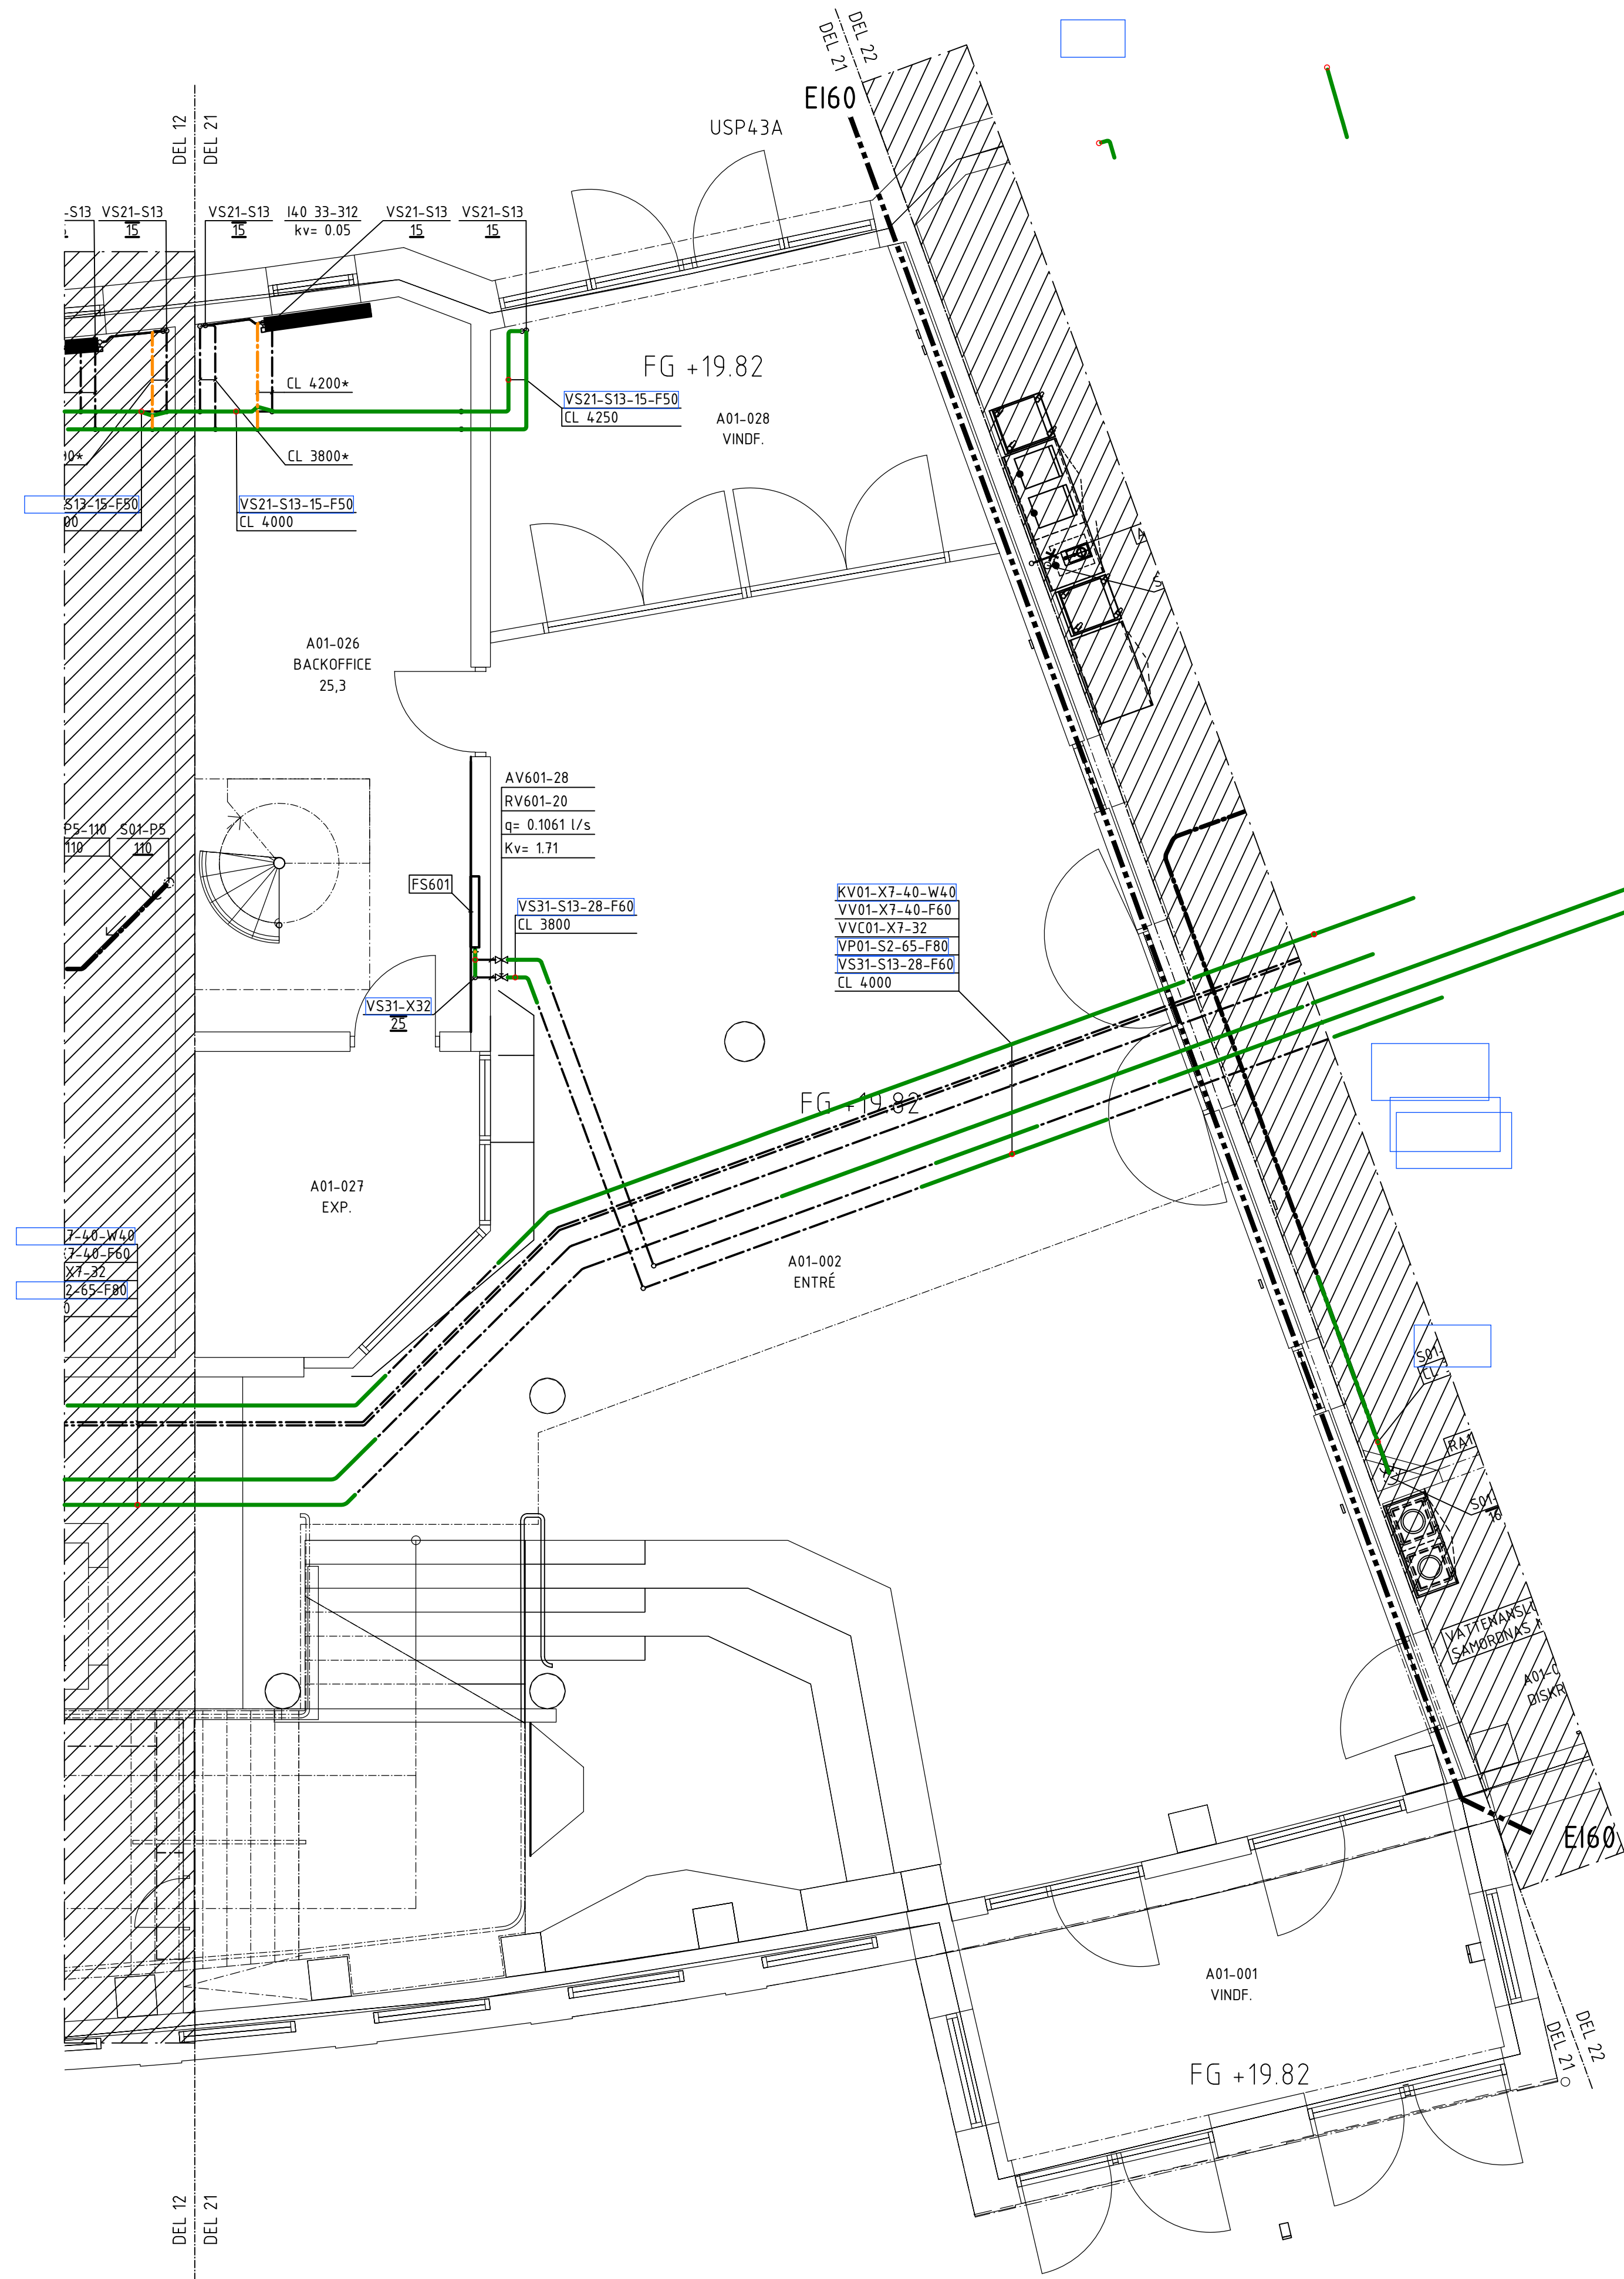

SKALA 1:50 (A1) 0 1 2 3 4 5

FÖRKLARINGAR

BETECKNING RÖRSYSTEM

VS11-S13-42-F100 - (100) mm
(L-F) Ev. isolering.
(42) Dimension
(S13) Rörmaterial
(11) Systemnummer
(VS) Systembeteckning

TAPPVATTENSYSTEM

KV01 Tappkallvatten
KV02 Tappkallvatten, kombiugnar
VV01 Tappvarmvatten
VVC01 Varmvattencirkulation

SPILLVATTENSYSTEM

S01 Spillvatten
SF01 Spillvatten, fettavskiljare

S01 Fall min: 1%
SF01 Fall min: 2%

VÄRMEVATTENSYSTEM

FJV01 Fjärrvärme
VP01 Värmebärare, primär
VS11 Värmebärare, sekundär, ventilation
VS21 Värmebärare, sekundär, radiatorer
VS31 Värmebärare, sekundär, golvvärme

RÖRLEDNINGAR

G3 MA-rör
K5 Kopparrör.Frkr
P2 PP markavloppsror
P3 PP-rör (avlopp inomhus)
P5 PP-rör (avlopp inomhus (juddäpat))
R2 Ledningar av syrafäst stål
R10 Rostfritt avloppsror, muff
S2 Handelsstub, stål
S6 Tryckkärlsstål
S13 Presskopplingsrör utv förs
X7 PAL-RÖR
X31 PEX-RIR
X32 PEX-RIR, extraisolerade

ISOLERING AV INSTALLATIONER

-F Mineralull
-W Mineralull, diffusionstät

VV01 & VVC01 SAMISOLERAS

SAKVAROR

Enl. BESKRIVNING AVSEENDE
VÄRME- OCH SANITETSANLÄGGNING
HANDLINGSNUMMER 11.A.2.1

MÄRKNING AV STYRKOMPONENTER


Föregås av 1764-A-

ÖVRIGT

CL xxxx* = Samma rördimension som
stick och isolering F50

KOPPLINGSLEDNINGAR FRÅN FÖRDELARE TILL APPARAT ENLIGT TABELL OM INGET ANNAT ANGES			
VV01-X31 KV01-X31			
BL			
TS			
UB			
VK			

A	0	PM1-W	230601	K. PERSSON		
BET	ANT	ÄNDRINGEN AVSER	DATUM	SEN		
BYGGHANDLING						
		Malmö stad Stadsfastigheter				
HYLLIE NYA HÖGSTADIUM OCH SPORTHALL 3 PROJEKT NR NYBYGGNAD AV SKOLA OCH SPORTHALL 5800						
						
Sweco Sverige AB - Tele: 08-695 60 00 - www.sweco.se						
FÖRETAG SWECO SVERIGE AB			TEL 040 - 16 70 00			
UPPDRAGSNUMMER 30025113		RITAD AV K. PERSSON		HANDLAGARE D. HAGSTRÖM		
DATUM 2023-01-31		REV. DATUM 2023-06-01		ANSVARIG J. ÅKESSON		
RUNDSTICKAN 1 RÖRINSTALLATIONER HUS A PLAN 1 DEL 21						
OBJEKTSNUMMER		BYGGNAD	PLAN	DEL	UNDERGRUPP	DISCIPLIN
1764		A	01	21	50	W
SKALA		RITINGSNUMMER			BET	
1:50		V-50-1-A0121			A	

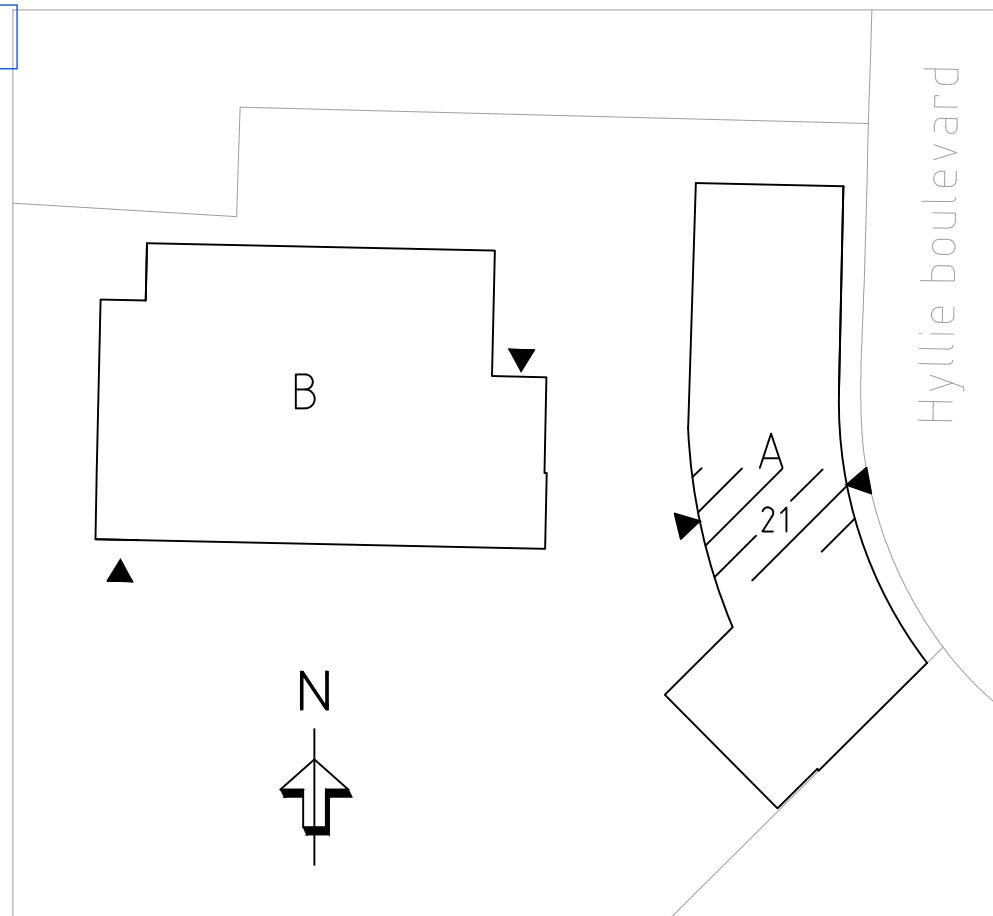

FILE: .\1\SVK\SK-model\SK-46-P-0100-1764-A.dwg PROJECT: 30025113 HYLLIE NYA HÖGSTADIUM OCH SPORTHALL 30025113 FILE: .\1\A\A-model\orient\enrigsfig.dwg PROJECT: 5800